

FOURTH FLOOR			
NO	LENGTH	WIDTH	TOTAL
C	13.49	20.45	275.59
DEDUCTION			
NO	LENGTH	WIDTH	TOTAL
1	1.60	x 3.50	6.30
2	9.63	x 7.20	69.54
3	4.13	x 1.65	6.81
4	2.55	x 1.25	3.19
5	2.55	x 1.25	3.19
6	2.44	x 0.50	1.22
7	6.69	x 4.40	29.44
TOTAL			119.55

BUILT-UP AREA FOURTH FLOOR			
NO	C	DEDUCTION	TOTAL
TOTAL	275.59	119.55	156.02







THIRD FLOOR			
NO	LENGTH	WIDTH	TOTAL
C	13.6'	23.45	275.82

DEDUCTION			
NO	LENGTH	WIDTH	TOTAL
1	1.80	X 3.50	6.30
2	2.85	X 3.50	10.00
3	2.55	X 1.25	3.19
TOTAL			19.50


BUILT-UP AREA THIRD FLOOR			
NO	C	DEDUCTION	TOTAL
TOTAL	275.82	- 19.50	260.12

SECOND FLOOR				
NO	LENGTH	WIDTH	TOTAL	
C	13.49	20.25	275.87	
DEDUCTION				
NO	LENGTH	WIDTH	TOTAL	
I	1.80	x	6.30	
TOTAL			6.30	

BUILDUP AREA SECOND FLOOR				
NO	C	WIDTH	TOTAL	
TOTAL	275.87	-	6.30	269.57

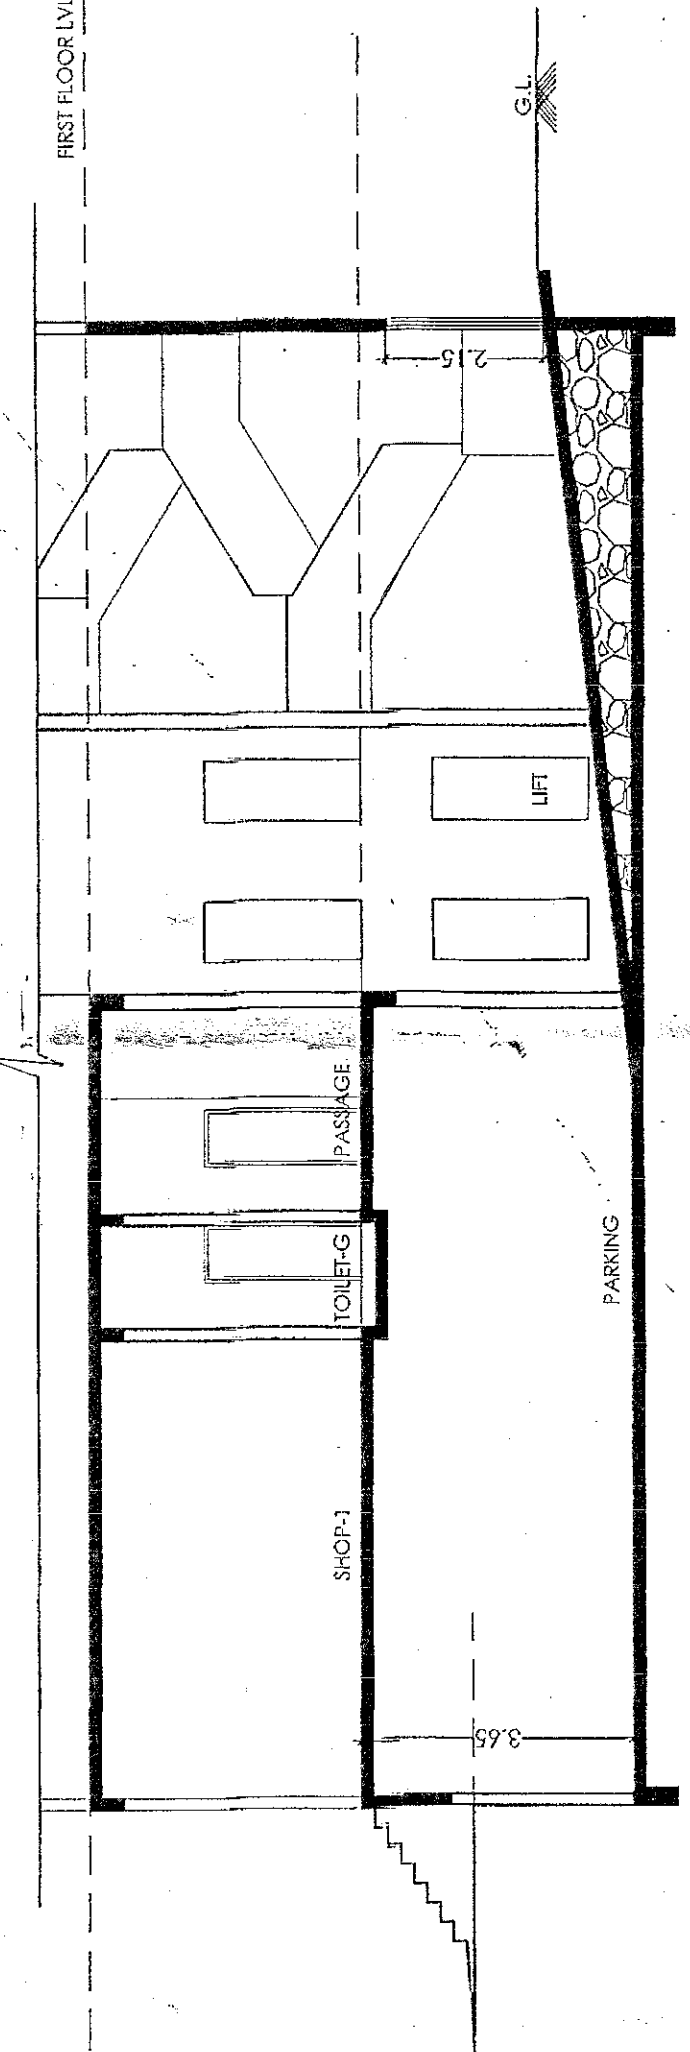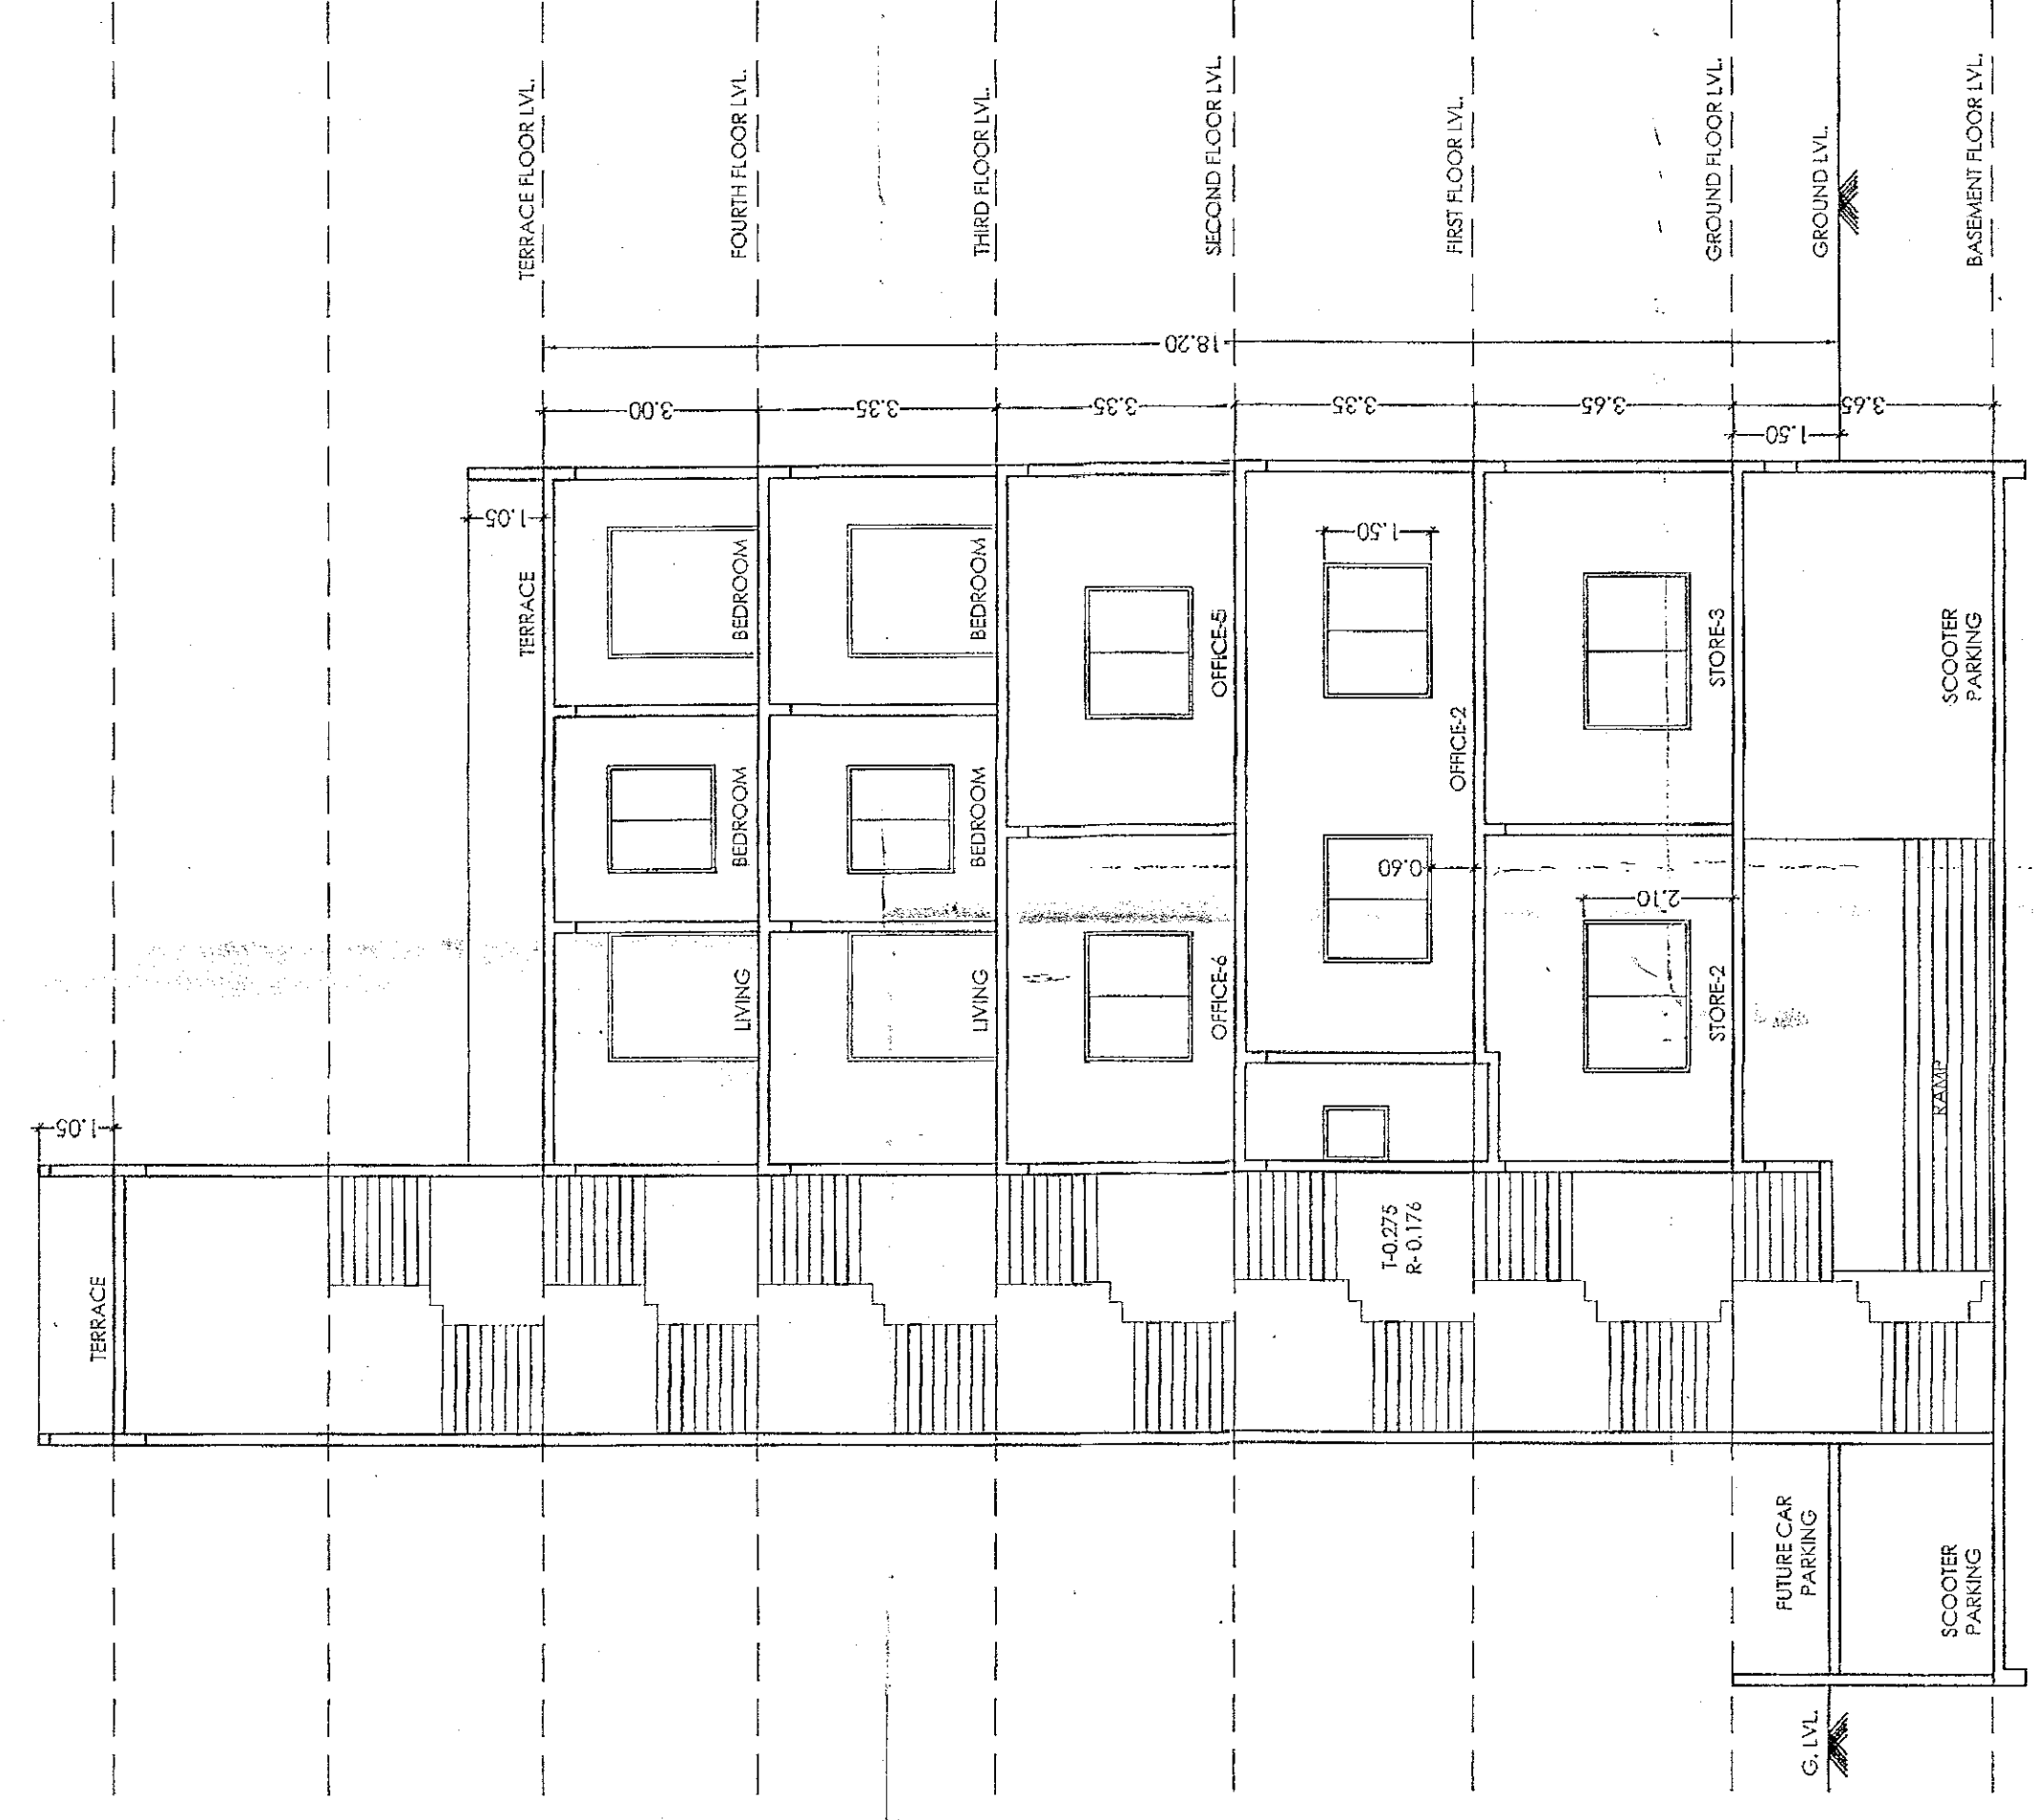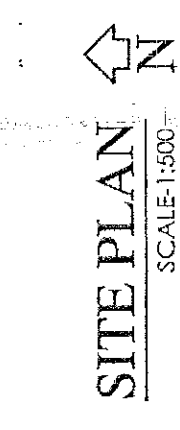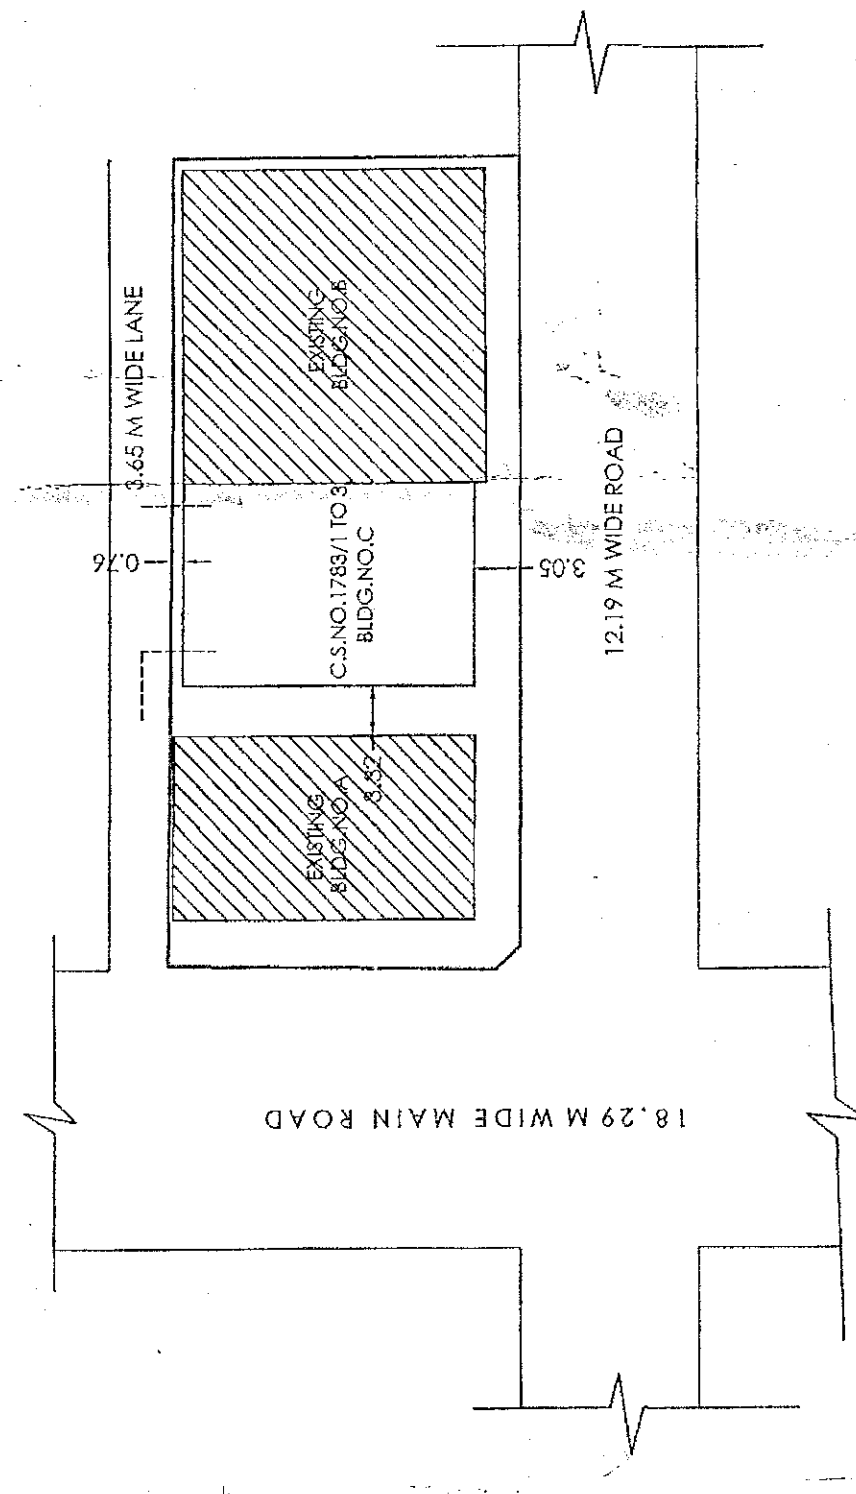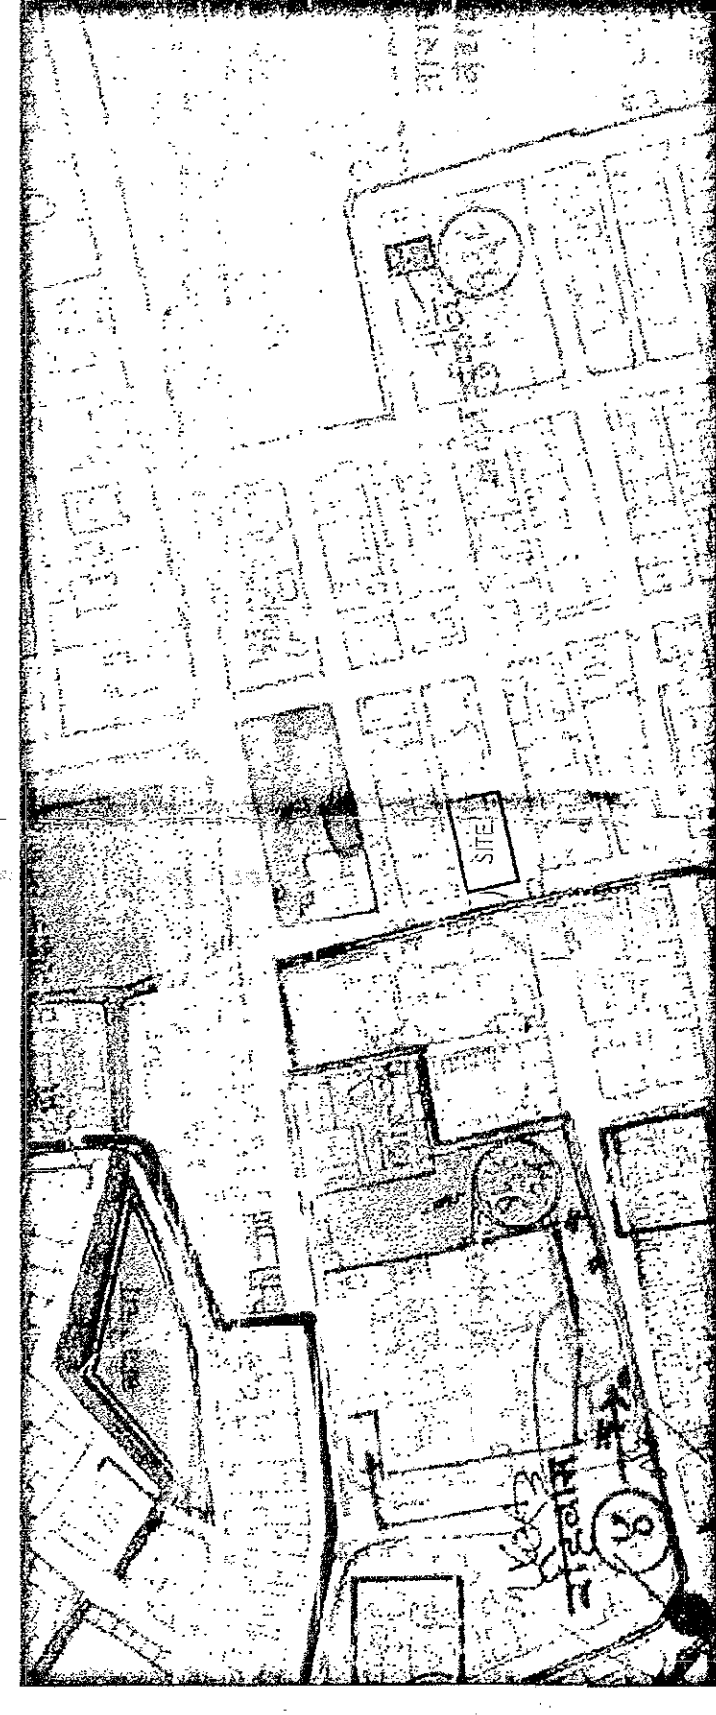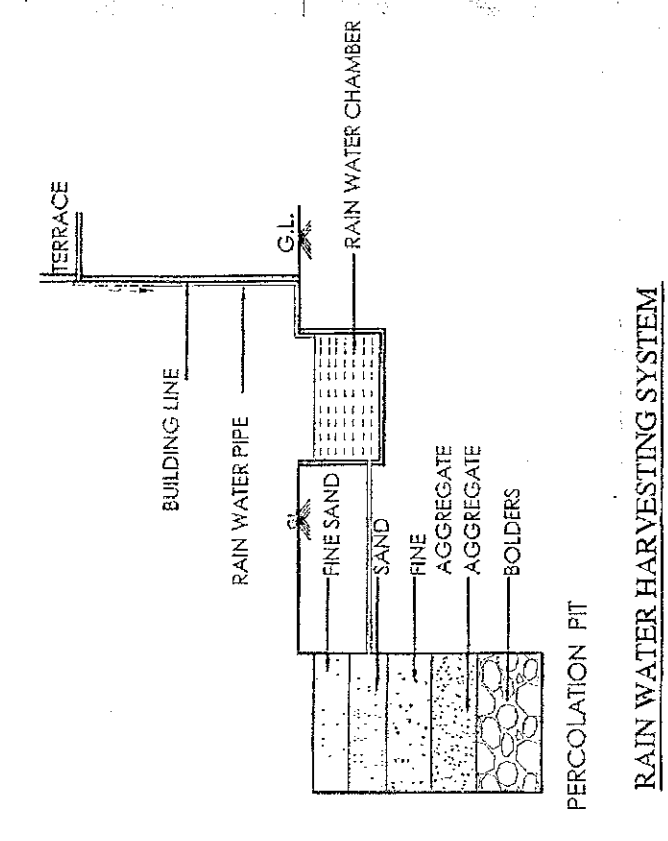

SECTION THOROUGH RAMP

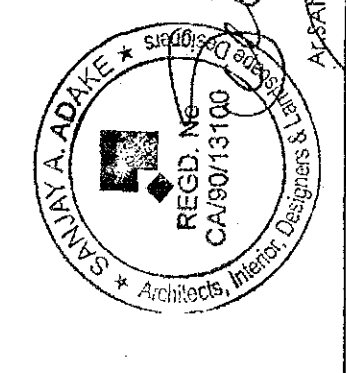


PROPOSED COMM./RESI. COMPLEX ON C.S.NO.
1783/1 TO 3'E WARD, RAJARAMPURI SECOND LANE,
KOLHAPUR FOR-
SHRI. DEEPAK BALASAHEB WAGHULE AND
SOU.POOJA DEEPAK WAGHULE.

DRG.NO.	JOB NO.	DATE	SCALE	DRNBY	CHD.BY
		21/06/2021	1:100		


■ SANJAY A. ADAKE.
ARCHITECTS AND INTERIOR DESIGNERS
"SRUSHTI MAHABHARAT," C.S. NO. 2508/22, 'E' WARD,
NAGALA PARK KOLHAPUR,
REGD. NO. CA - 90/13100
PHONE NO. 2656448
E-MAIL = sanjay9008@gmail.com

SHRI. DEEPAK BALASAHEB WAGHULE SOU. POOJA DEEPAK WAGHULE
SIGN OF OWNER'S


... SO
SIGN OF OWNER'S

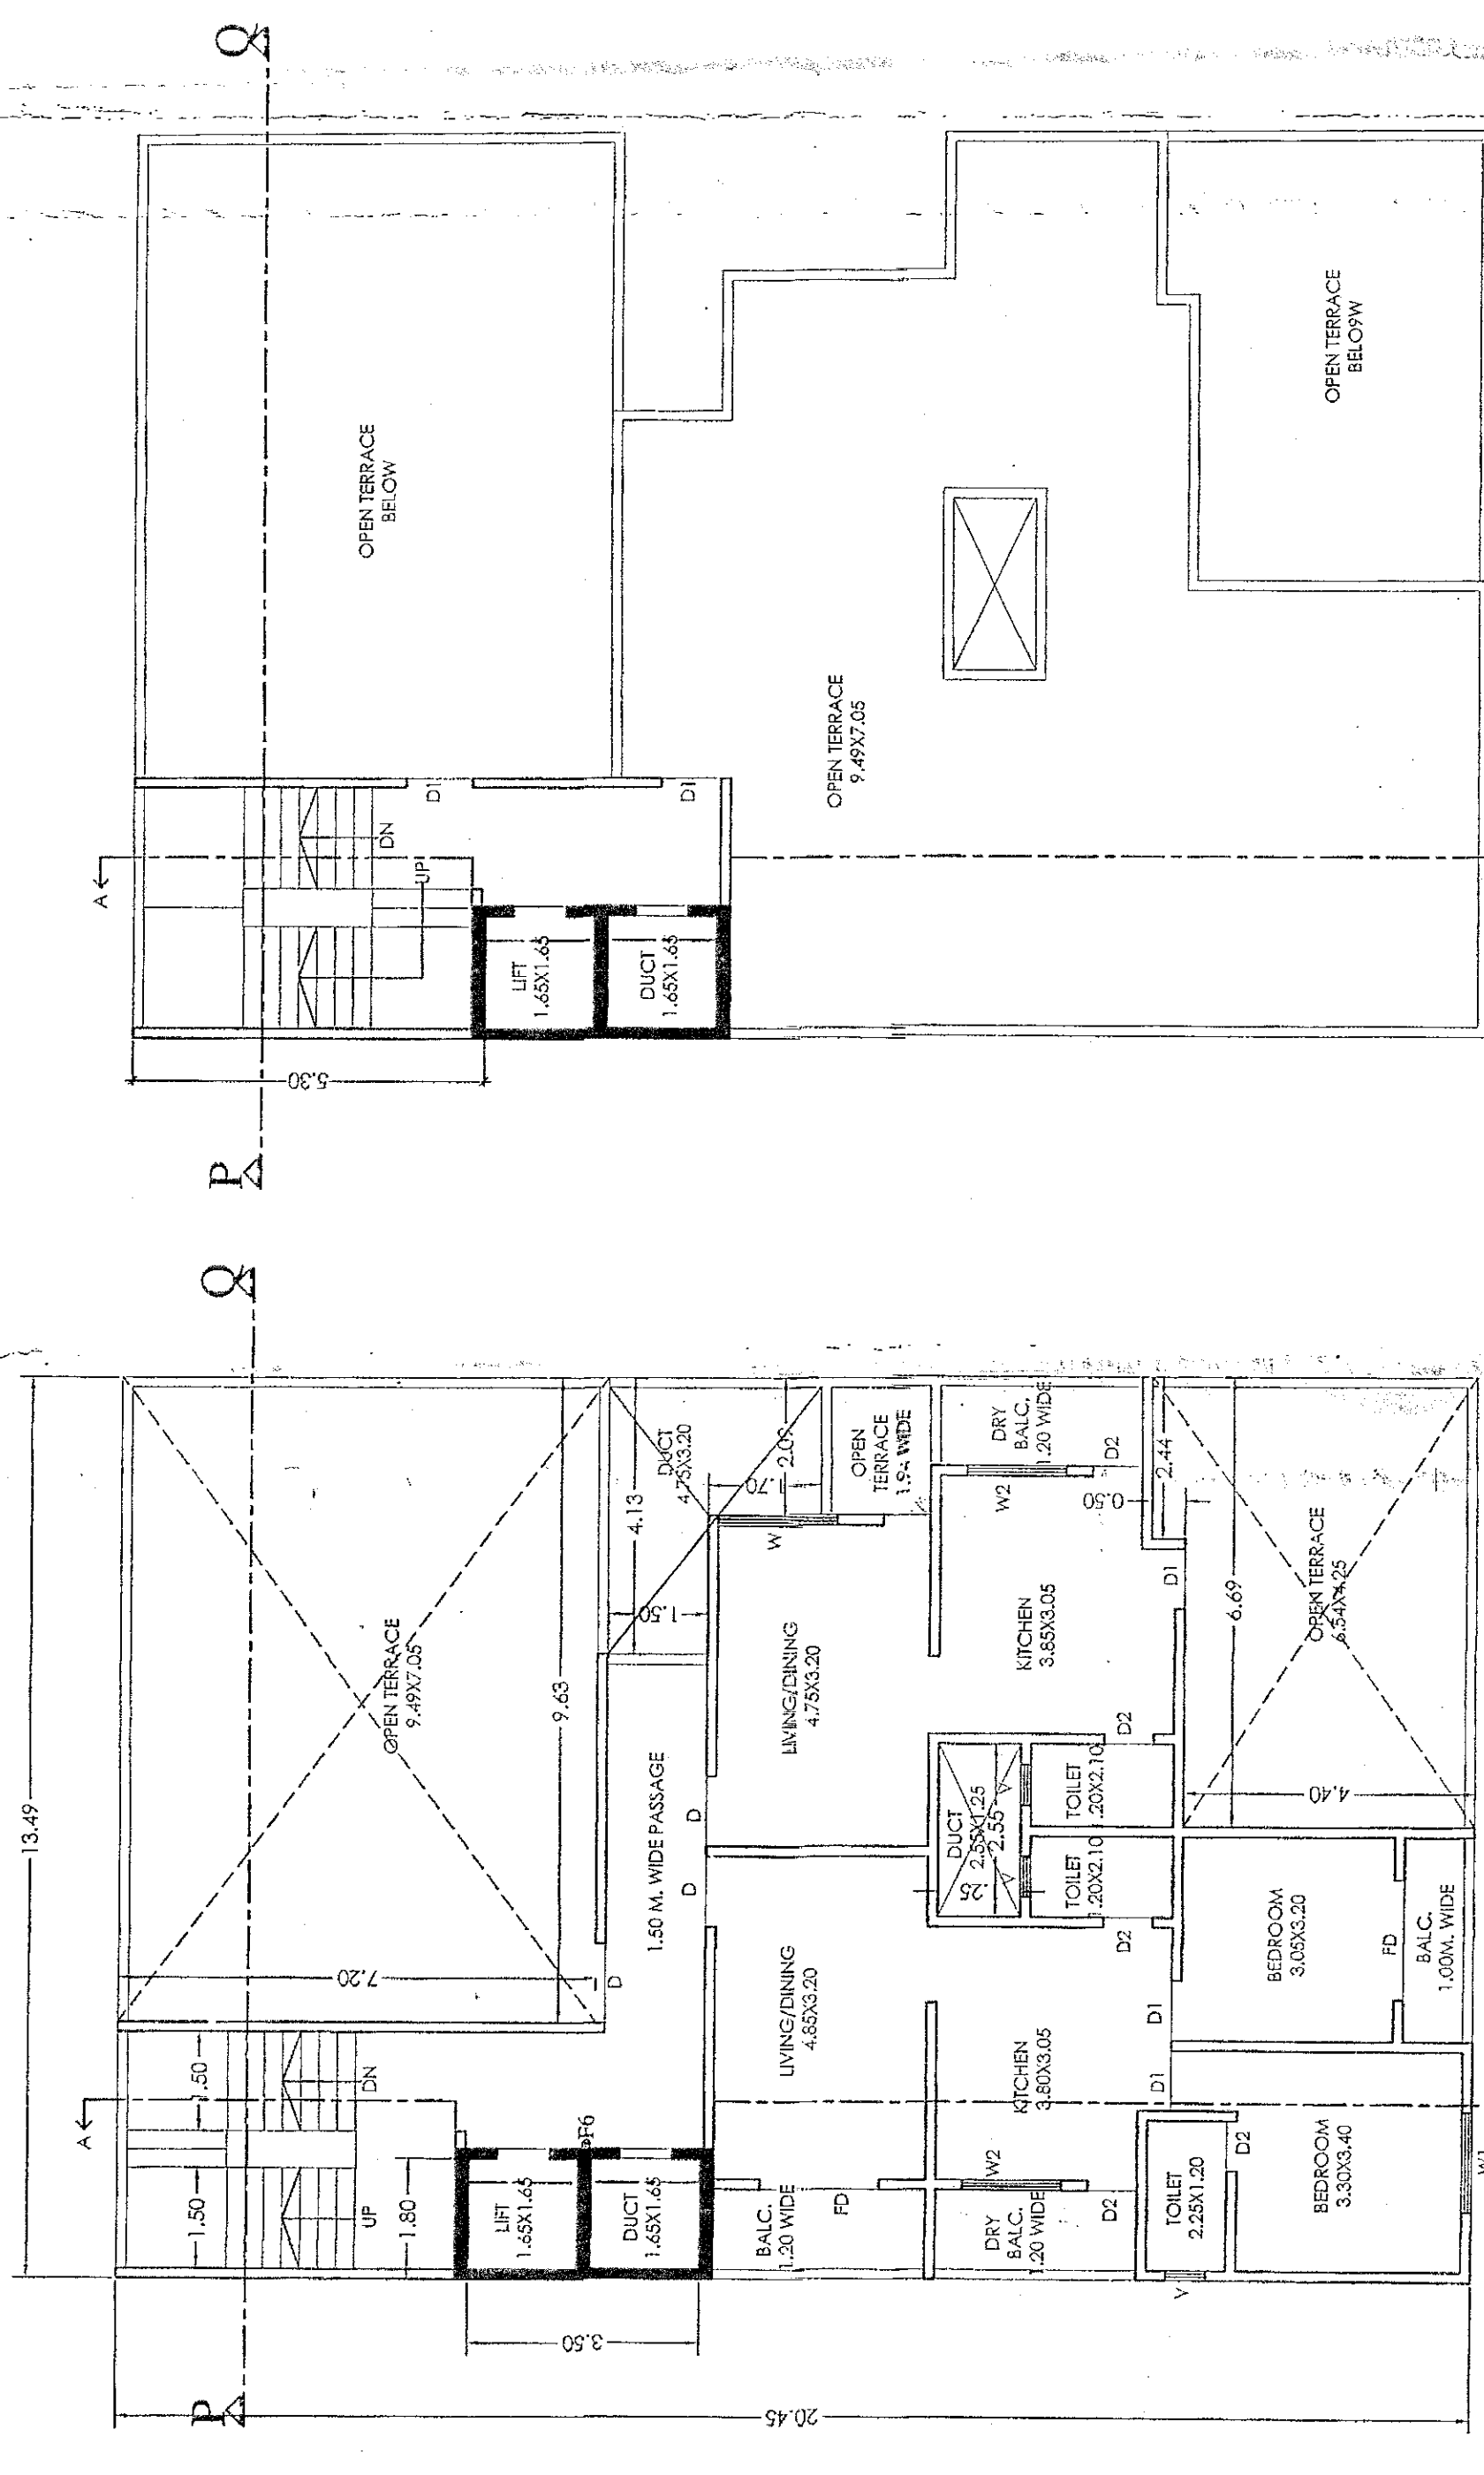

FOURTH FLOOR PLAN

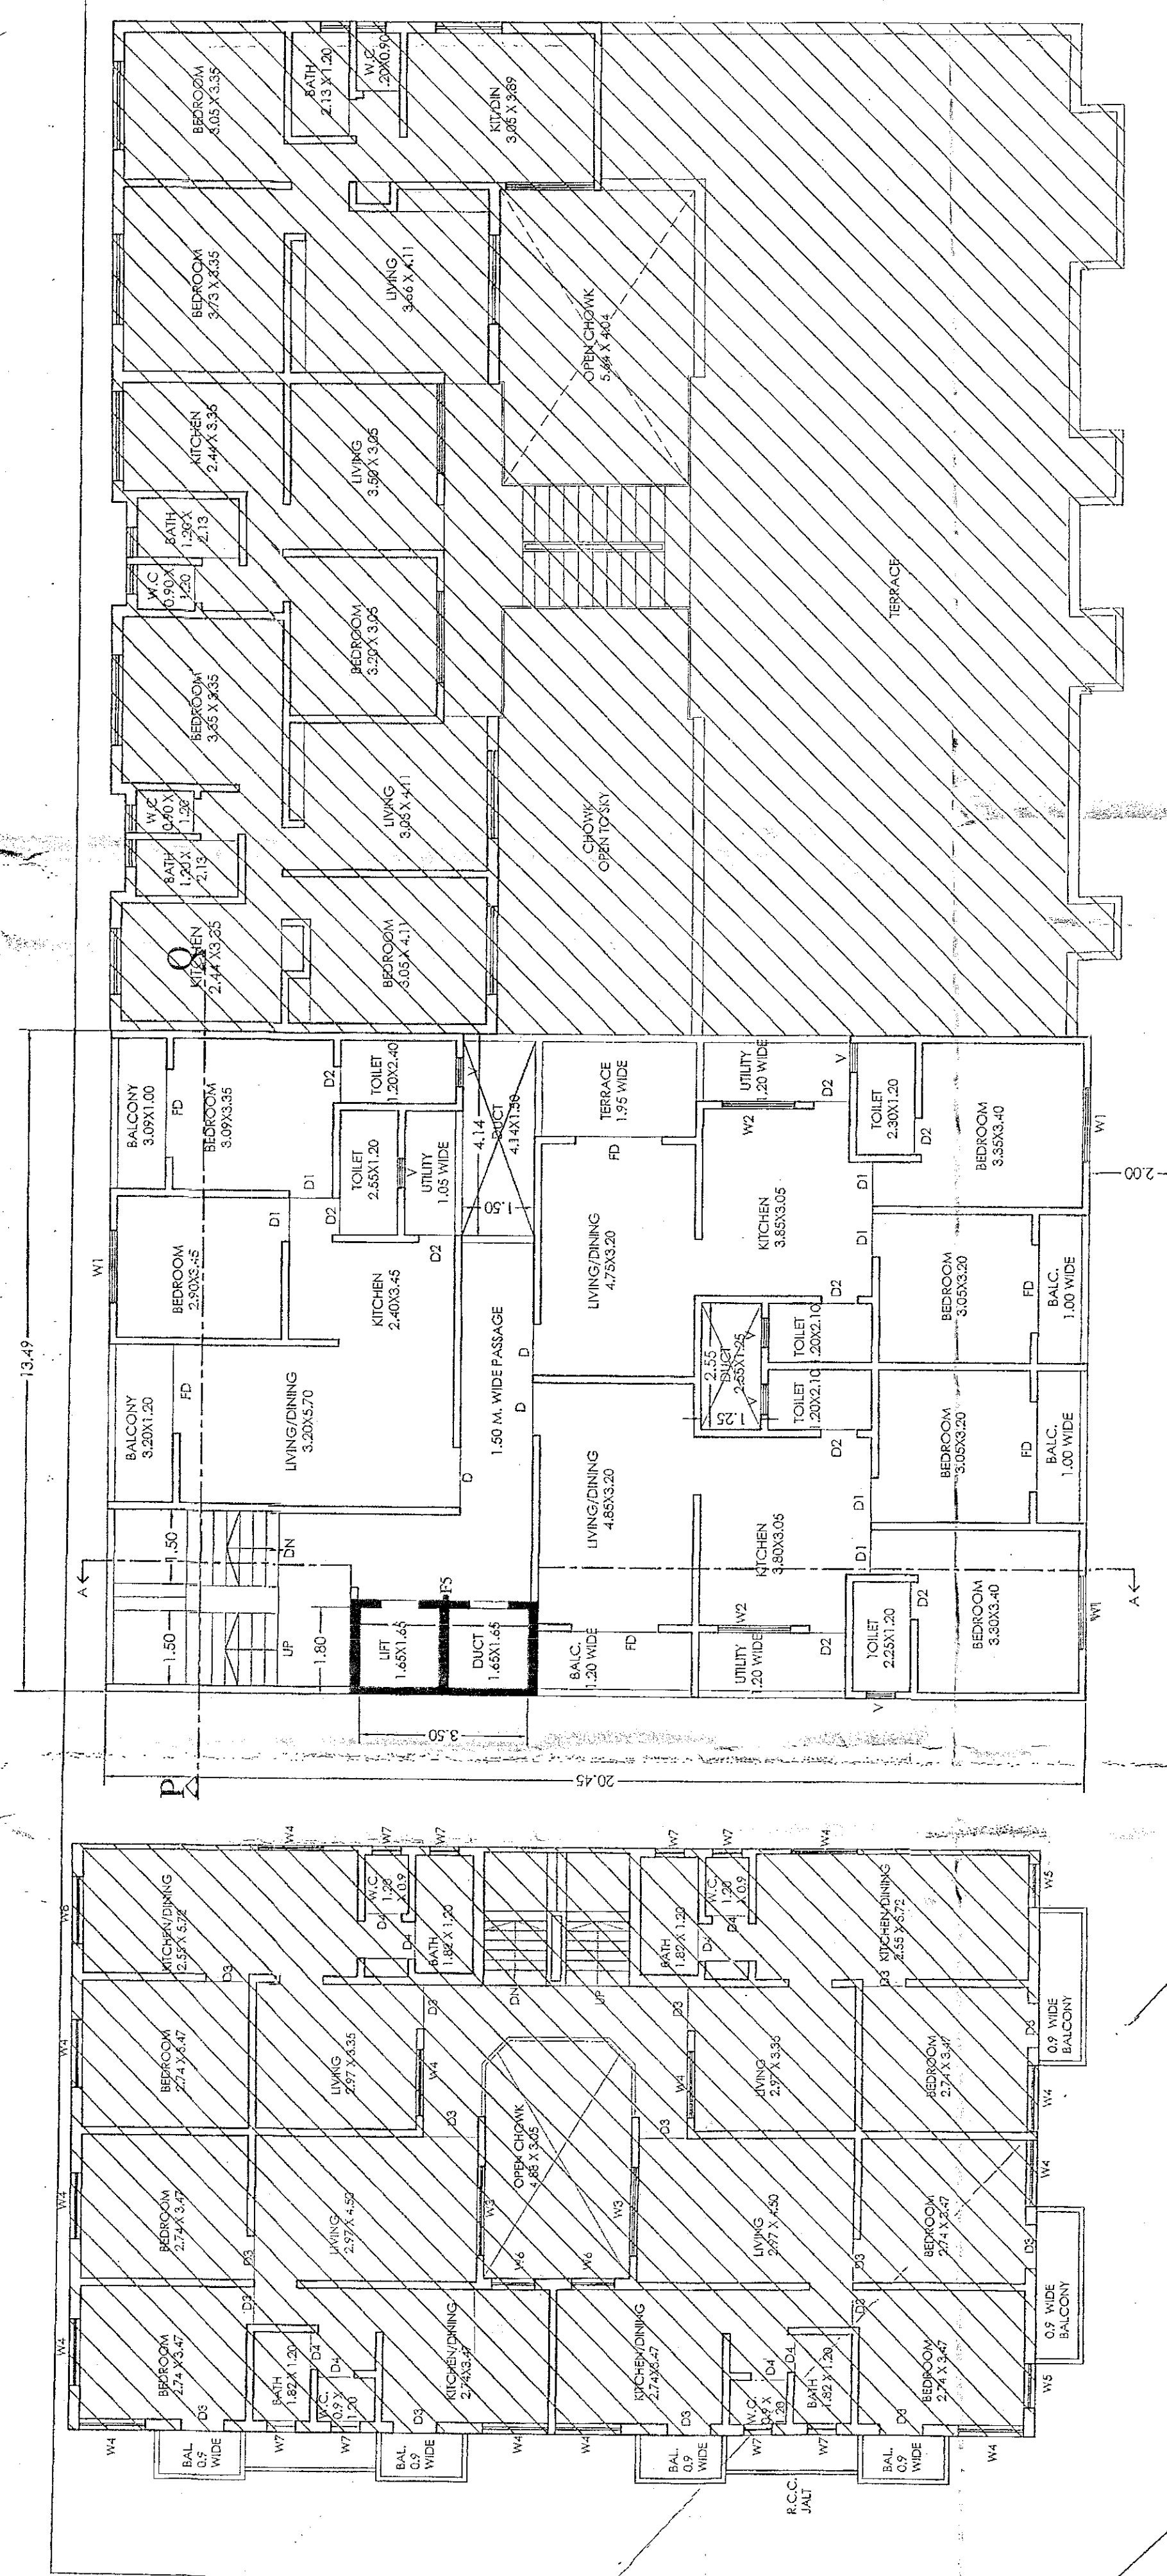

TERRACE FLOOR PLAN

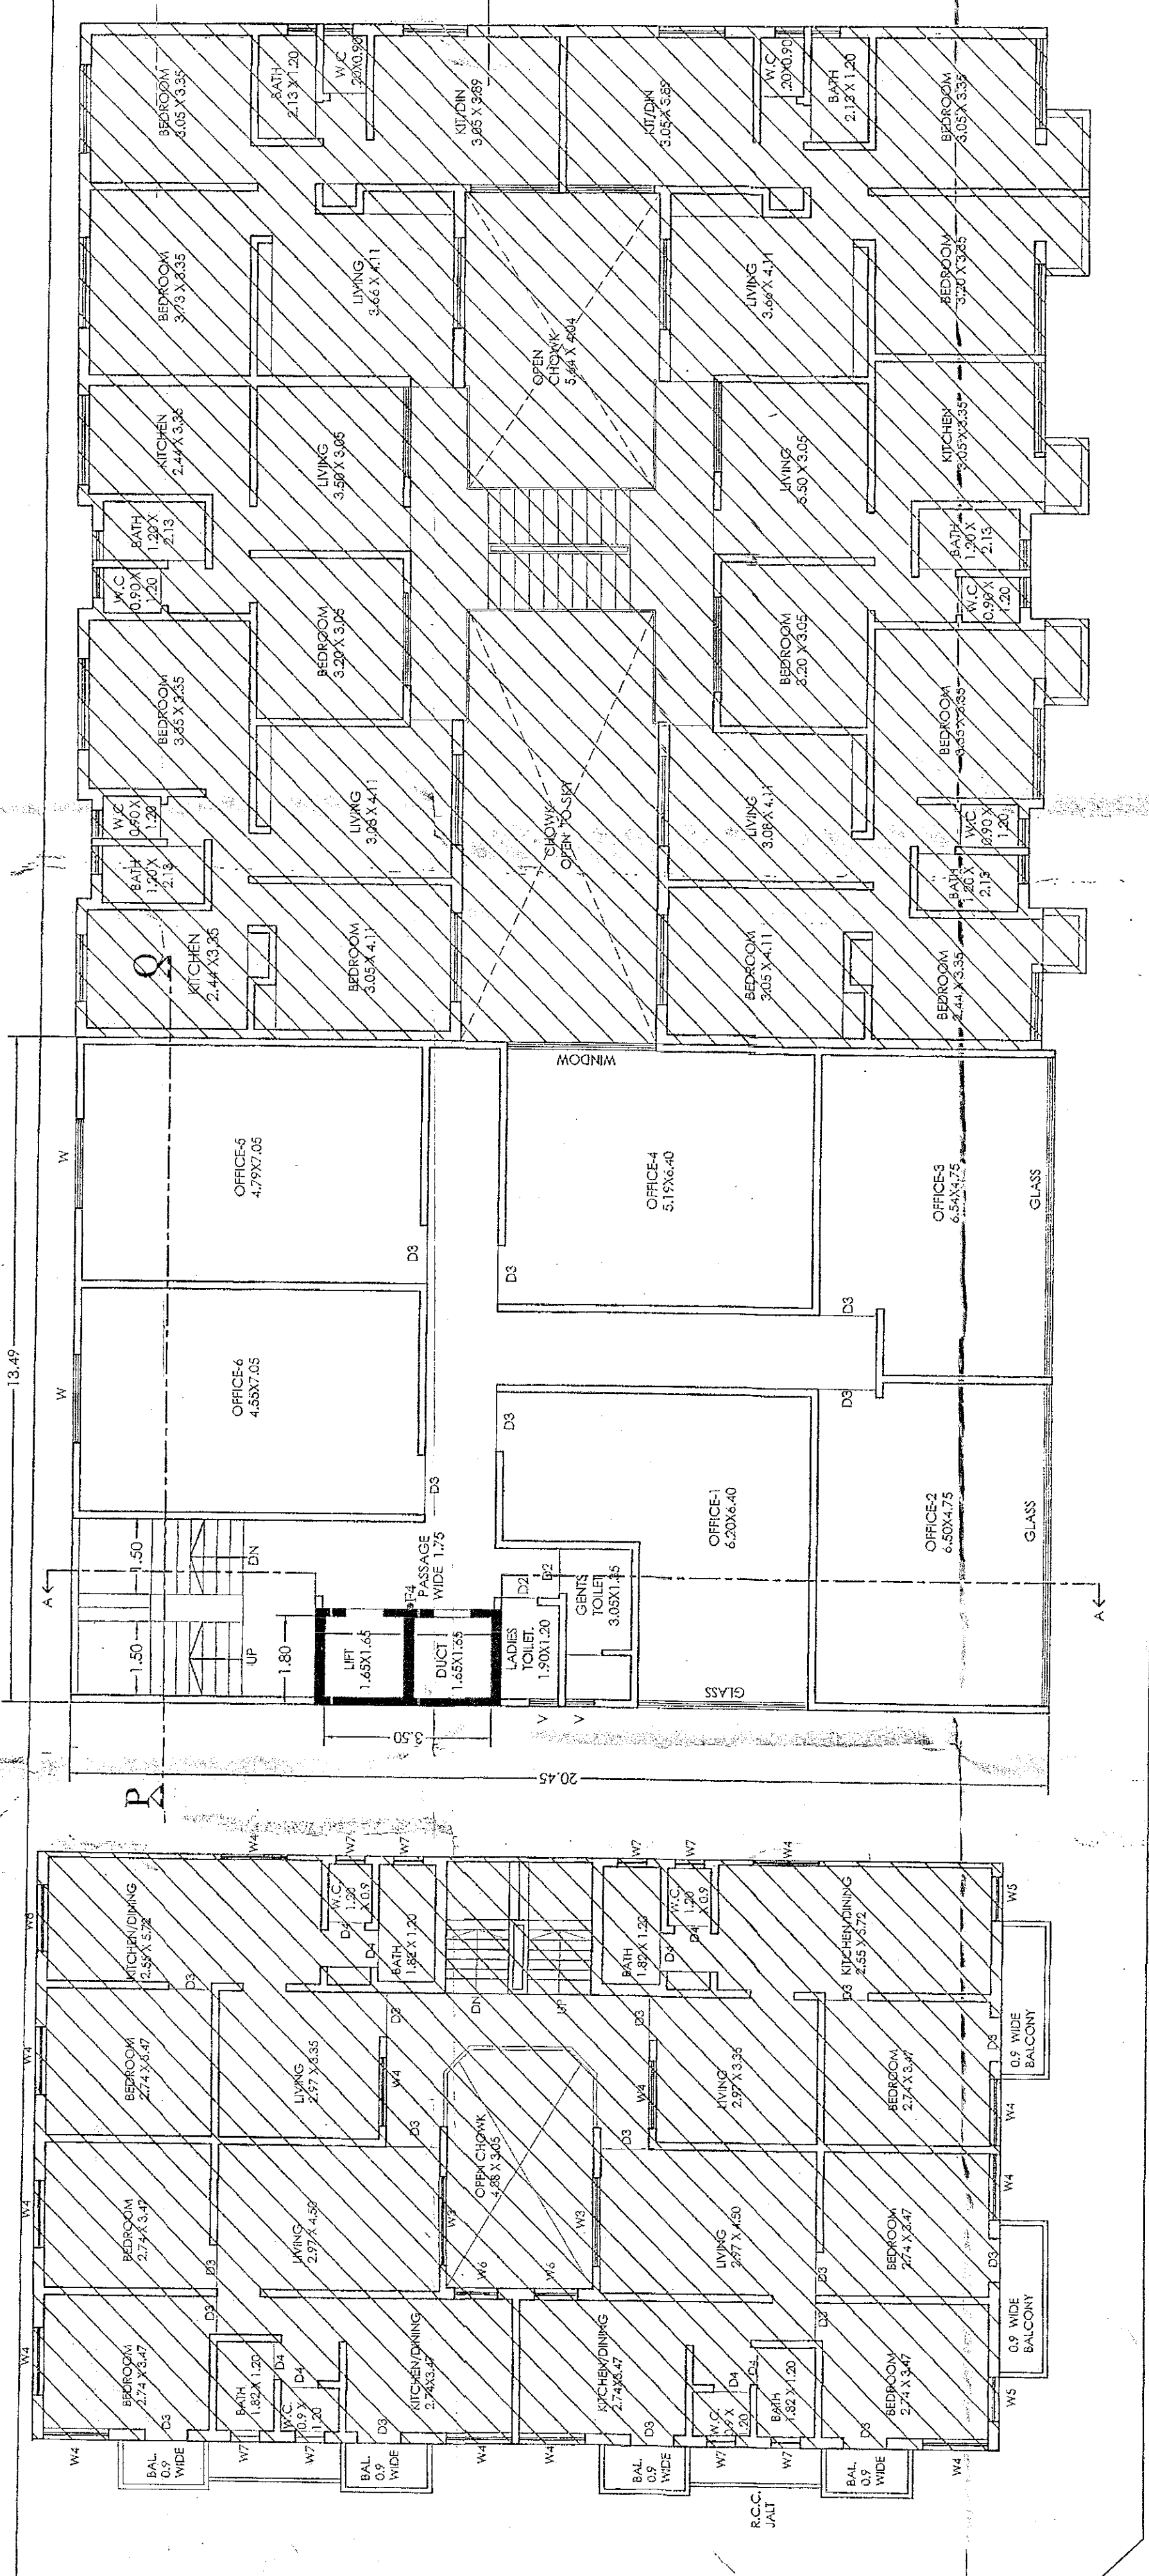

SECOND FLOOR PLAN