
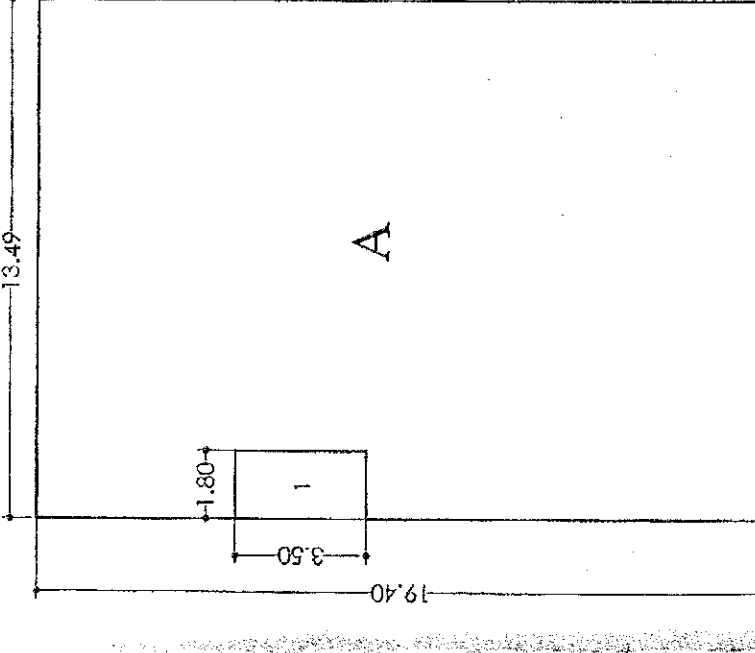
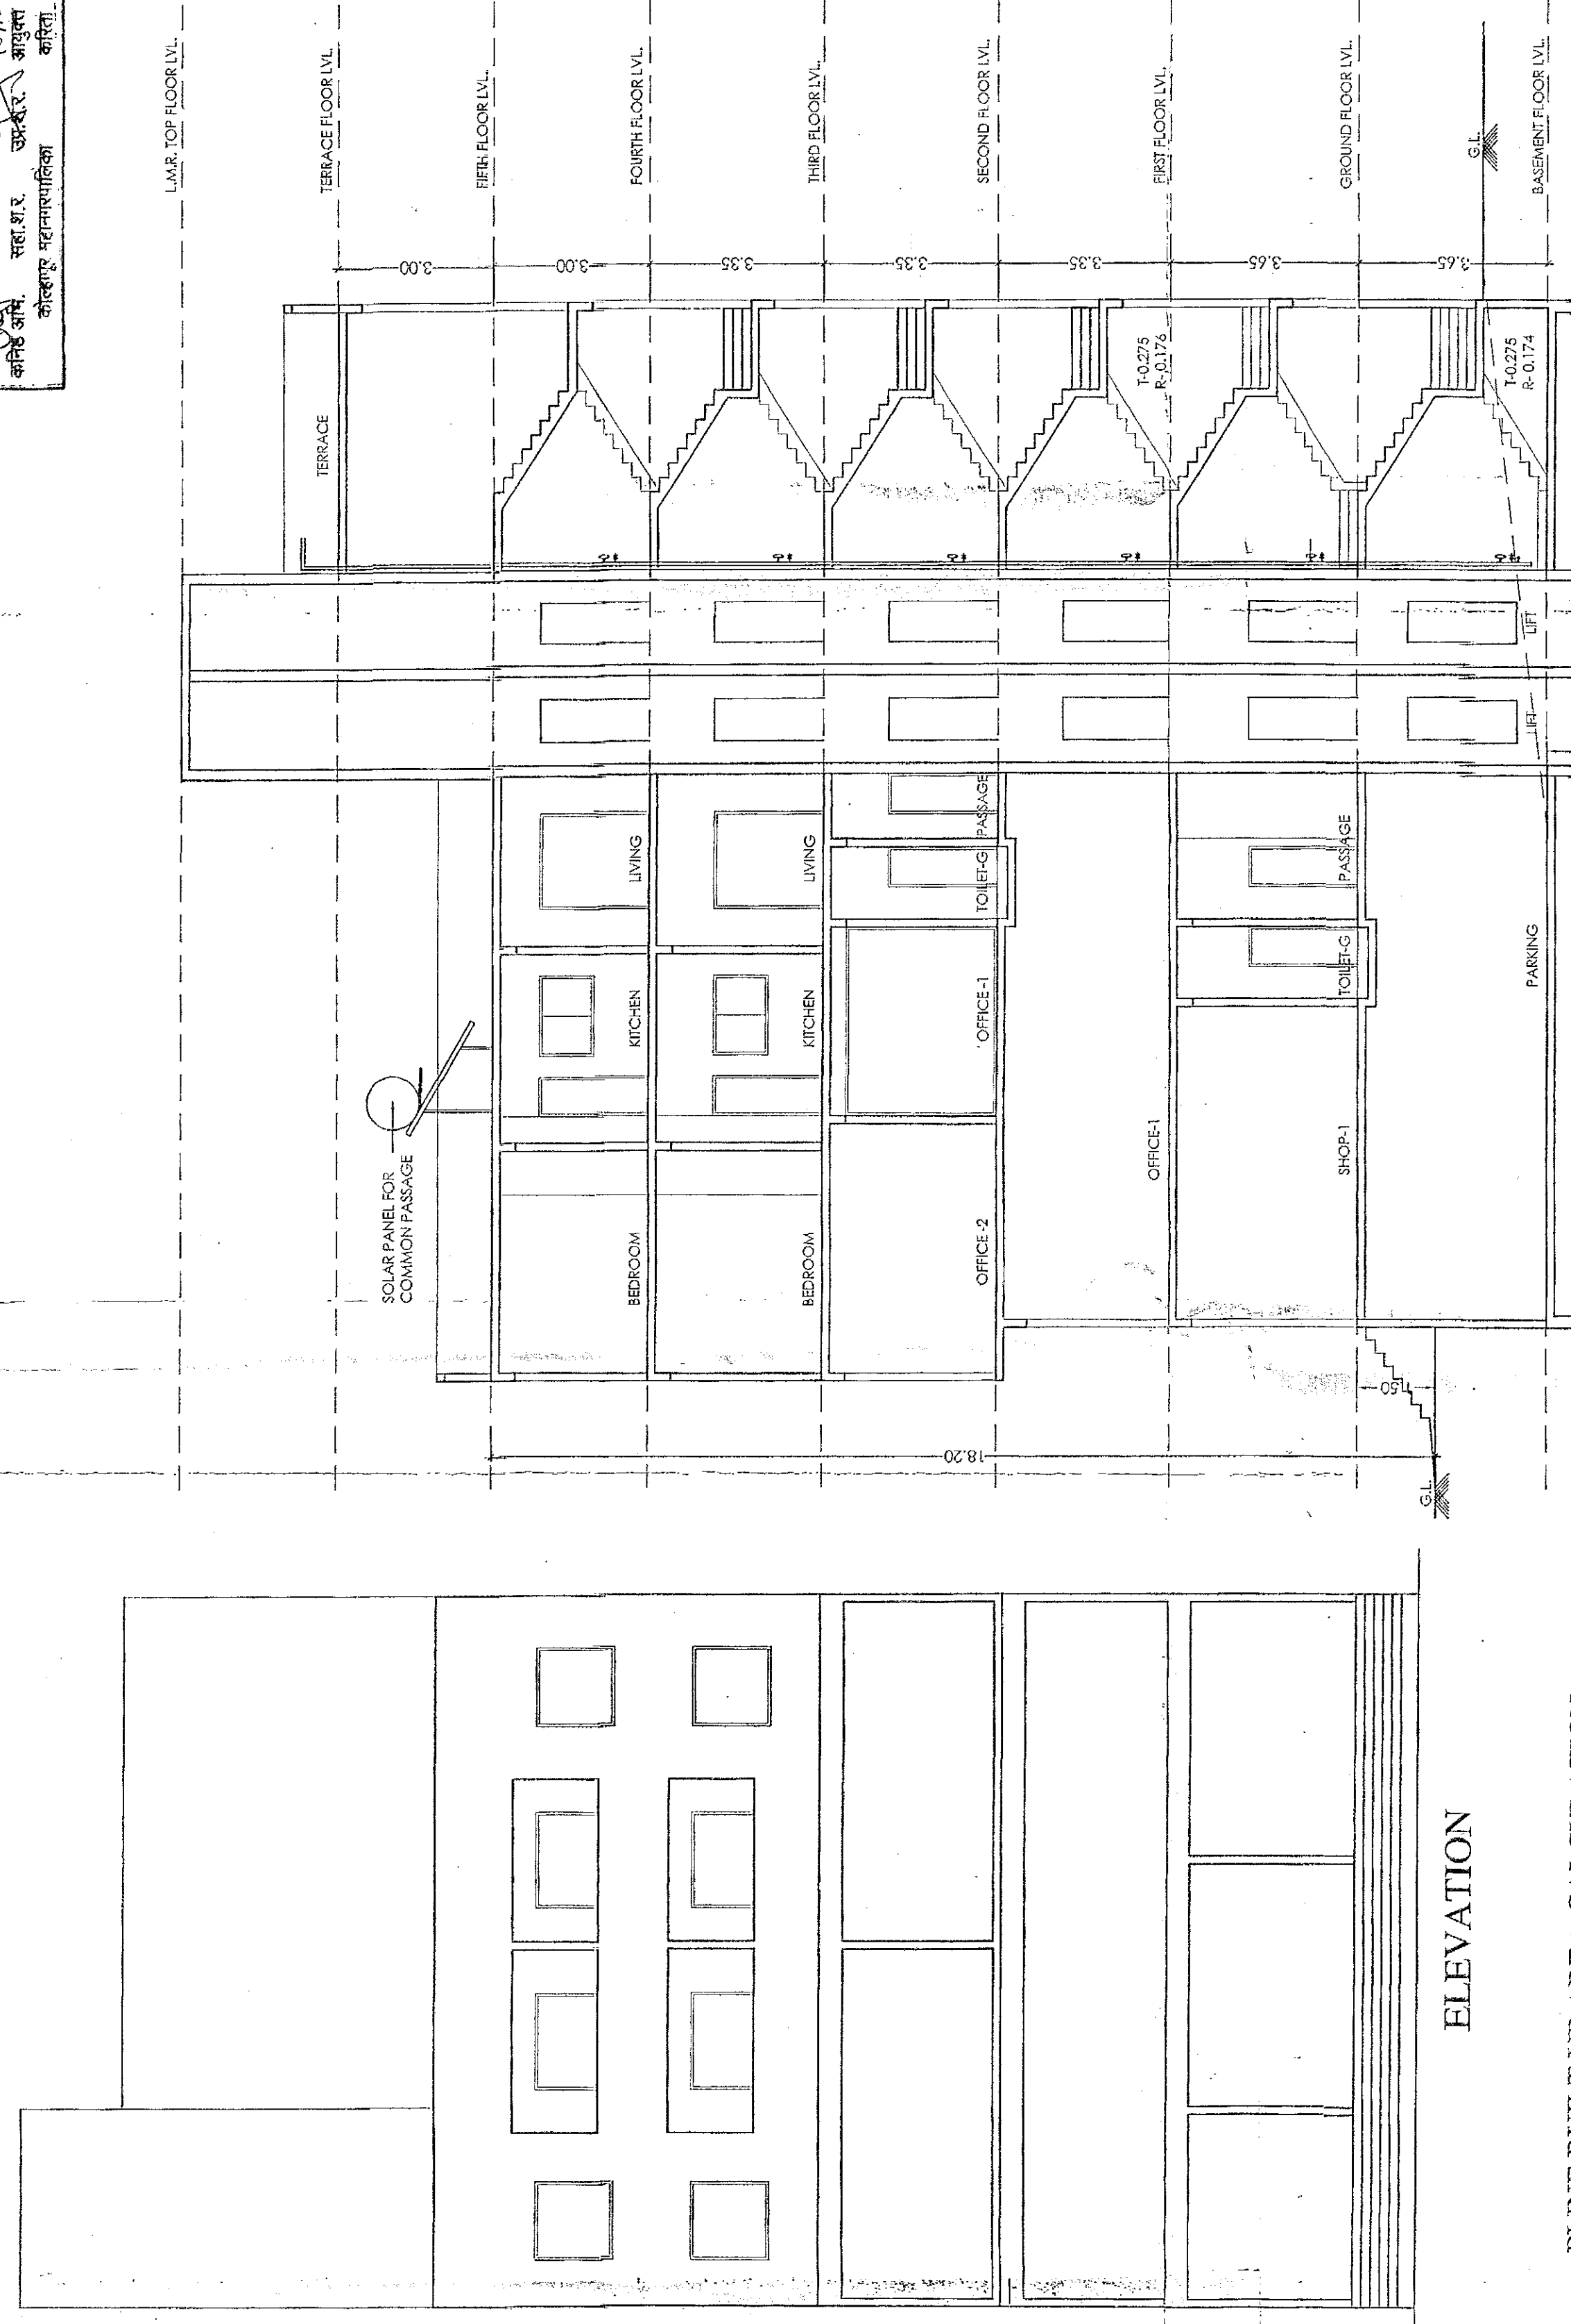
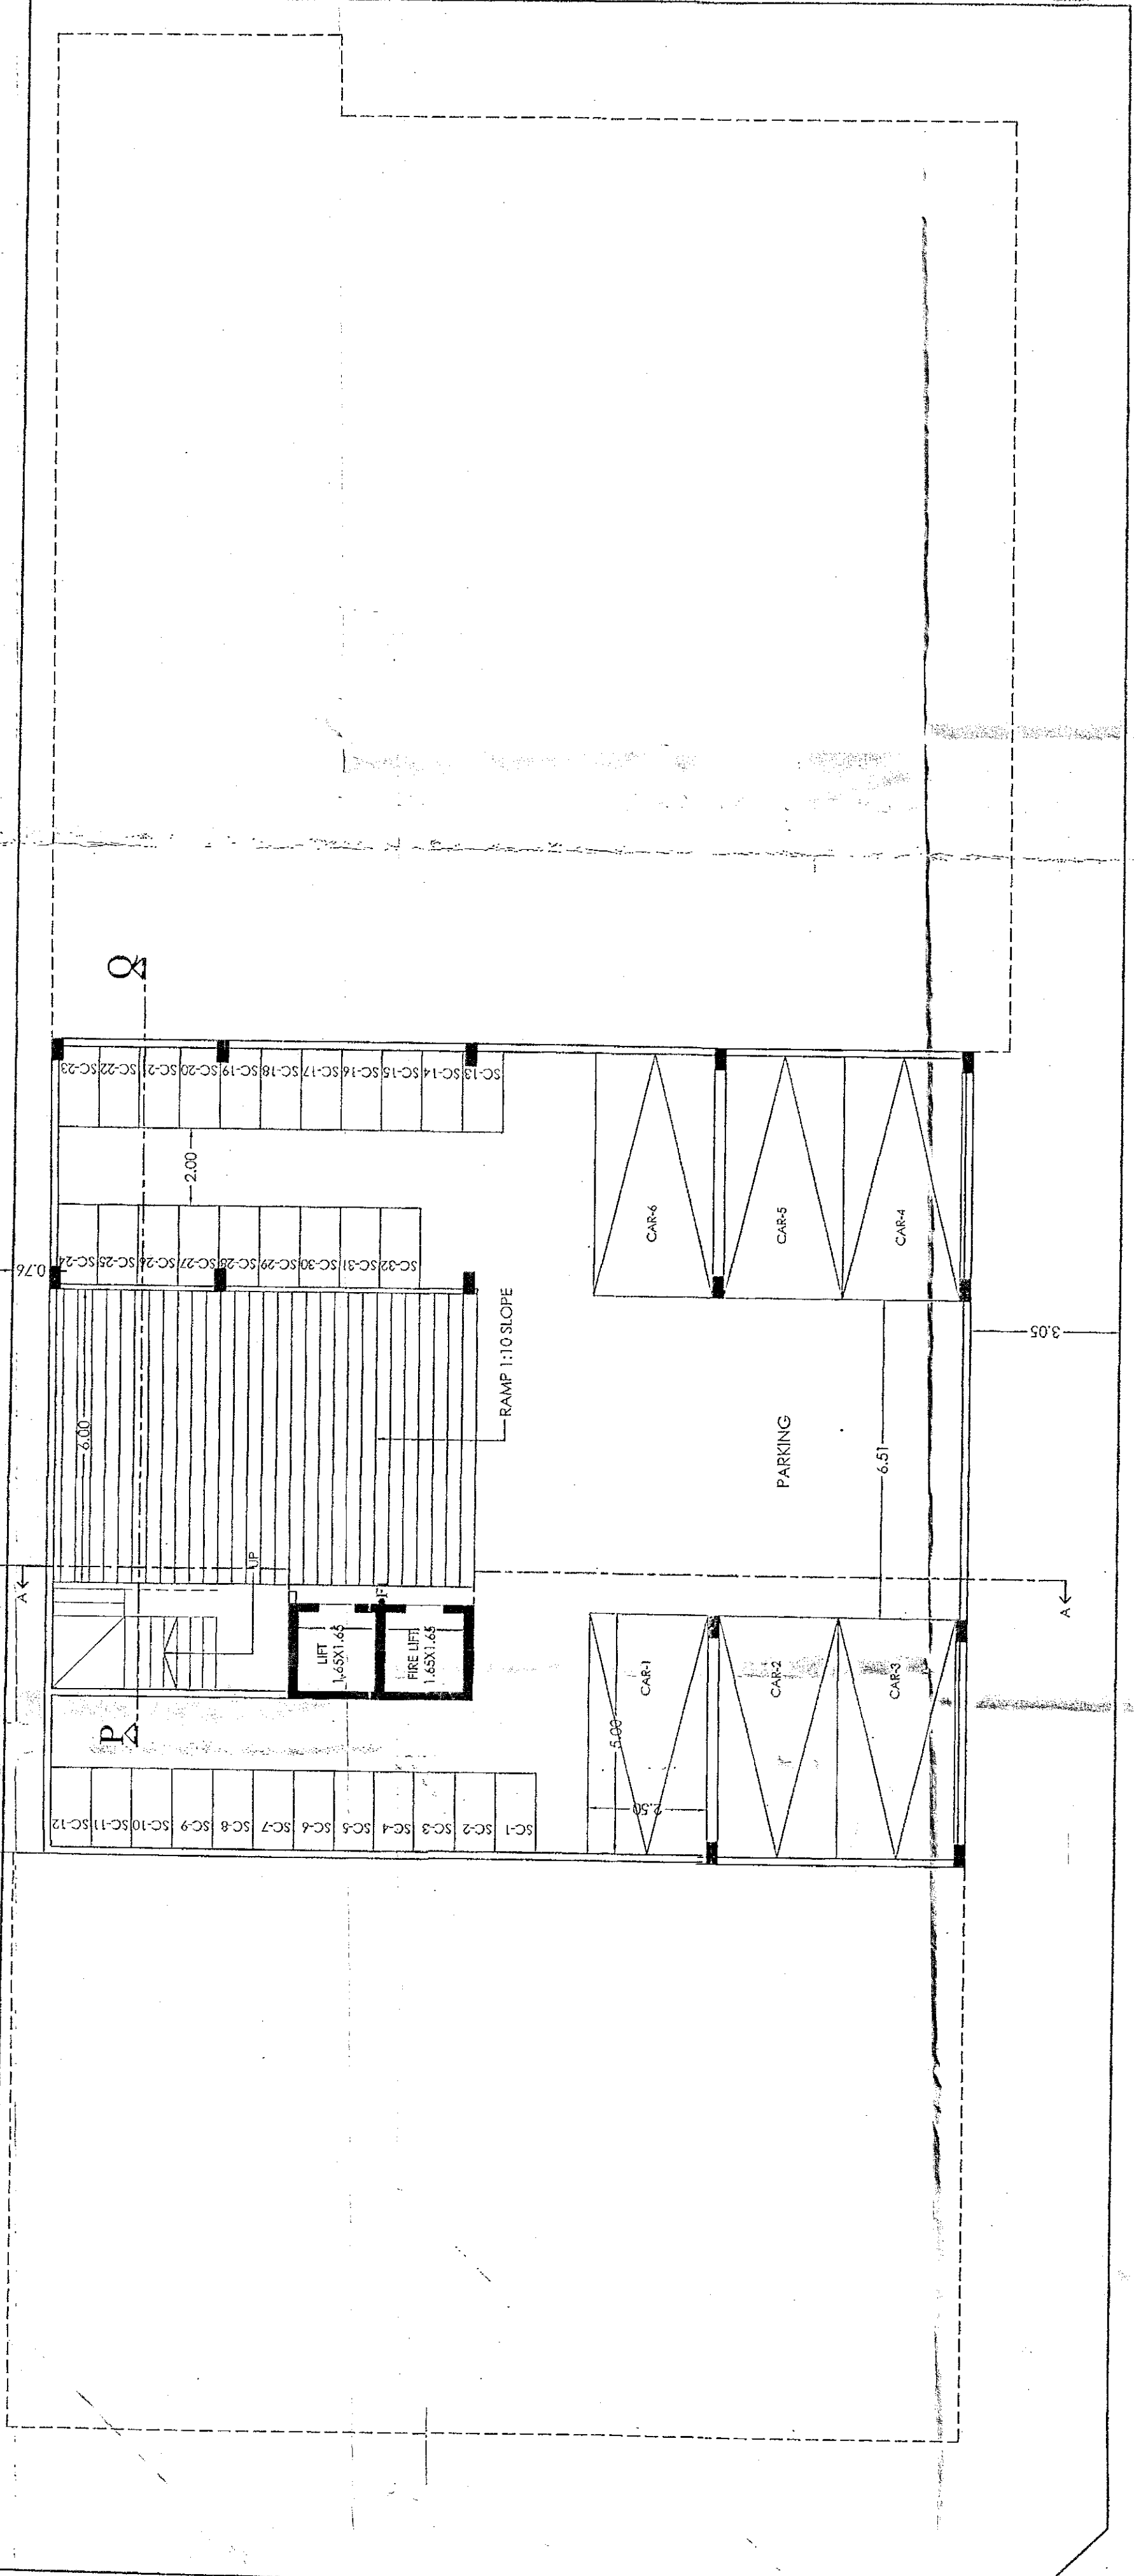
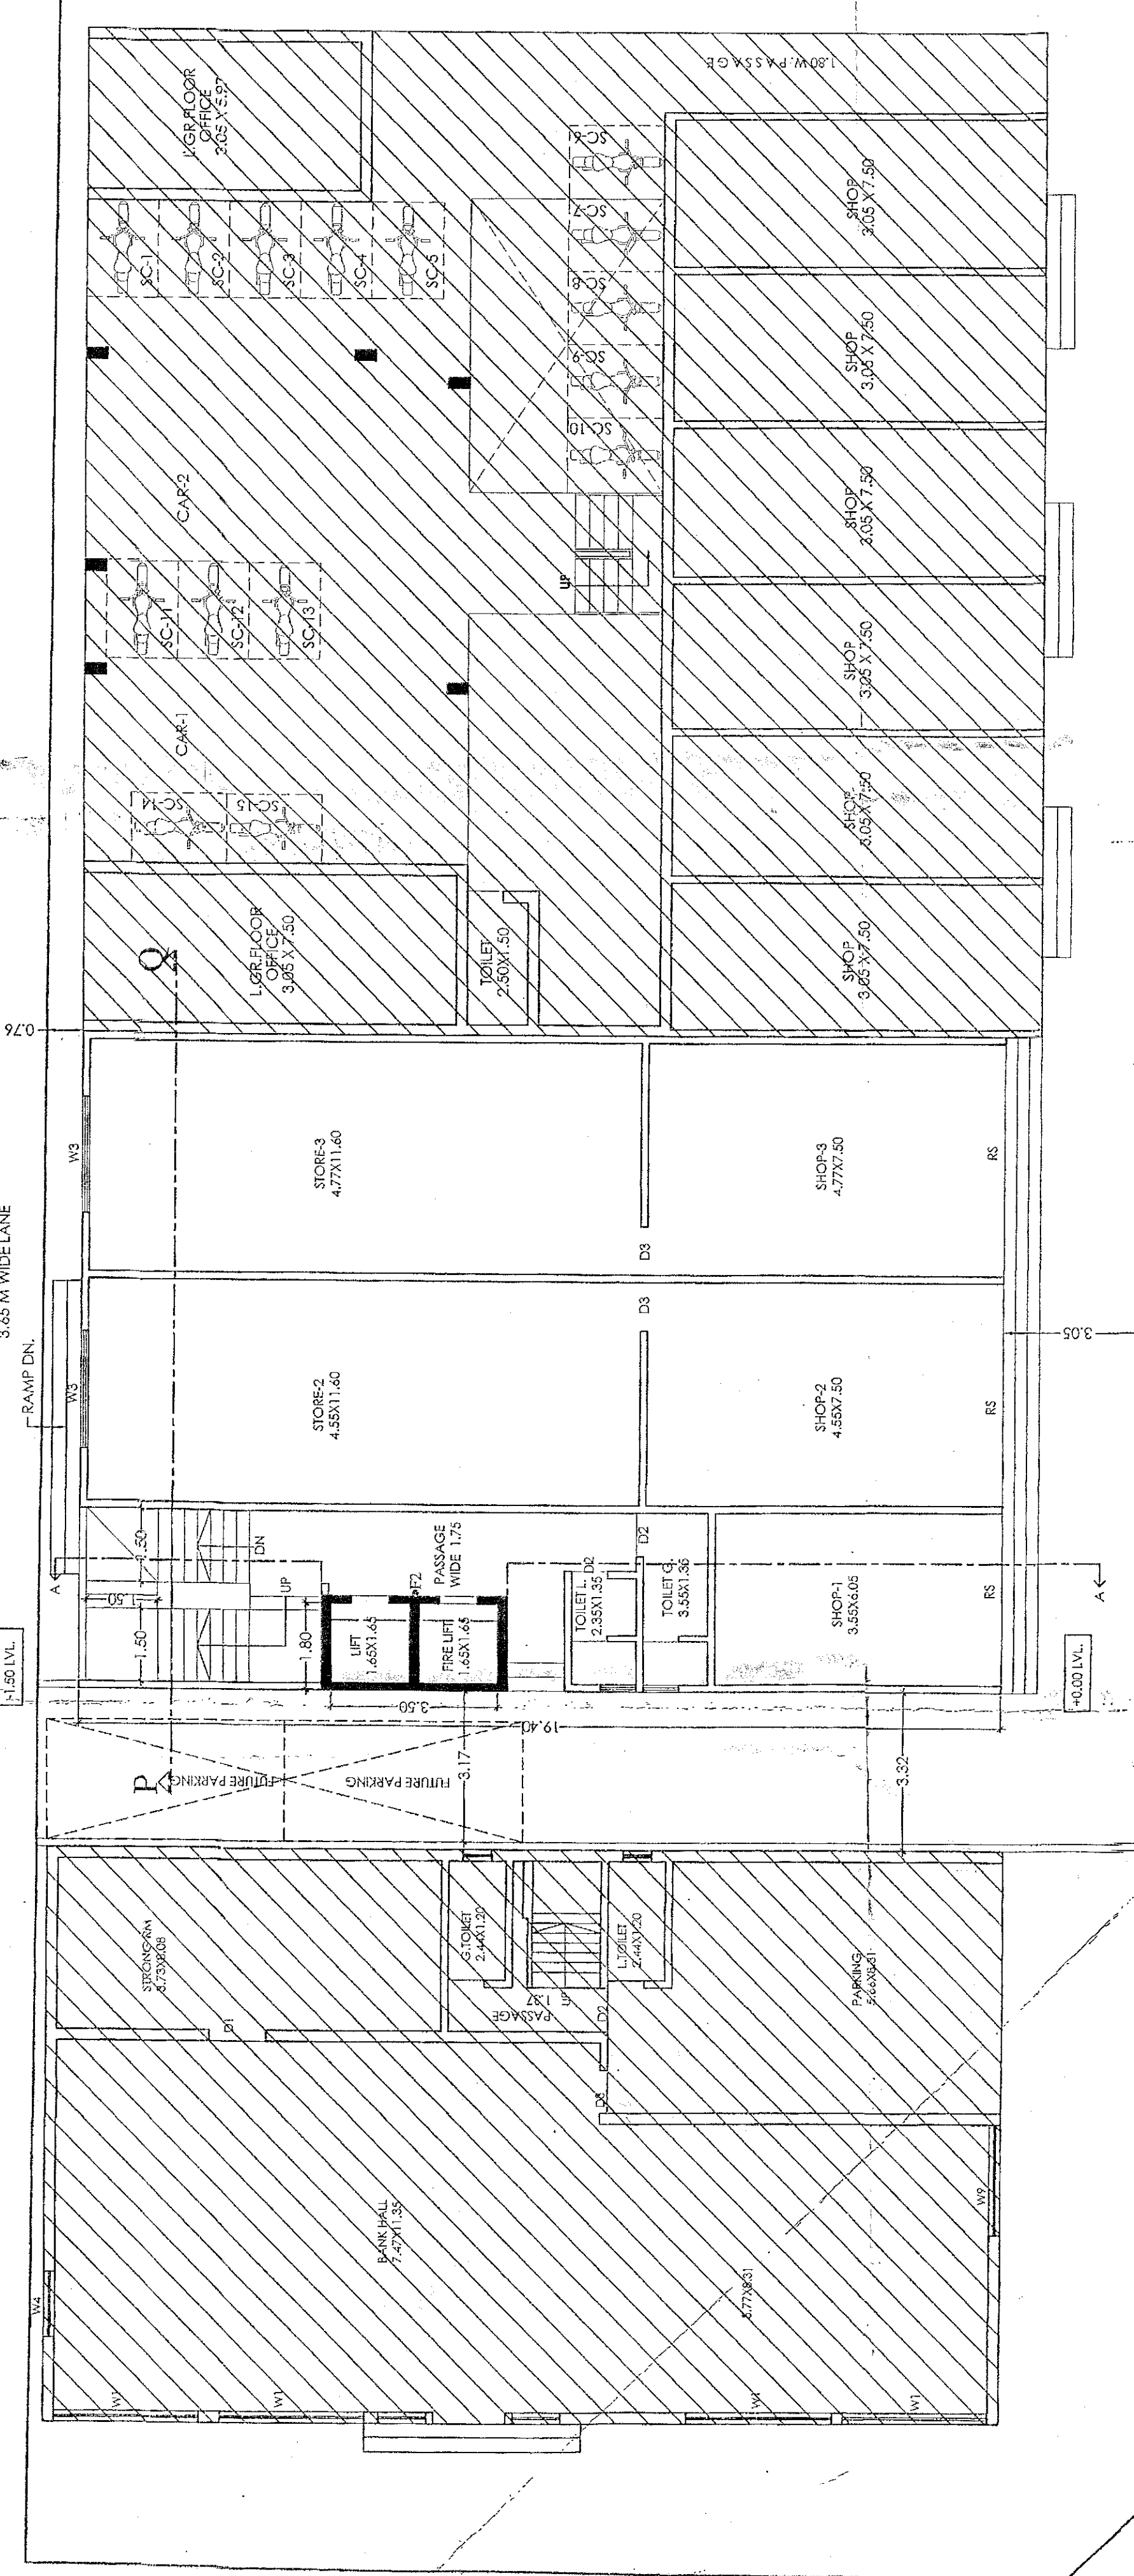


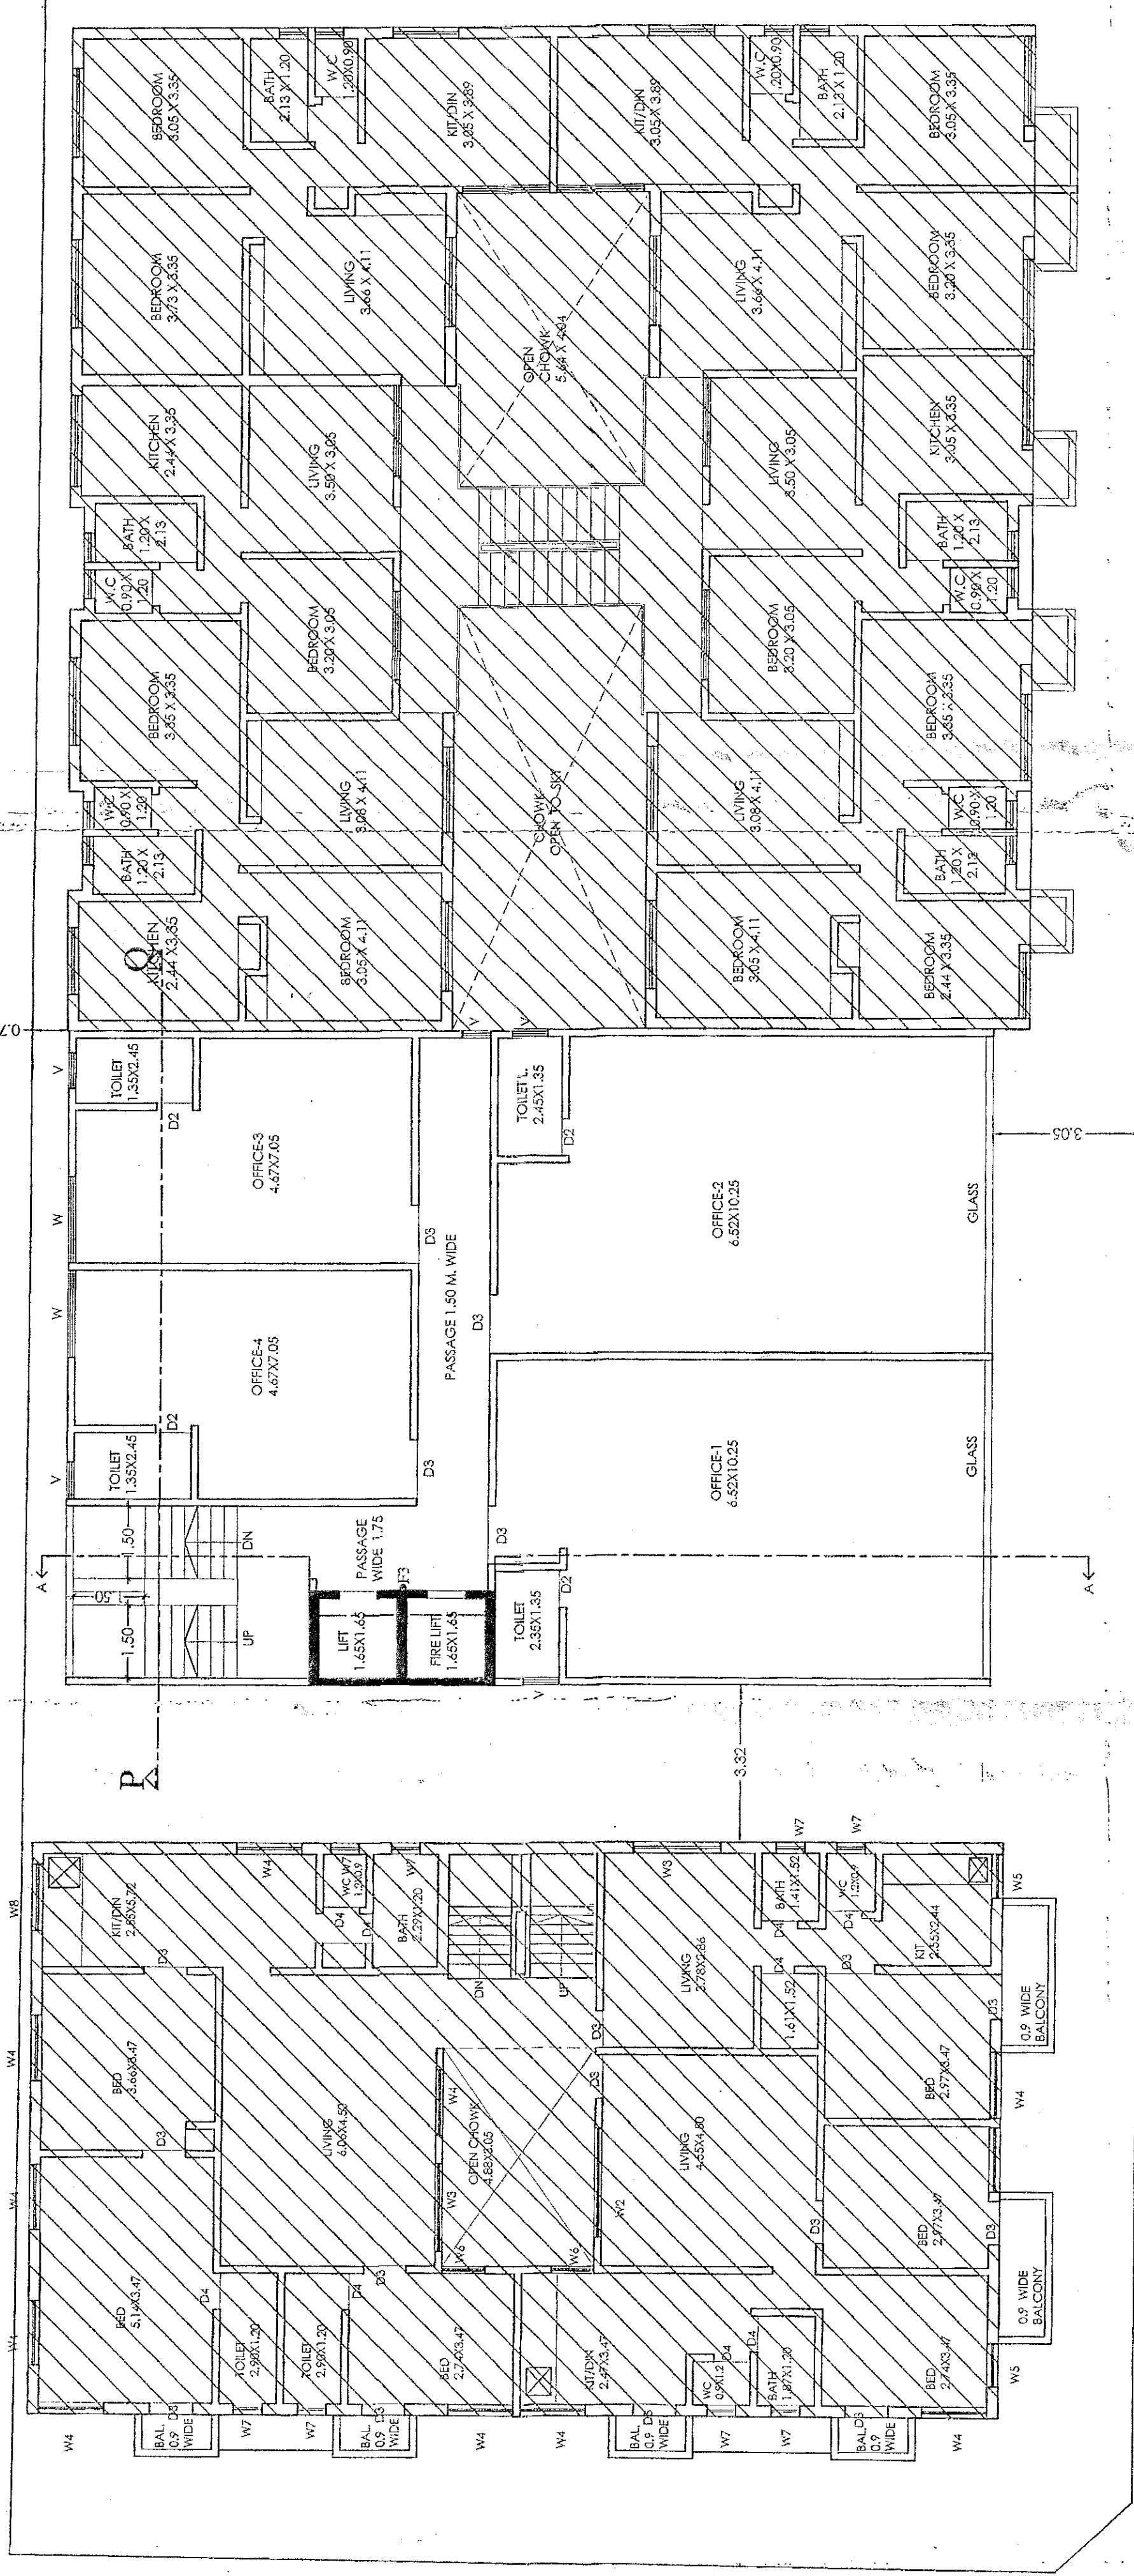

GROUND & FIRST FLOOR			
NO	LENGTH	WIDTH	TOTAL
A	13.49	19.40	261.71

DEDUCTION			
NO	LENGTH	WIDTH	TOTAL
1	1.80	x	6.30
TOTAL			6.30

BUILTUP AREA GROUND & FIRST FLOOR			
NO	A	DEDUCTION	TOTAL
TOTAL	261.71	- 6.30	255.41


BUILT-UP AREA GROUND & FIRST FLOOR			
NO	A	DEDUCTION	TOTAL
TOTAL	261.71	6.30	255.41

TABLE NO. 8B, PARKING REQUIREMENTS

TYPE	REQUIREMENTS AS PER IS 456:2000		REQUIREMENTS AS PER IS 456:2000		CUMULATIVE CUMULATIVE	REQUIREMENTS AS PER IS 456:2000
	4 WTH	2 WTH	4 WTH	2 WTH		
1) MERCANAL FOR EVERY 10.00 SQ.M. CUMULATIVE AREA OR RATION THEREOF	01	06	68.00	40		
2) RESIDENTIAL FOR EVERY TWO THIRDS BERT WITH EIGHTEN BERT OR ABOVE IS EQUAL TO OR ABOVE IS EQUAL BUT LESS THAN IS EQUAL	01	04	08	05	12	
5% VARIATION						40
						110
						32
						66
						32

ANCILLARY AREAS			
FLOOR	TOTAL AREA	BASIC AREA	ANCILLARY AREA
GROUND	255.41	141.89	113.52
FIRST	255.41	141.89	113.52
SECOND	269.57	147.76	119.81
THIRD	210.17	162.61	97.56
FOURTH	156.02	97.51	58.51
	1198.48	699.72	564.54

BUILT UP	AREA(SQ.M.)
COMMERCIAL	780.39
RESIDENTIAL	415.89

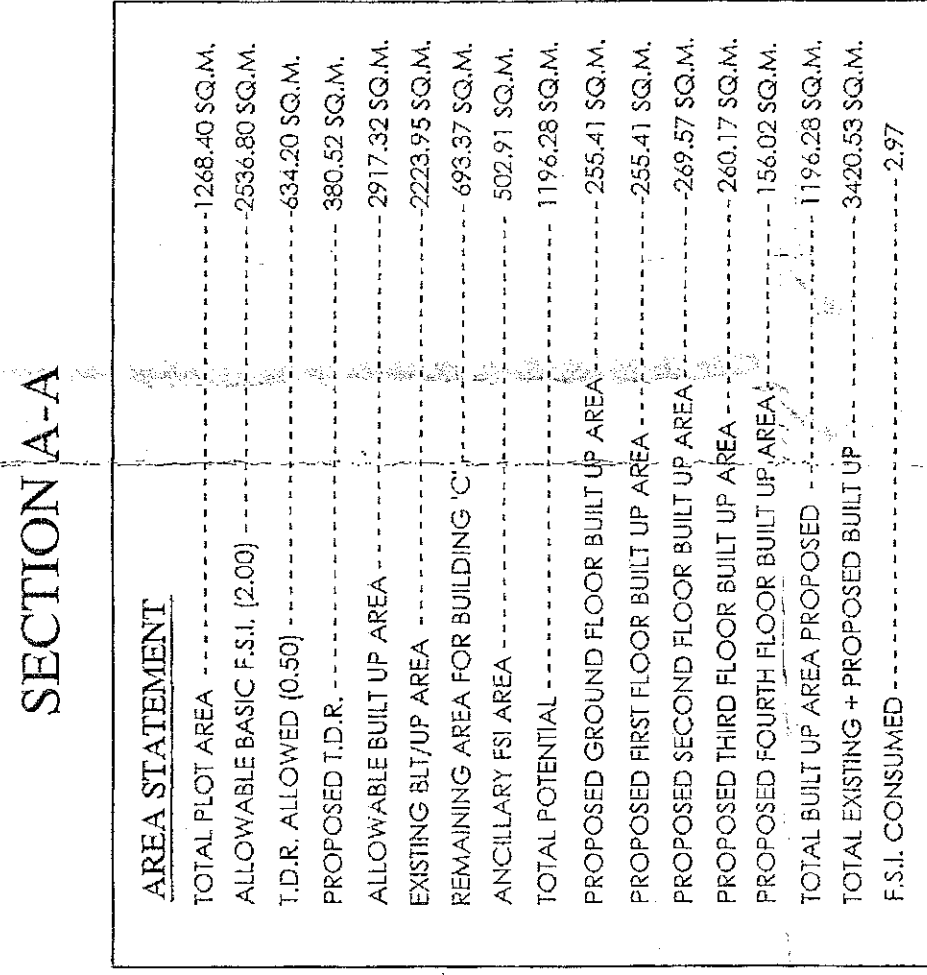

TYPE	DESCRIPTION	SIZE
T0	T.W. FRAMED POLYING GLAZED DOOR	1.6X7.210
T1	T.W. FRAMED POLYING GLAZED DOOR	1.8X7.210
D1	T.W. FRAMED CUBIN DOOR	0.9X0.210
D2	T.W. FRAMED HURDOOR	0.5X2.020
D3	T.W. FRAMED PANSELED DOOR	1.2X2.020
R3	ROLLING SHUTTER	4.5X5.7 HEIGHT R.A.S.H.
G	STRUCTURAL GLAZING	N/A
W	ALUMINIUM FRAMED GLAZED WINDOW	1.8X1.150
W1	ALUMINIUM FRAMED GLAZED WINDOW	1.5X1.150
W2	ALUMINIUM FRAMED GLAZED WINDOW	1.5X1.150
W3	ALUMINIUM FRAMED GLAZED WINDOW	2.6X1.000
V3	ALUMINIUM FRAMED GLAZED VENT	2.6X1.000

		AREA STATEMENT	TOTAL
01	a	AREA OF PLOT	324.0
	b	AS PER OWNERSHIP DOCUMENT (7172, CTS EXTRACT)	1266.0
	c	AFTER ACQUISITION SHEET	1266.0
	d	AS PER SITE	1266.0
02	e	DEDUCTIONS FOR	NIL
	f	PROPOSED D.P./ D.F. ROAD WIDENING AREA	NIL
03	g	ANT D.P. RESERVATION AREA	NIL
	h	TOTAL (A-H)	1266.0
04	i	BALANCE AREA OF PLOT (J2)	N/A
	j	ARMING SPACE (IF APPLICABLE)	N/A
05	k	REQUIRED	
06	l	ADJUSTMENT OF 25% IF ANY	
	m	BALANCE PROPOSED	1266.0
07	n	NET PLOT (3-4c)	
	o	RECREATIONAL OPEN SPACE (IF APPLICABLE)	
08	p	INTERNAL ROAD AREA	
	q	POTABLE AREA (IF APPLICABLE)	
09	r	WIDE PAV. AREA WITH REFERENCE TO BASIC F.S.L. AS PER FRONT WIDTH (5.0 X 2.0)	2550.0
10	s	ADDITIONAL F.S.L. ON PAYMENT. REMAIN	N/A
	t	MAX. POSSIBLE PRODUCE F.S.L. BASED ON ROAD WIDENING ZONE	N/A
11	u	PROPOSED F.S.L. ON PAYMENT OF PREMIUM	360.0
	v	IN 50' H/TY TDS LOADING	NIL
12	w	NET AREA, ADJUSTED TO ROAD (EUBOR (2.0 X 3.0)) IF ANY	NIL
	x	ADJUSTED TO ROAD (EUBOR (2.0 X 3.0)) IF HAND OVER	NIL
13	y	ADJUSTED TO ROAD (EUBOR (2.0 X 3.0)) IF HAND OVER	NIL
	z	TDS AREA	NIL
14	aa	TOTAL SITE IN TDS LOADING PROPOSED (1.1 HIGH-ROAD)	NIL
15	ab	ADDITIONAL F.S.L. IN THE PROPOSAL (BASIC SITE)	291.22
	ac	IN 50' H/TY TDS LOADING PROPOSED (1.1 HIGH-ROAD)	686.37
16	ad	TOTAL ENTIREMENT (A-H)	3402.23
17	ae	MAXIMUM UTILIZATION UNIT OF F.S.L. (BUILDING POTENTIAL)	3402.23
	af	MAXIMUM UTILIZATION UNIT OF F.S.L. (BUILDING POTENTIAL) PER 100' H/TY TDS LOADING PROPOSED (1.1 HIGH-ROAD)	3402.23
18	ag	TOTAL BUILD UP AREA IN PROPOSAL = BASIC TDS + ANGLARY	2222.35
19	ah	EXISTING BUILD UP AREA	1196.26
20	ai	F.S.L. CONSUMED (18/31)	3402.23
21	aj	AREA OF INCLUSIVE HOUSING, IF ANY	
22	ak	REQUIRED	
23	al	PROPOSED	

CERTIFICATE OF AREA

CERTIFIED THAT THE AREA UNDER REFERENCE WAS SURVEYED BY ME ON 27.02.2020 AND
DIMENSION OF THE PLD SITES ON THE PUNJABIA MANOUEHS ON THE SITE AREA AND
FOUNDER OF THE PLD SITES WERE MEASURED AND THE RESULTS WERE RECORDED IN THE
ORIGINAL P.D. SCHEDULE RECORDS. (LAND RECORD DEPARTMENT) PUNJABIA, ALAKA

RECD NO. 100/2020
CHANDIGARH
10/03/2020

MANOUEHS, ALAKA

PROPOSED COMM./RESI. COMPLEX ON C.S.NO.
1783/1 TO 3, 'E' WARD, RAJARAMPURI SECOND LANE,
KOLHAPUR FOR-
SHRI. DEEPAK BALASAHEB WAGHULE AND
SRI. POOTA DEEPAK WAGHULE F.

DRG.NO.	JOB NO.	DATE	SCALE	DRN.BY	CHD.BY
	1	21.06/2003	1:100		

SANJAY A. ADAKE.
ARCHITECTS AND INTERIOR DESIGNERS
'SRUSHITI MAHAABHARTI', C.S.NO.250B/22, 'E' WARD,
NAGALA PARK, KOLHAPUR.
REGD. No. CA - 90/13100
PHONE No. 2658648
E-MAIL = sanjay900@gmail.com

SHRI. DEEPAK BALASAHEB WAGHULE SQU. POOJA DEEPAK WAGHULE
SIGN OF OWNERS