


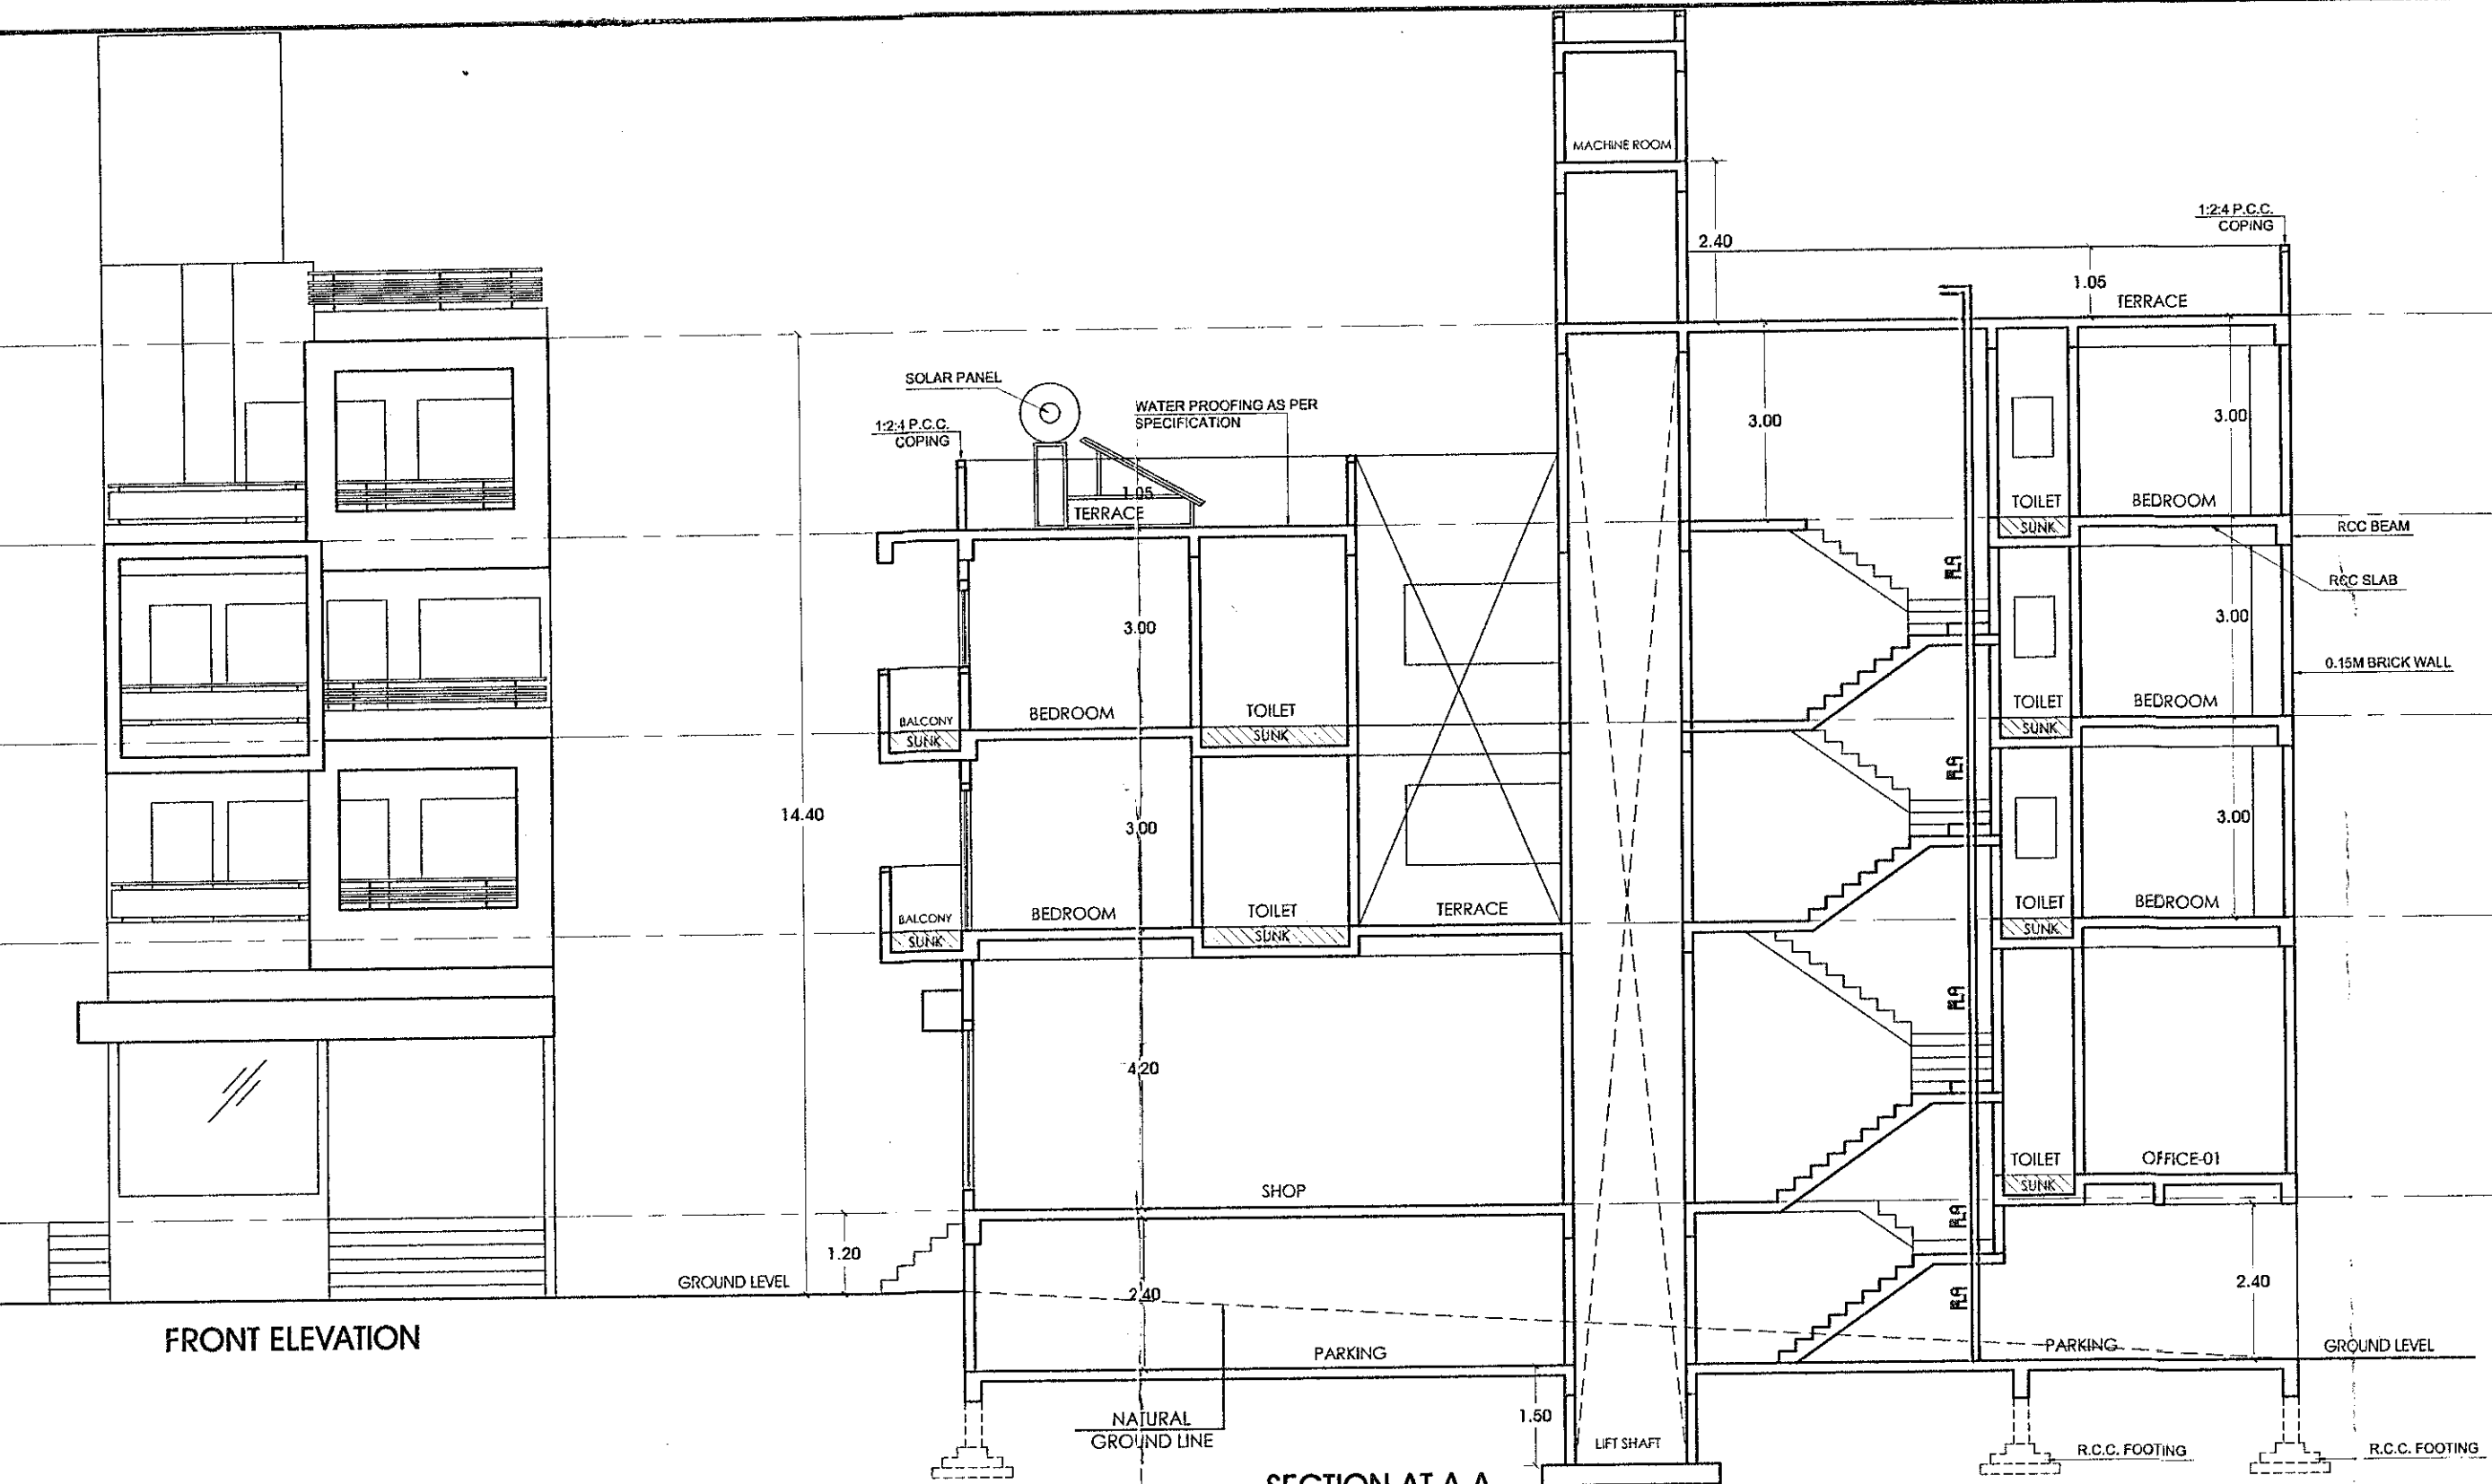


FRONT ELEVATION


SECTION AT A-A

PARKING STATEMENT - TABLE NO. 8B


Sr. No.	OCCUPANCY	REQUIREMENT OF PARKING FOR EVERY	NON CONGESTED AREA CAR NOS. SCOOTER NOS.	CARPET AREA	PARKING REQUIRED CAR NOS. SCOOTER NOS.	PARKING PROVIDED CAR NOS. SCOOTER NOS.
1	COMMERCIAL	FOR EVERY 100 SQM. CARPET AREA OR FRACTION THEREOF.	2 6	111.50 SQM.	2 6	2 6
2	RESIDENTIAL	FOR EVERY TWO TENEMENTS WITH EACH TENEMENT HAVING CARPET AREA EQUAL TO OR ABOVE 40 SQM. BUT LESS THAN 80 SQM.	1 5	106.50 SQM. (2 TENEMENTS)	1 5	1 5
		FOR EVERY TWO TENEMENTS WITH EACH TENEMENT HAVING CARPET AREA LESS THAN 40 SQM. BUT MORE THAN 30 SQM.	1 2	108.50 SQM. (3 TENEMENTS)	1 3	1 3
TOTAL					4 14	4 14
TABLE NO. 8C - 'D' CLASS MUNICIPAL CORPORATION AREA (MULTIPLYING FACTOR - 0.60) - A					2 9	2 9
5% VISITORS - B					1 1	1 1
TOTAL PARKING (A+B)					2 10	2 10

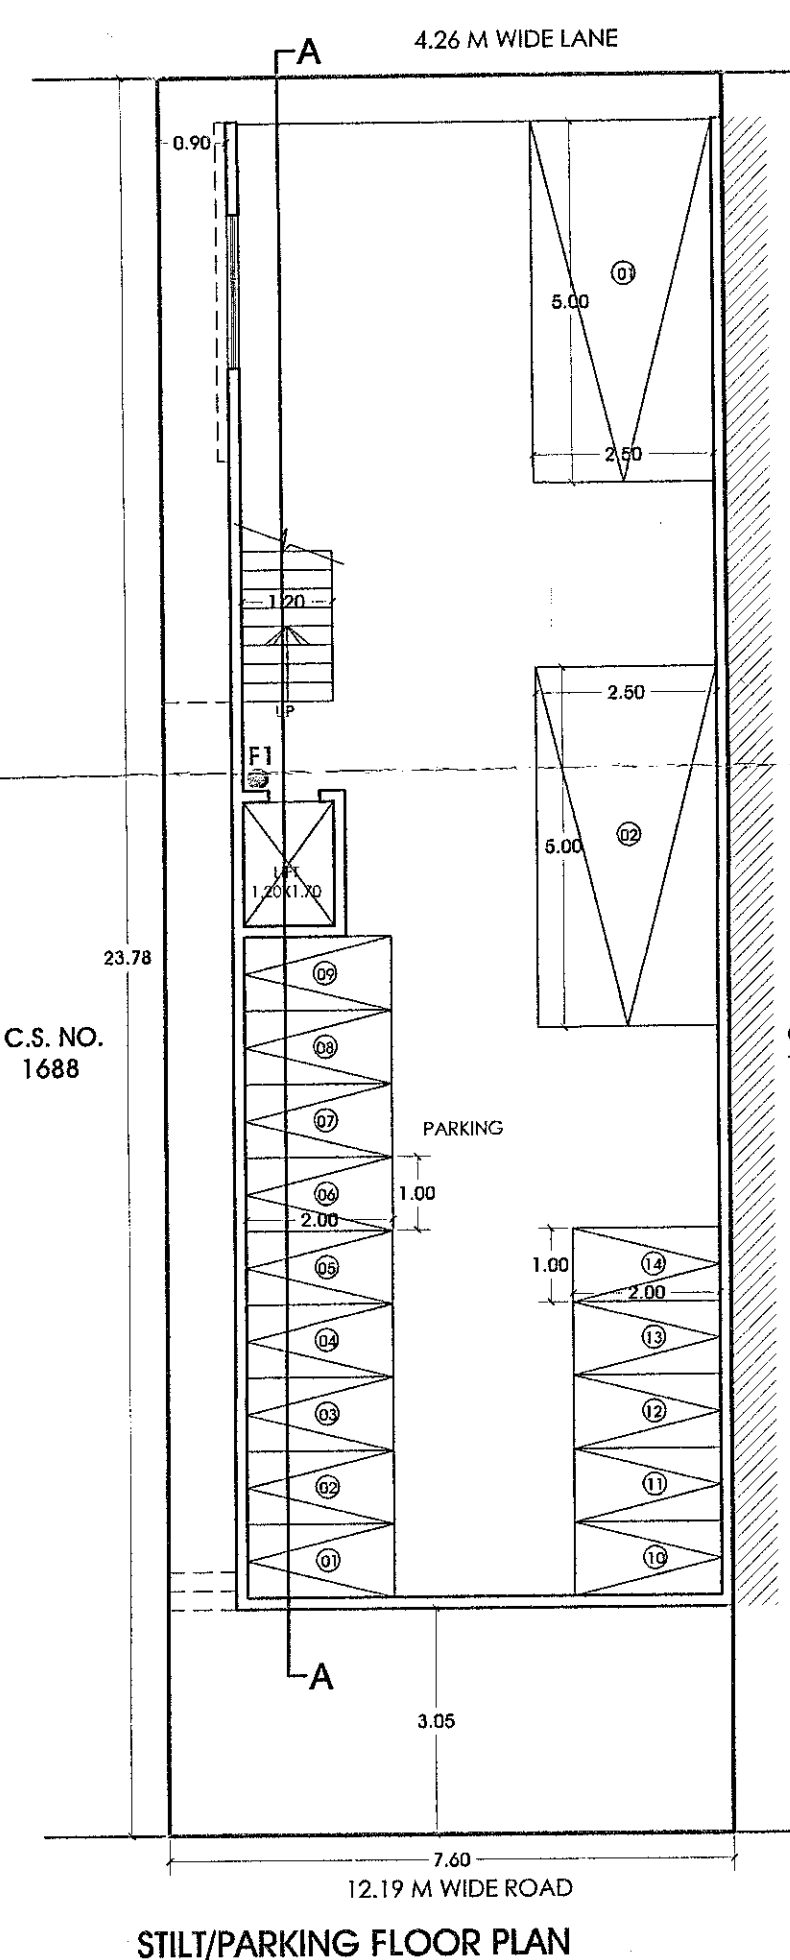


STILT/PARKING FLOOR PLAN

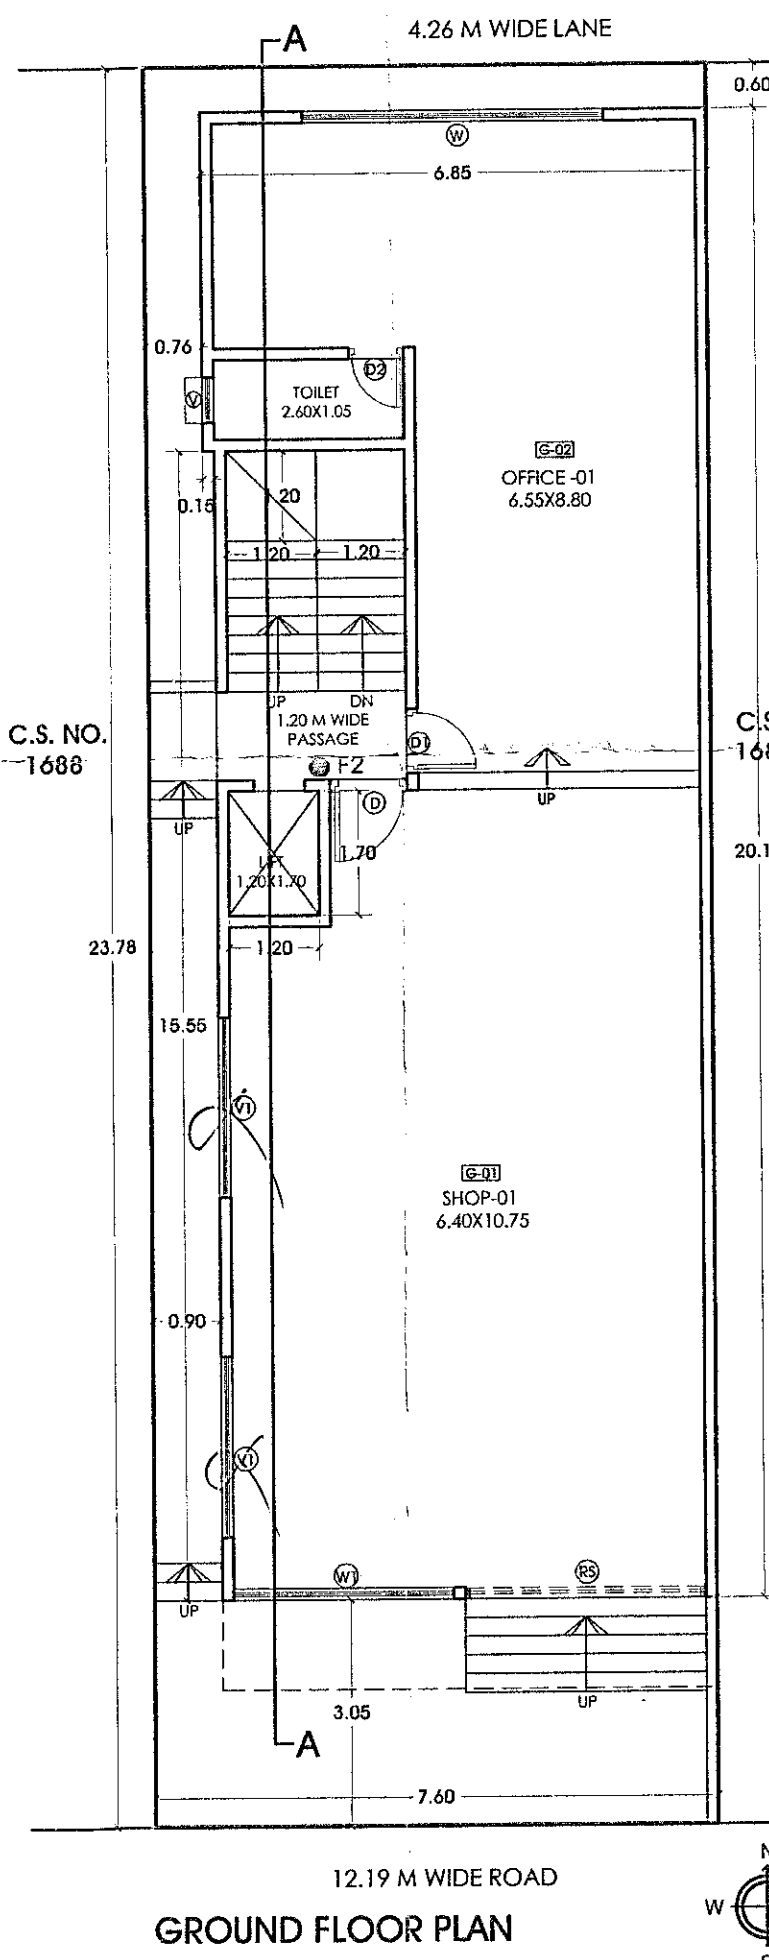


GROUND FLOOR PLAN

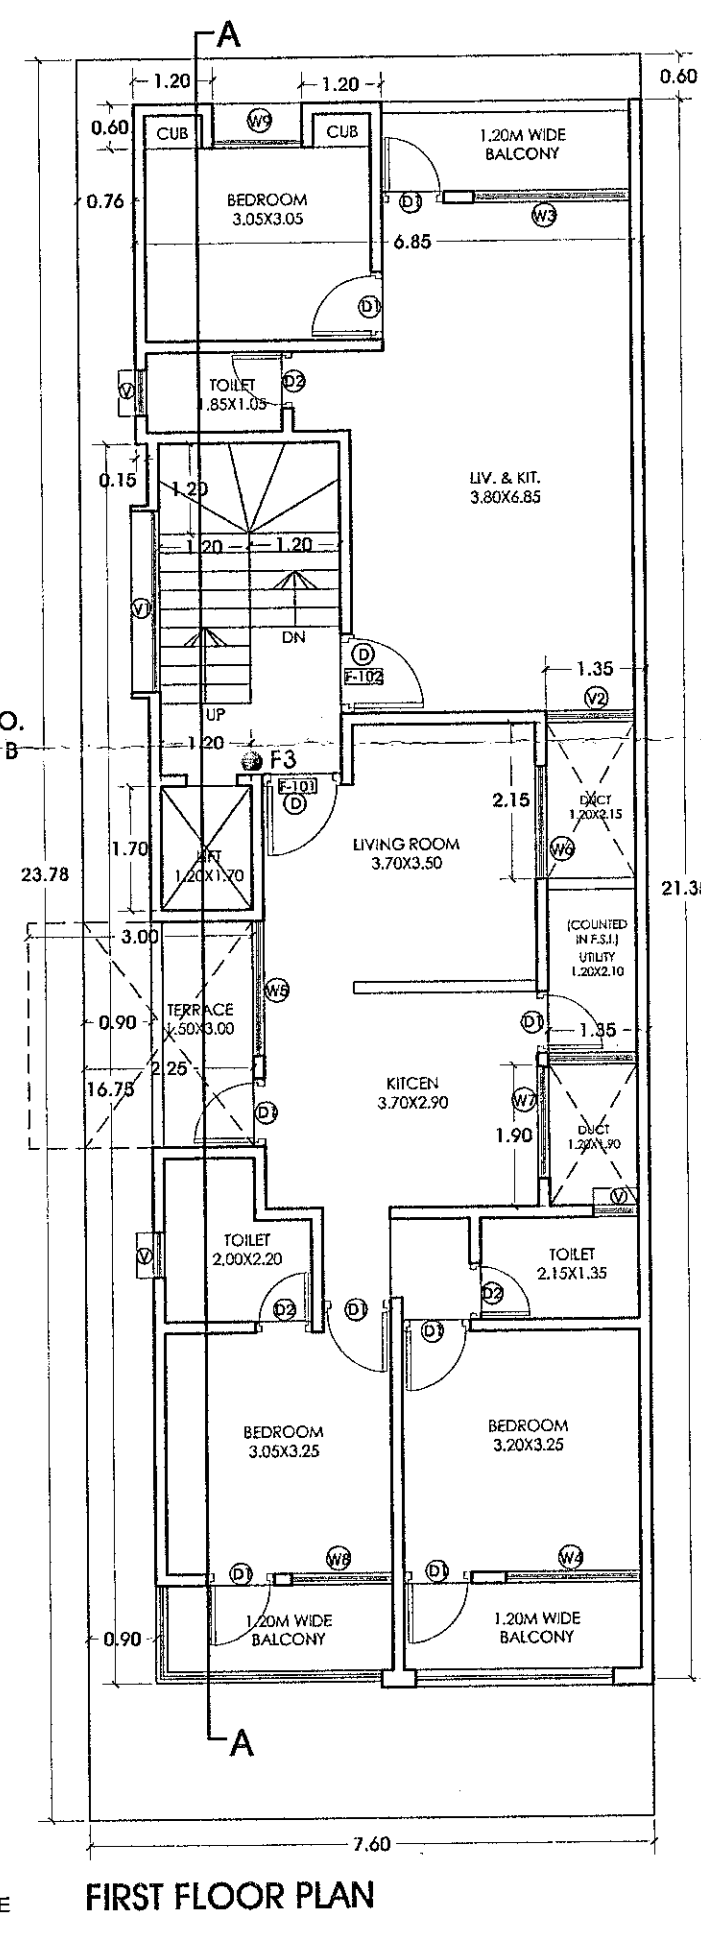

FIRST FLOOR PLAN

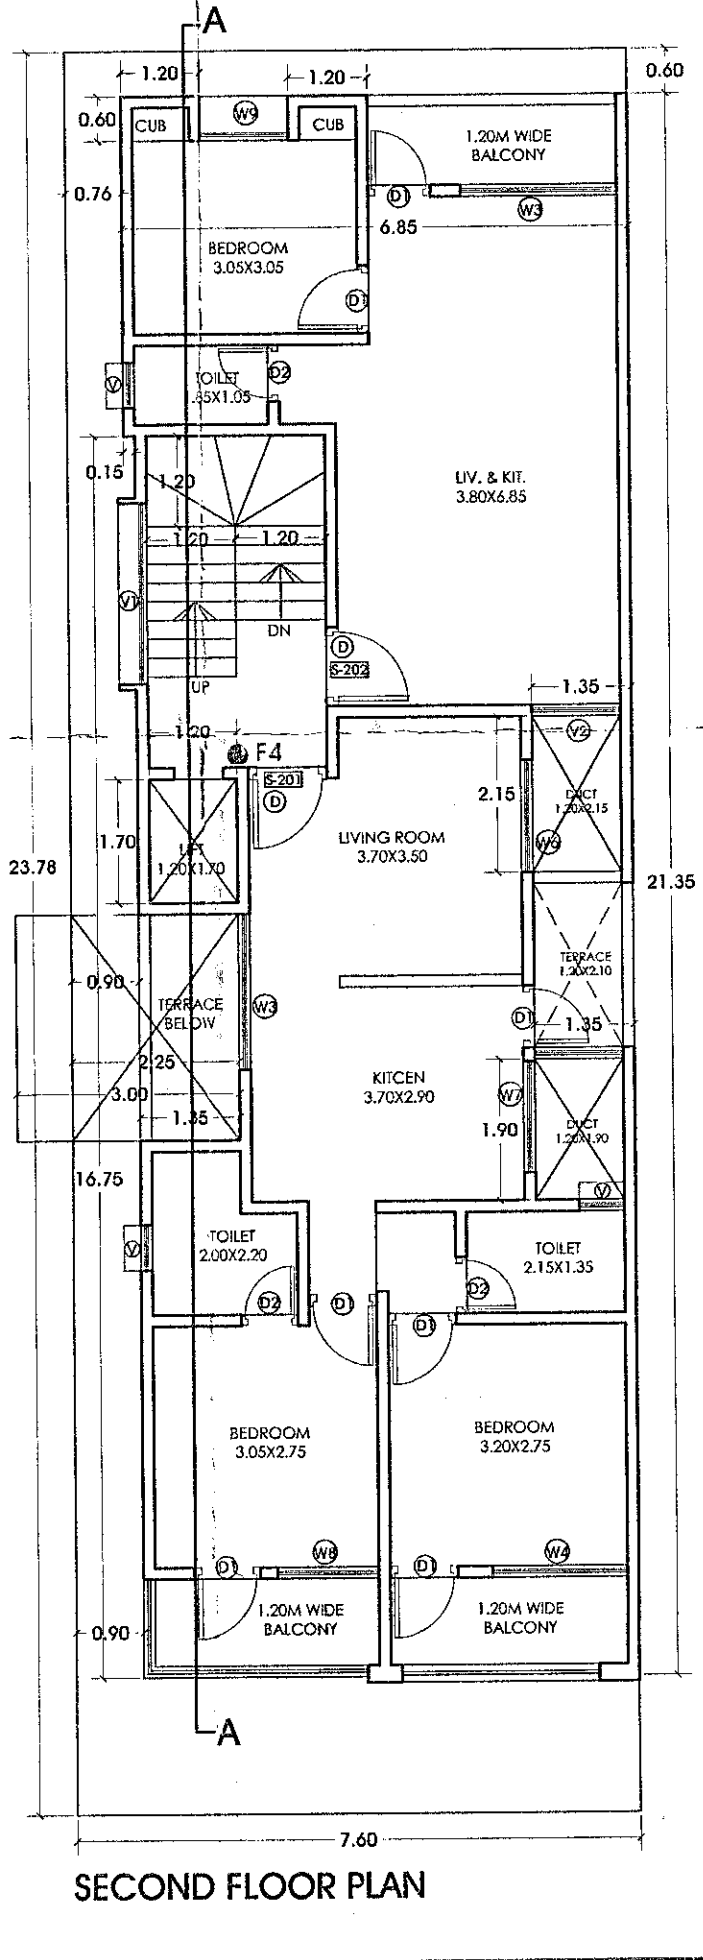


SECOND FLOOR PLAN

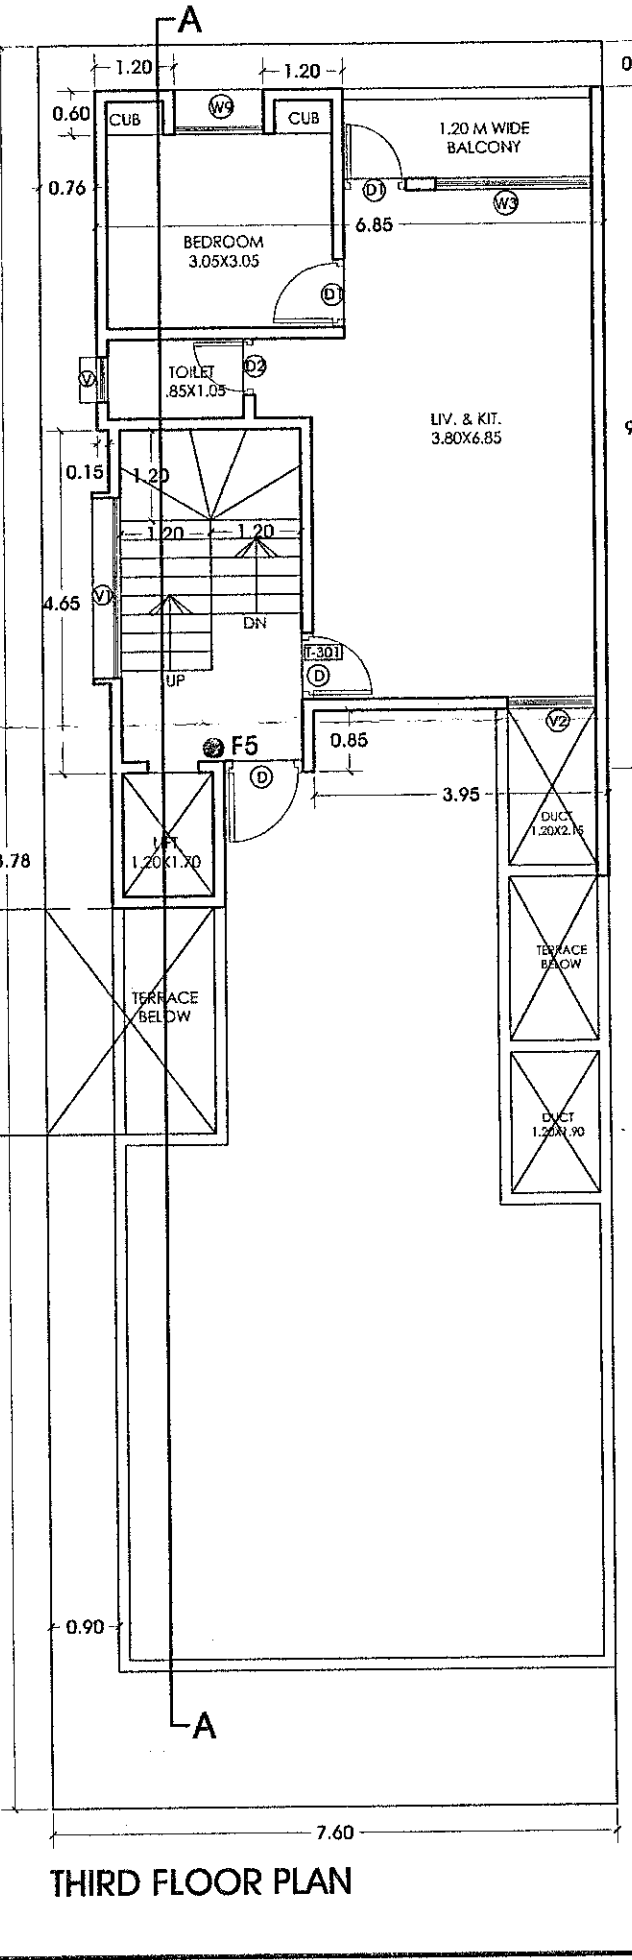

THIRD FLOOR PLAN

AREA STATEMENT

TOTAL PLOT AREA = 174.40 SQM.
F.S.I. PERMISSIBLE = 2.00
BUILT UP AREA PERMISSIBLE = 348.80 SQM. (01)
ANCILLARY F.S.I. 60% ALLOWED = 209.28 SQM. (02)
TOTAL BUILT UP AREA PERMISSIBLE (01+02) = 558.08 SQM.
GROUND FLOOR AREA = 133.31 SQM.
FIRST FLOOR AREA = 136.23 SQM.
SECOND FLOOR AREA = 132.11 SQM.
THIRD FLOOR AREA = 58.96 SQM.
TOTAL BUILT UP AREA = 460.61 SQM.
F.S.I. CONSUMED = 2.64
ANCILLARY F.S.I. TAKEN = 111.81 SQM.

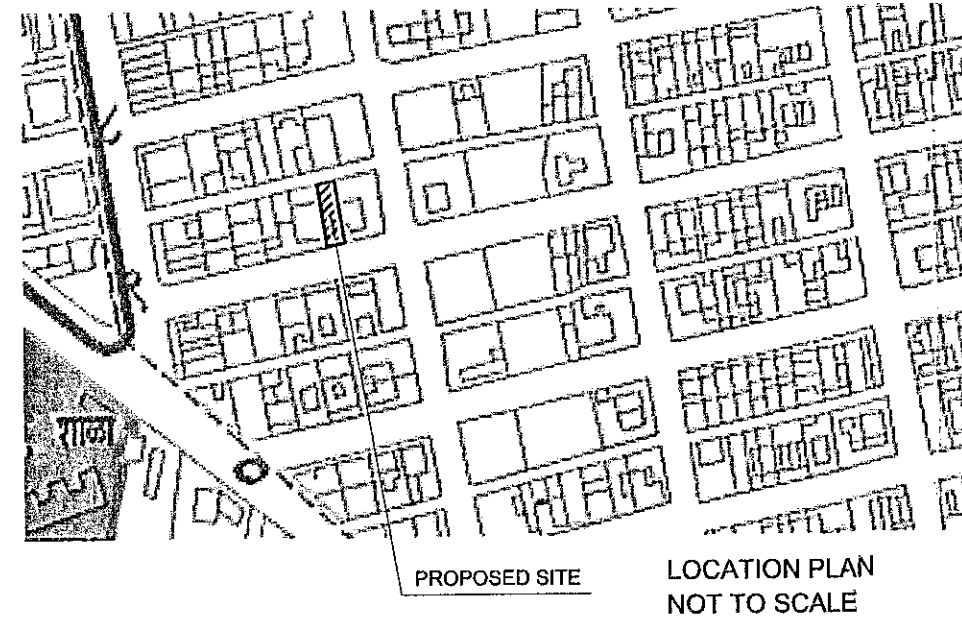

LOCATION PLAN NOT TO SCALE

AREA STATEMENT FOR GROUND FLOOR PLAN (COMMERCIAL)
TOTAL AREA = 6.85 X 20.10 = 137.68 SQM
DEDUCTION BLOCK - (L(M) X B(M)) = AREA (SQM)
a - 1.20 X 1.70 = 2.04
b - 0.15 X 15.55 = 2.33
TOTAL = 4.37 sqm.
TOTAL GROUND FLOOR AREA = 137.68 - 4.37 = 133.31 SQM.
GROUND FLOOR SCALE 1:200


AREA STATEMENT FOR FIRST FLOOR PLAN (RESIDENTIAL)
TOTAL AREA = 6.85 X 21.35 = 146.25 SQM
DEDUCTION BLOCK - (L(M) X B(M)) = AREA (SQM)
a - 0.15 X 16.75 = 2.51
b - 1.20 X 1.70 = 2.04
c - 1.35 X 2.15 = 2.90
d - 1.35 X 1.90 = 2.57
TOTAL = 10.02 sqm.
TOTAL FIRST FLOOR AREA = 146.25 - 10.02 = 136.23 SQM.
FIRST FLOOR SCALE 1:200

AREA STATEMENT FOR SECOND FLOOR PLAN (RESIDENTIAL)
TOTAL AREA = 6.85 X 21.35 = 146.25 SQM
DEDUCTION BLOCK - (L(M) X B(M)) = AREA (SQM)
a - 0.15 X 16.75 = 2.51
b - 1.20 X 1.70 = 2.04
c - 1.35 X 2.15 = 2.90
d - 1.35 X 1.90 = 2.57
TOTAL = 10.02 sqm.
TOTAL SECOND FLOOR AREA = 146.25 - 10.02 = 136.23 SQM.
SECOND FLOOR SCALE 1:200

AREA STATEMENT FOR THIRD FLOOR PLAN (RESIDENTIAL)
TOTAL AREA = 6.85 X 9.20 = 63.02 SQM
DEDUCTION BLOCK - (L(M) X B(M)) = AREA (SQM)
a - 0.15 X 4.65 = 0.70
b - 3.95 X 0.85 = 3.36
TOTAL = 4.06 sqm.
TOTAL THIRD FLOOR AREA = 63.02 - 4.06 = 58.96 SQM.
THIRD FLOOR SCALE 1:200


SCHEDULE OF DOORS & WINDOWS

TYPE	DESCRIPTION	SIZE
S1	ROLLING SHUTTER	3.20MX2.40M
D	TEAK WOOD FRAME PANEELED DOOR	1.05MX2.10M
D1	TEAK WOOD FRAME PANEELED DOOR	0.90MX2.10M
D2	TEAK WOOD FRAME PANEELED DOOR	0.75MX2.10M
W	ALUMINIUM GLAZED FRAME GLAZED WINDOW	4.10MX1.20M
W1	ALUMINIUM GLAZED FRAME GLAZED WINDOW	3.00MX1.20M
W2	ALUMINIUM GLAZED FRAME GLAZED WINDOW	2.40MX1.20M
W3	ALUMINIUM GLAZED FRAME GLAZED WINDOW	2.10MX1.05M
W4	ALUMINIUM GLAZED FRAME GLAZED WINDOW	1.80MX1.20M
W5	ALUMINIUM GLAZED FRAME GLAZED WINDOW	1.80MX1.05M
W6	ALUMINIUM GLAZED FRAME GLAZED WINDOW	1.50MX1.20M
W7	ALUMINIUM GLAZED FRAME GLAZED WINDOW	1.50MX1.05M
W8	ALUMINIUM GLAZED FRAME GLAZED WINDOW	1.35MX1.20M
W9	ALUMINIUM GLAZED FRAME GLAZED WINDOW	1.20MX1.05M
V	ALUMINIUM FRAME LOUVERED WINDOW	0.40MX0.90M
V1	ALUMINIUM FRAME LOUVERED WINDOW	2.40MX0.90M
V2	ALUMINIUM FRAME LOUVERED WINDOW	1.05MX0.90M

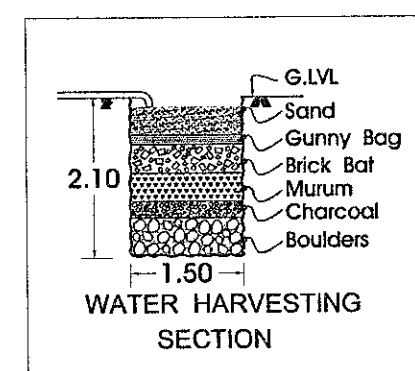

WATER HARVESTING SECTION

STAMP OF APPROVAL PLAN

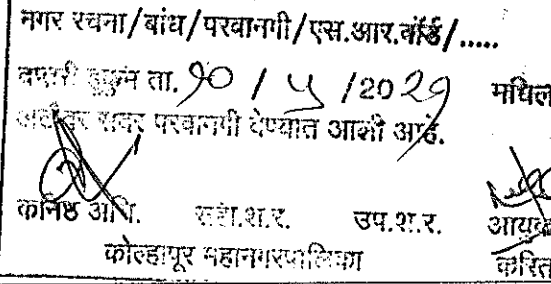

COPY RIGHT
REPRODUCED WITHOUT PRIOR WRITTEN PERMISSION FROM THIS FIRM. THIS DRAWING IS THE SOLE PROPERTY OF SWAPNIL & CAN NOT BE COPIED, ALTERED.

PROFORMA I

A	AREA STATEMENT	TOTAL
1	AREA OF PLOT (Minimum area of a,b,c to be considered)	174.40
a)	As per ownership document (7/12, CTS extract)	174.40
b)	As per measurement sheet	-
c)	As per site	-
2	Deductions for	-
(a)	Proposed D.P. / D.P. Road widening area/Service Road/ Highway widening	-
(b)	Any D.P. Reservation area	-
Total - (a+b)		-
3	Balance Area of Plot (1-2)	174.40
4	Amenity Space (if applicable)	nil
(a)	Required -	nil
(b)	Adjustment of 2(b), if any -	nil
(c)	Balance Proposed -	nil
5	Net Plot Area (3-4 (c))	174.40
6	Recreational Open space (if applicable)	nil
(a)	Required -	nil
(b)	Proposed -	nil
7	Internal Road area	nil
(d)	Plotable area (if applicable)	174.40
(e)	For Basic F.S.I. = 1.00	2.00
9	Built up area with reference to Basic F.S.I. as per front road width (Sr. No. 5 basic FSI)	348.80
10	Addition of FSI on payment of premium	-
(a)	Maximum permissible premium FSI - based on road width / TOD Zone.	-
(b)	Proposed FSI on payment of premium.	-
11	In-situ FSI / TDR loading	-
(a)	In-situ area against D.P. Road [2.0 x Sr. No. 2 (a)] if any	-
(b)	In-situ area against Amenity Space if handed over [2.00 or 1.85 x Sr. No. 4 (b) and for (c)]	-
(c)	TDR area	-
(d)	Total in-situ / TDR loading proposed (11 (a)+(b)+(c))	-
12	Additional FSI area under Chapter No. 7	-
13	Total entitlement of FSI in the proposal	-
(a)	2 + 10(b) + 11(c) or 12 whichever is applicable.	348.80
(b)	Ancillary Area FSI upto 60% or 80% with payment of charges.	209.28
(c)	Total entitlement (a+b)	558.08
14	Maximum utilization limit of F.S.I. (building potential) Permissible as per Road width (as per Regulation No. 6.1 or 6.2 or 6.3 or 6.4 as applicable) x 1.6 or 1.8	3.20
15	Total Built-up Area in proposal (excluding area at Sr.No.17 b)	-
(a)	Existing Built-up Area.	-
(b)	Proposed Built-up Area (as per P-line)	460.61
(c)	Total (a+b)	460.61
16	F.S.I. Consumed (15/13) (should not be more than serial No.14 above.)	2.63
17	Area for Inclusive Housing, if any	-
(a)	Required (20% of Sr.No.5)	-
(b)	Proposed	-

PROFORMA II

CONTENTS OF SHEETS					
ALL FLOOR PLANS, SITE PLAN, SCHEDULE DOORS & WINDOWS, PERFORMANCE I & II.					
OWNER / P.A. HOLDER		CO-OWNERS		REVISION / DESCRIPTION	
SIGN		SIGN		SIGN	
DATE	JOB NO.	SCALE	DRG. NO.	DRAWN BY	CHECKED BY
19/12	1:100	19/12-AP-11-01	Sandeep	Swapnil	

NOTES:
ALL WRITTEN DIMENSIONS SHOULD BE FOLLOWED. ALL DIMENSIONS ARE IN METERS. CUP, BALCONY, OPEN SPACES TERRACES, STILT AREAS ARE NOT TAKEN IN F.S.I. CALCULATIONS. CALCULATIONS. ALL INTERNAL WALLS ARE 115/230 MM. THK. ANY DIMENSIONS & OTHER MUST BE REPORTED TO ARCHITECT.

CERTIFICATE OF AREA
CERTIFIED THAT THE PLOT UNDER REFERENCE WAS SURVEYED BY ME ON AND THE DIMENSION OF SIDES ETC. OF PLOT STATED ON PLAN ARE AS MEASURED ON SITE AND THE AREA SO WORKED OUT TALLIES WITH THE AREA STATED IN DOCUMENT OF OWNERSHIP/T.P. SCHEME RECORDS/LAND RECORDS DEPARTMENT/CITY SURVEY RECORDS.

SIGNATURE
(Name of Architect/ Licensed Engineer/ Supervisor.)

PROJECT :
PROPOSED COMMERCIAL CUM RESIDENTIAL BUILDING AT C.S. NO. 1689/1B, 'E' WARD, AT RAJARAMPURI 9TH LANE, AT KOLHAPUR, BELONGING TO MR. GAJANAN GOVINDRAO SOLANKURKAR.

OWNER'S SIGN

MR. GAJANAN G. SOLANKURKAR.

STAMP OF APPROVAL PLAN.

STAMP OF RECEIPT PLAN.
SPECIFICATION R.C.C. FRAMED STRUCTURE / LOAD BEARING, 230 MM/150MM/115MM THICK BRICK / CONCRETE BLOCK/WALLS DOOR WINDOW ALUM. S. STEELWOOD FLOORING MOSAIC, GLAZED, CERAMIC/TILE, MARBLE, SHAHABAD GRANITE.

ARCHITECTS SIGN

SWAPNIL ARCHITECTS

AR.SWAPNIL.SANKPAL

1690, 8TH LANE, RAJARAMPURI, 9TH WARD, KOLHAPUR.

B.Arch.A.I.A./CA/2004/33369. M-09850046263