



Advanced Construction Technologies & BIM

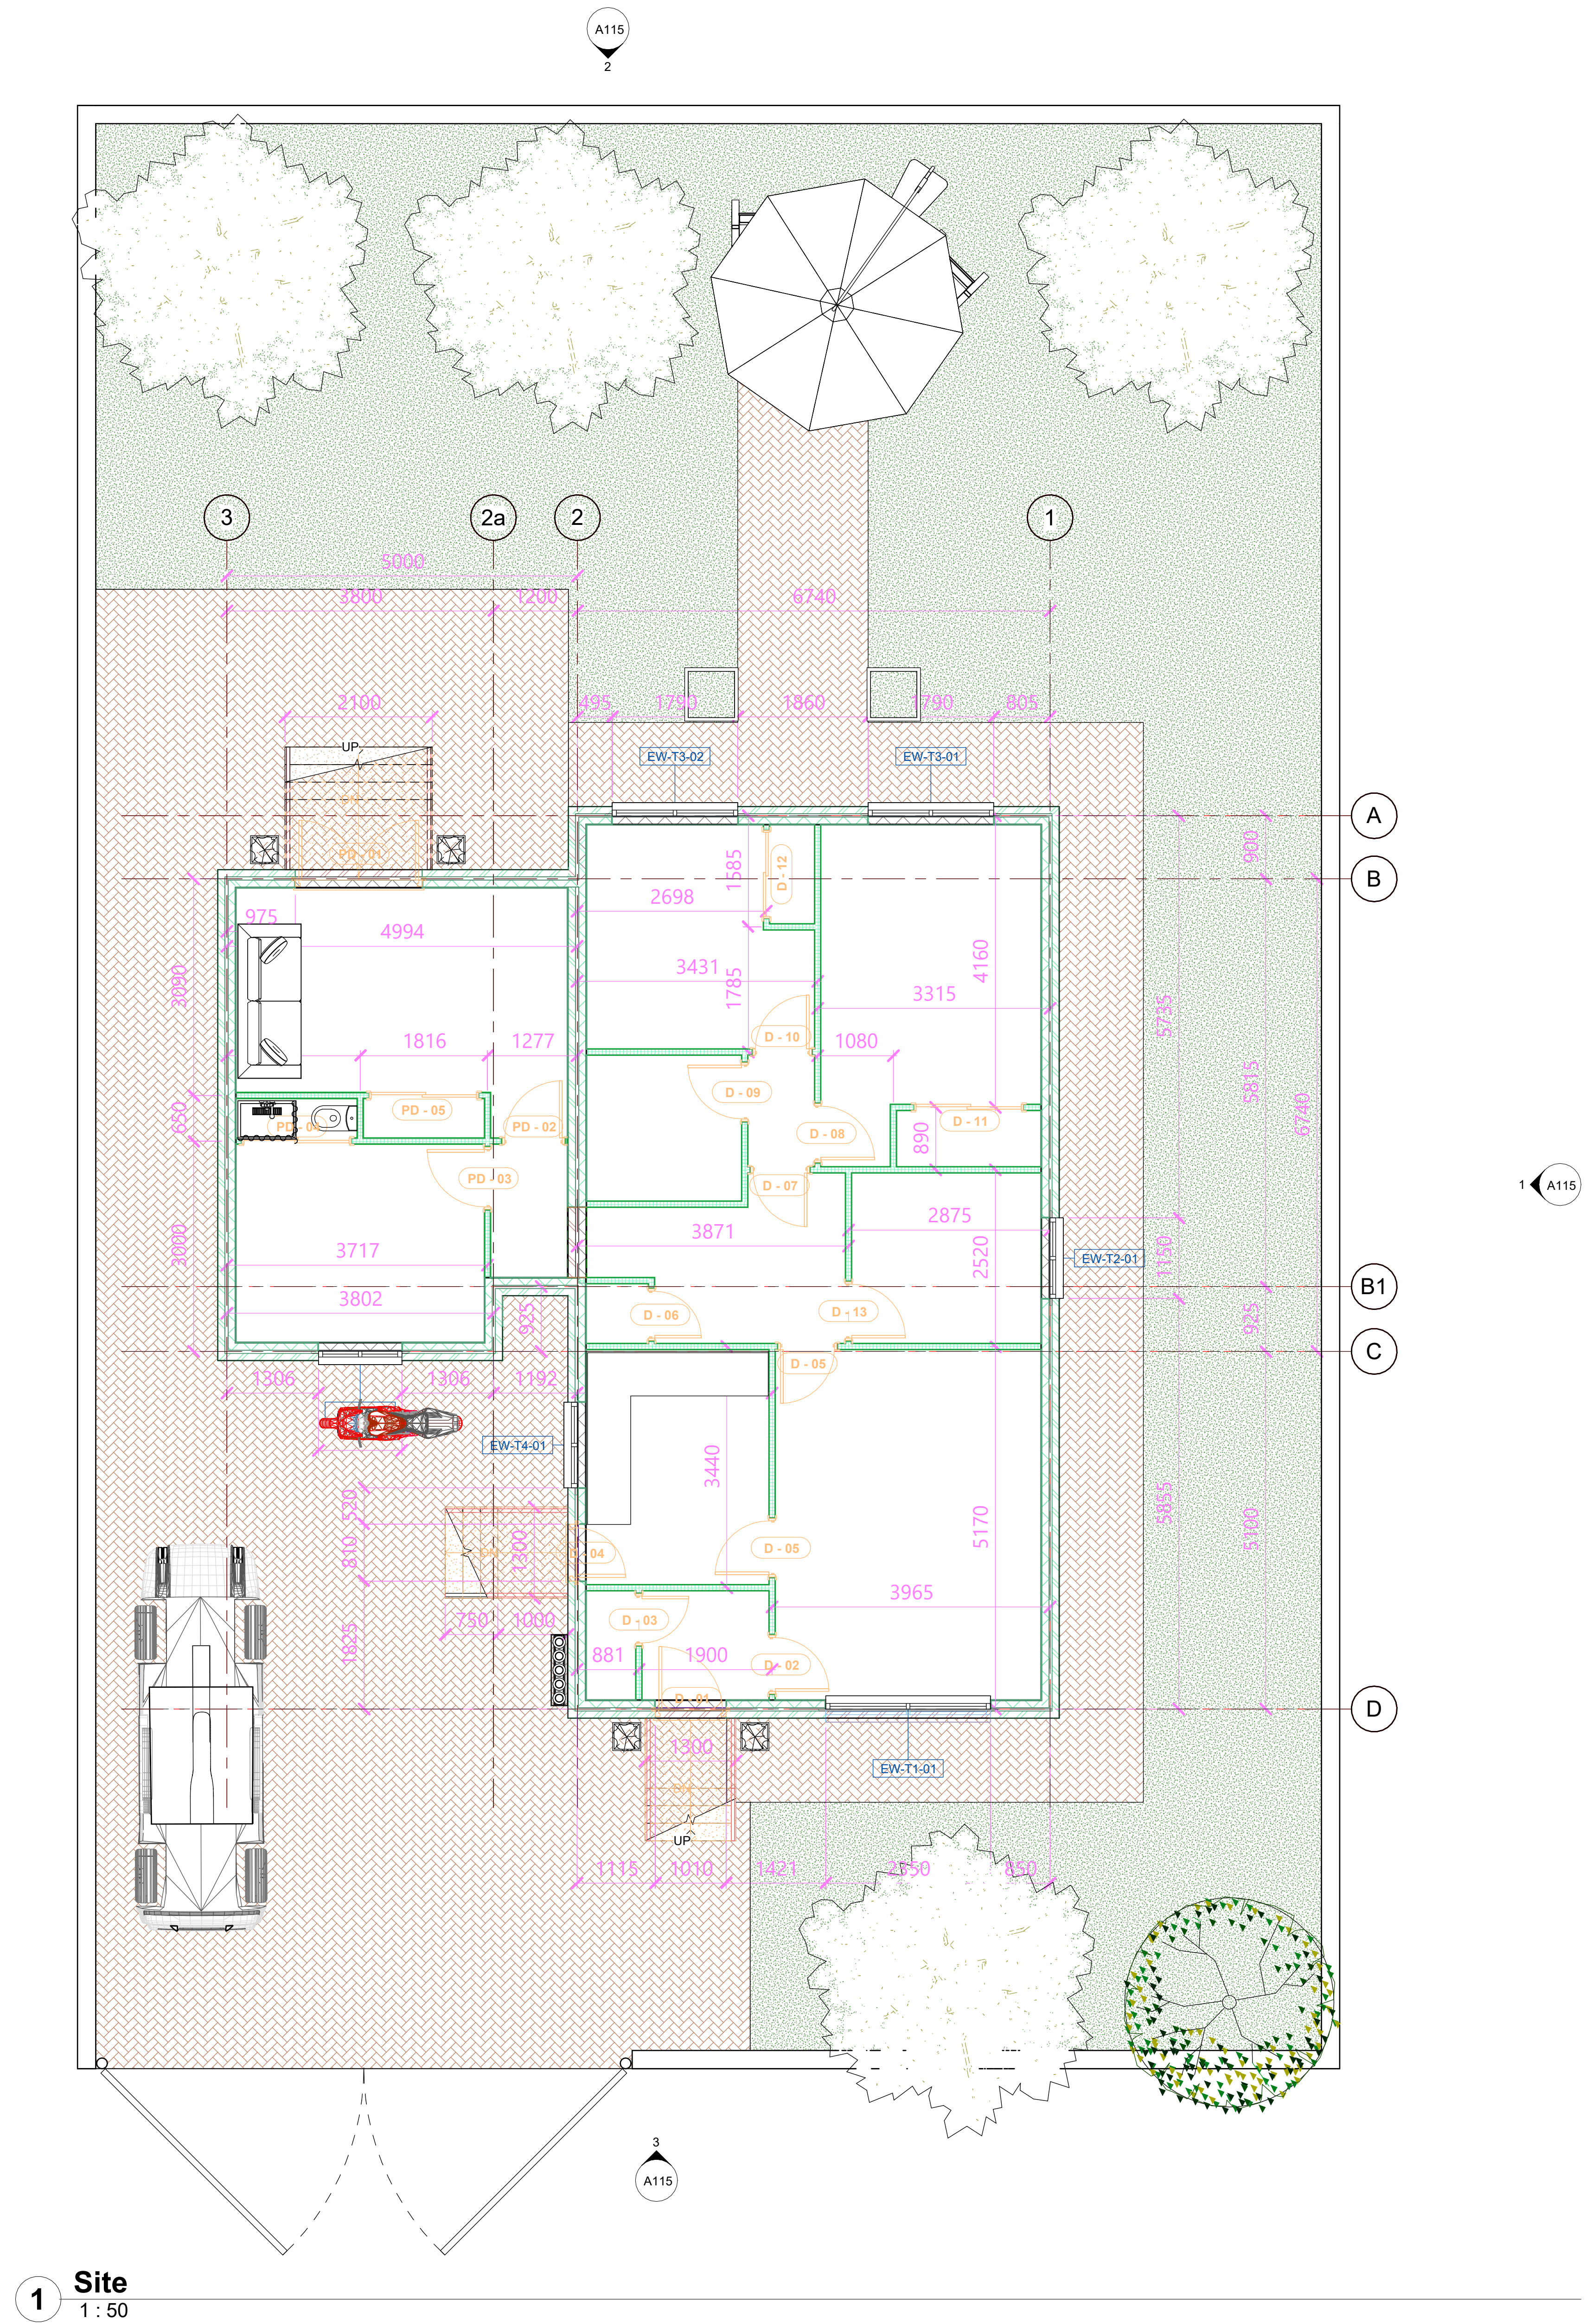
AB991 Building Information Management

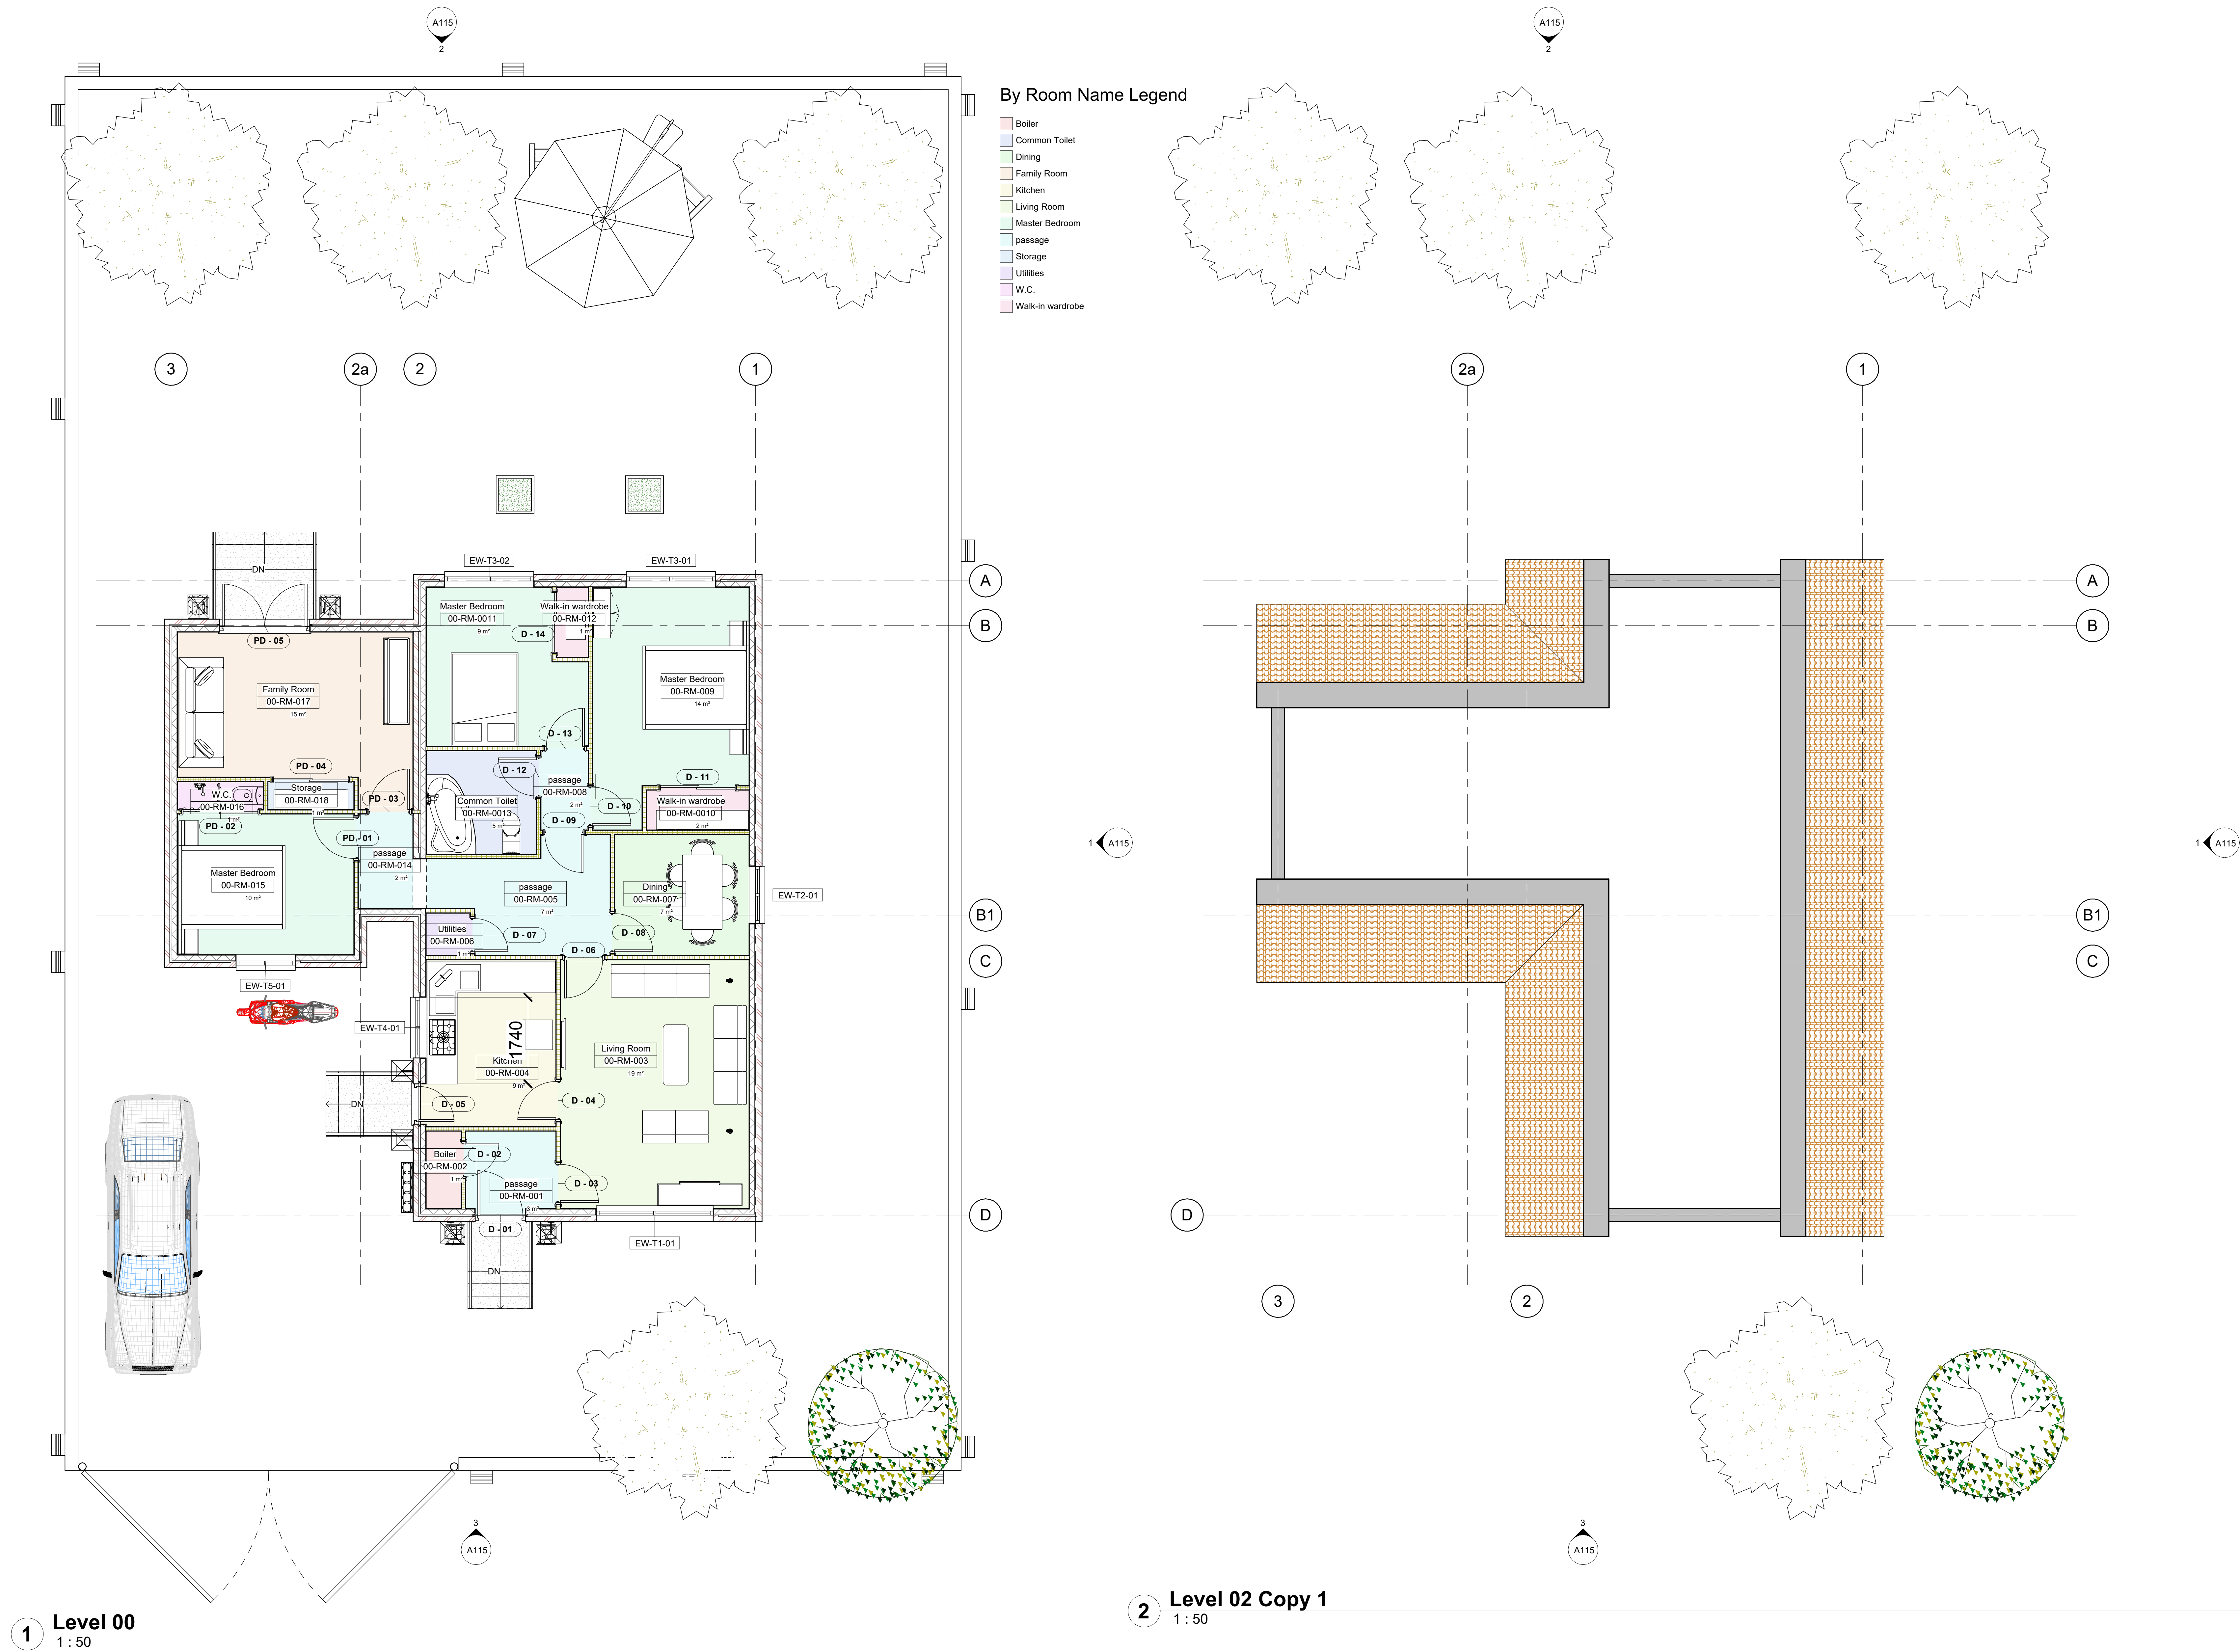
Existing Building Extension Proposal

KIRAN VISHWANATH RAWAL 202474957

University of Strathclyde

24/03/2025 11:59:06

[illegible]

[illegible]

Project Name
**Existing Building Extension
Proposal**

Project Number M3K227048

Drawing Title

Floor Plan

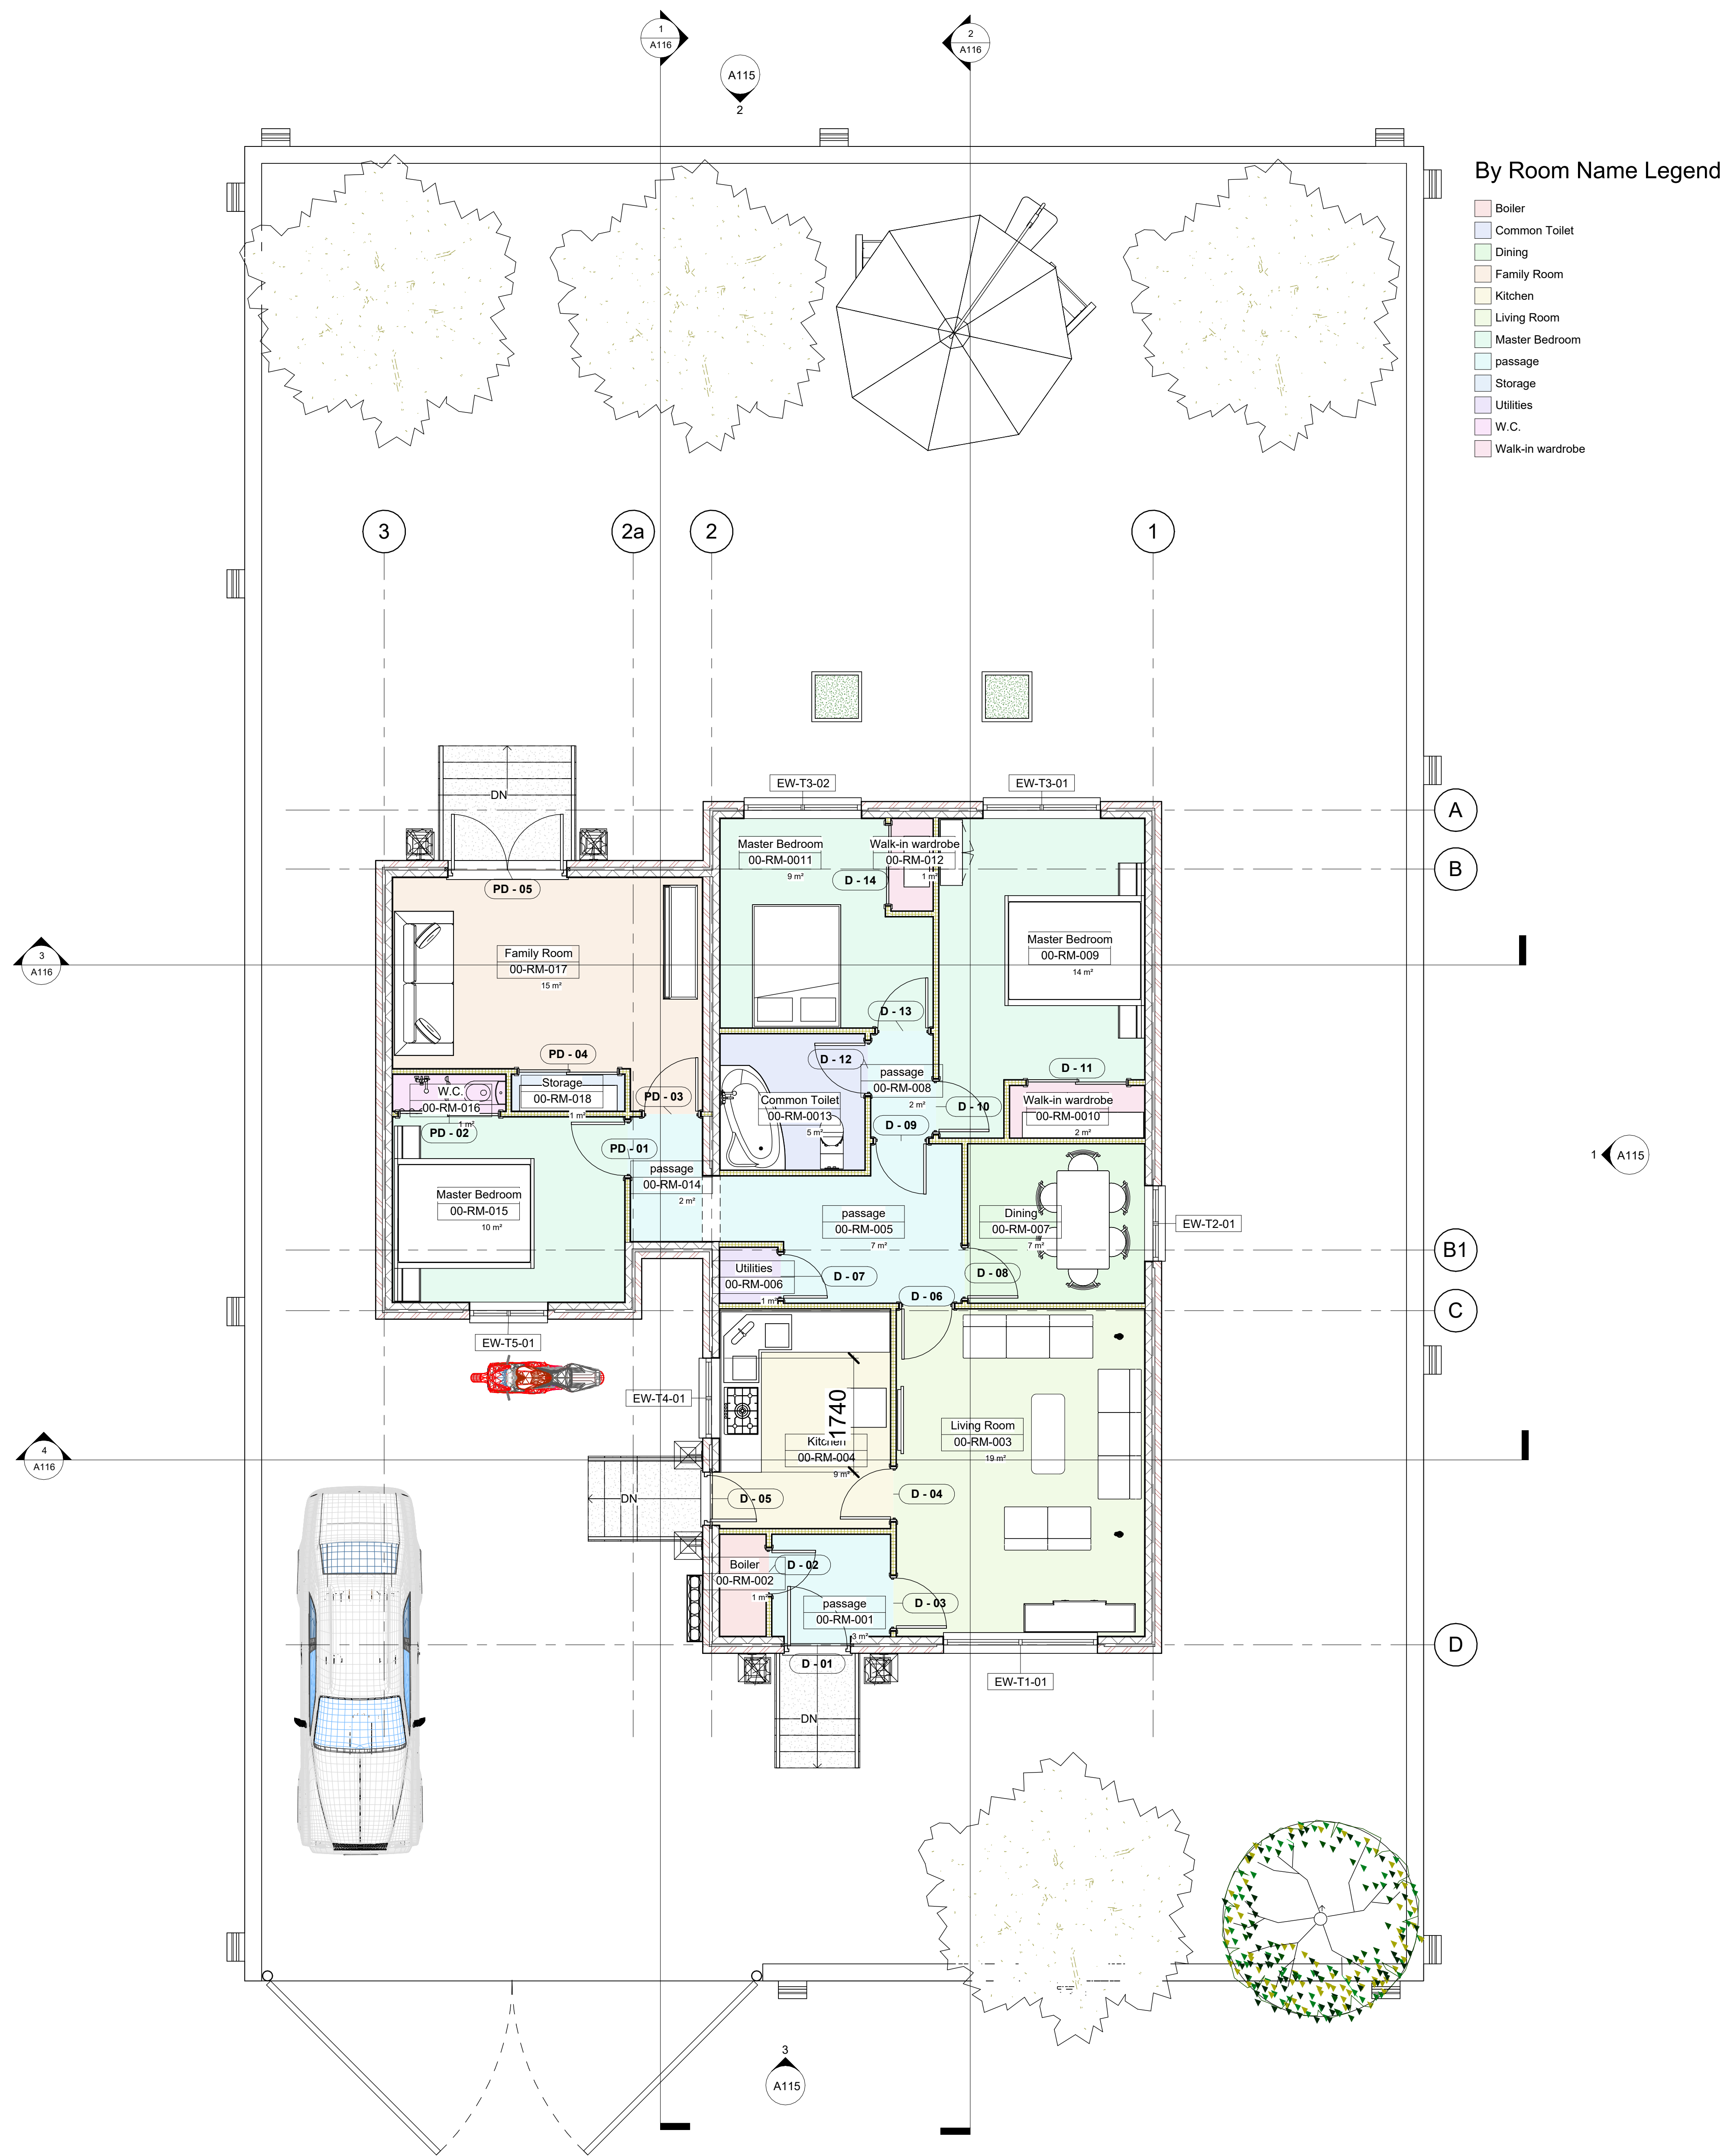
Drawn By KIRAN VISHWANATH
RAWAL 202474957

Checked By University of Strathclyde

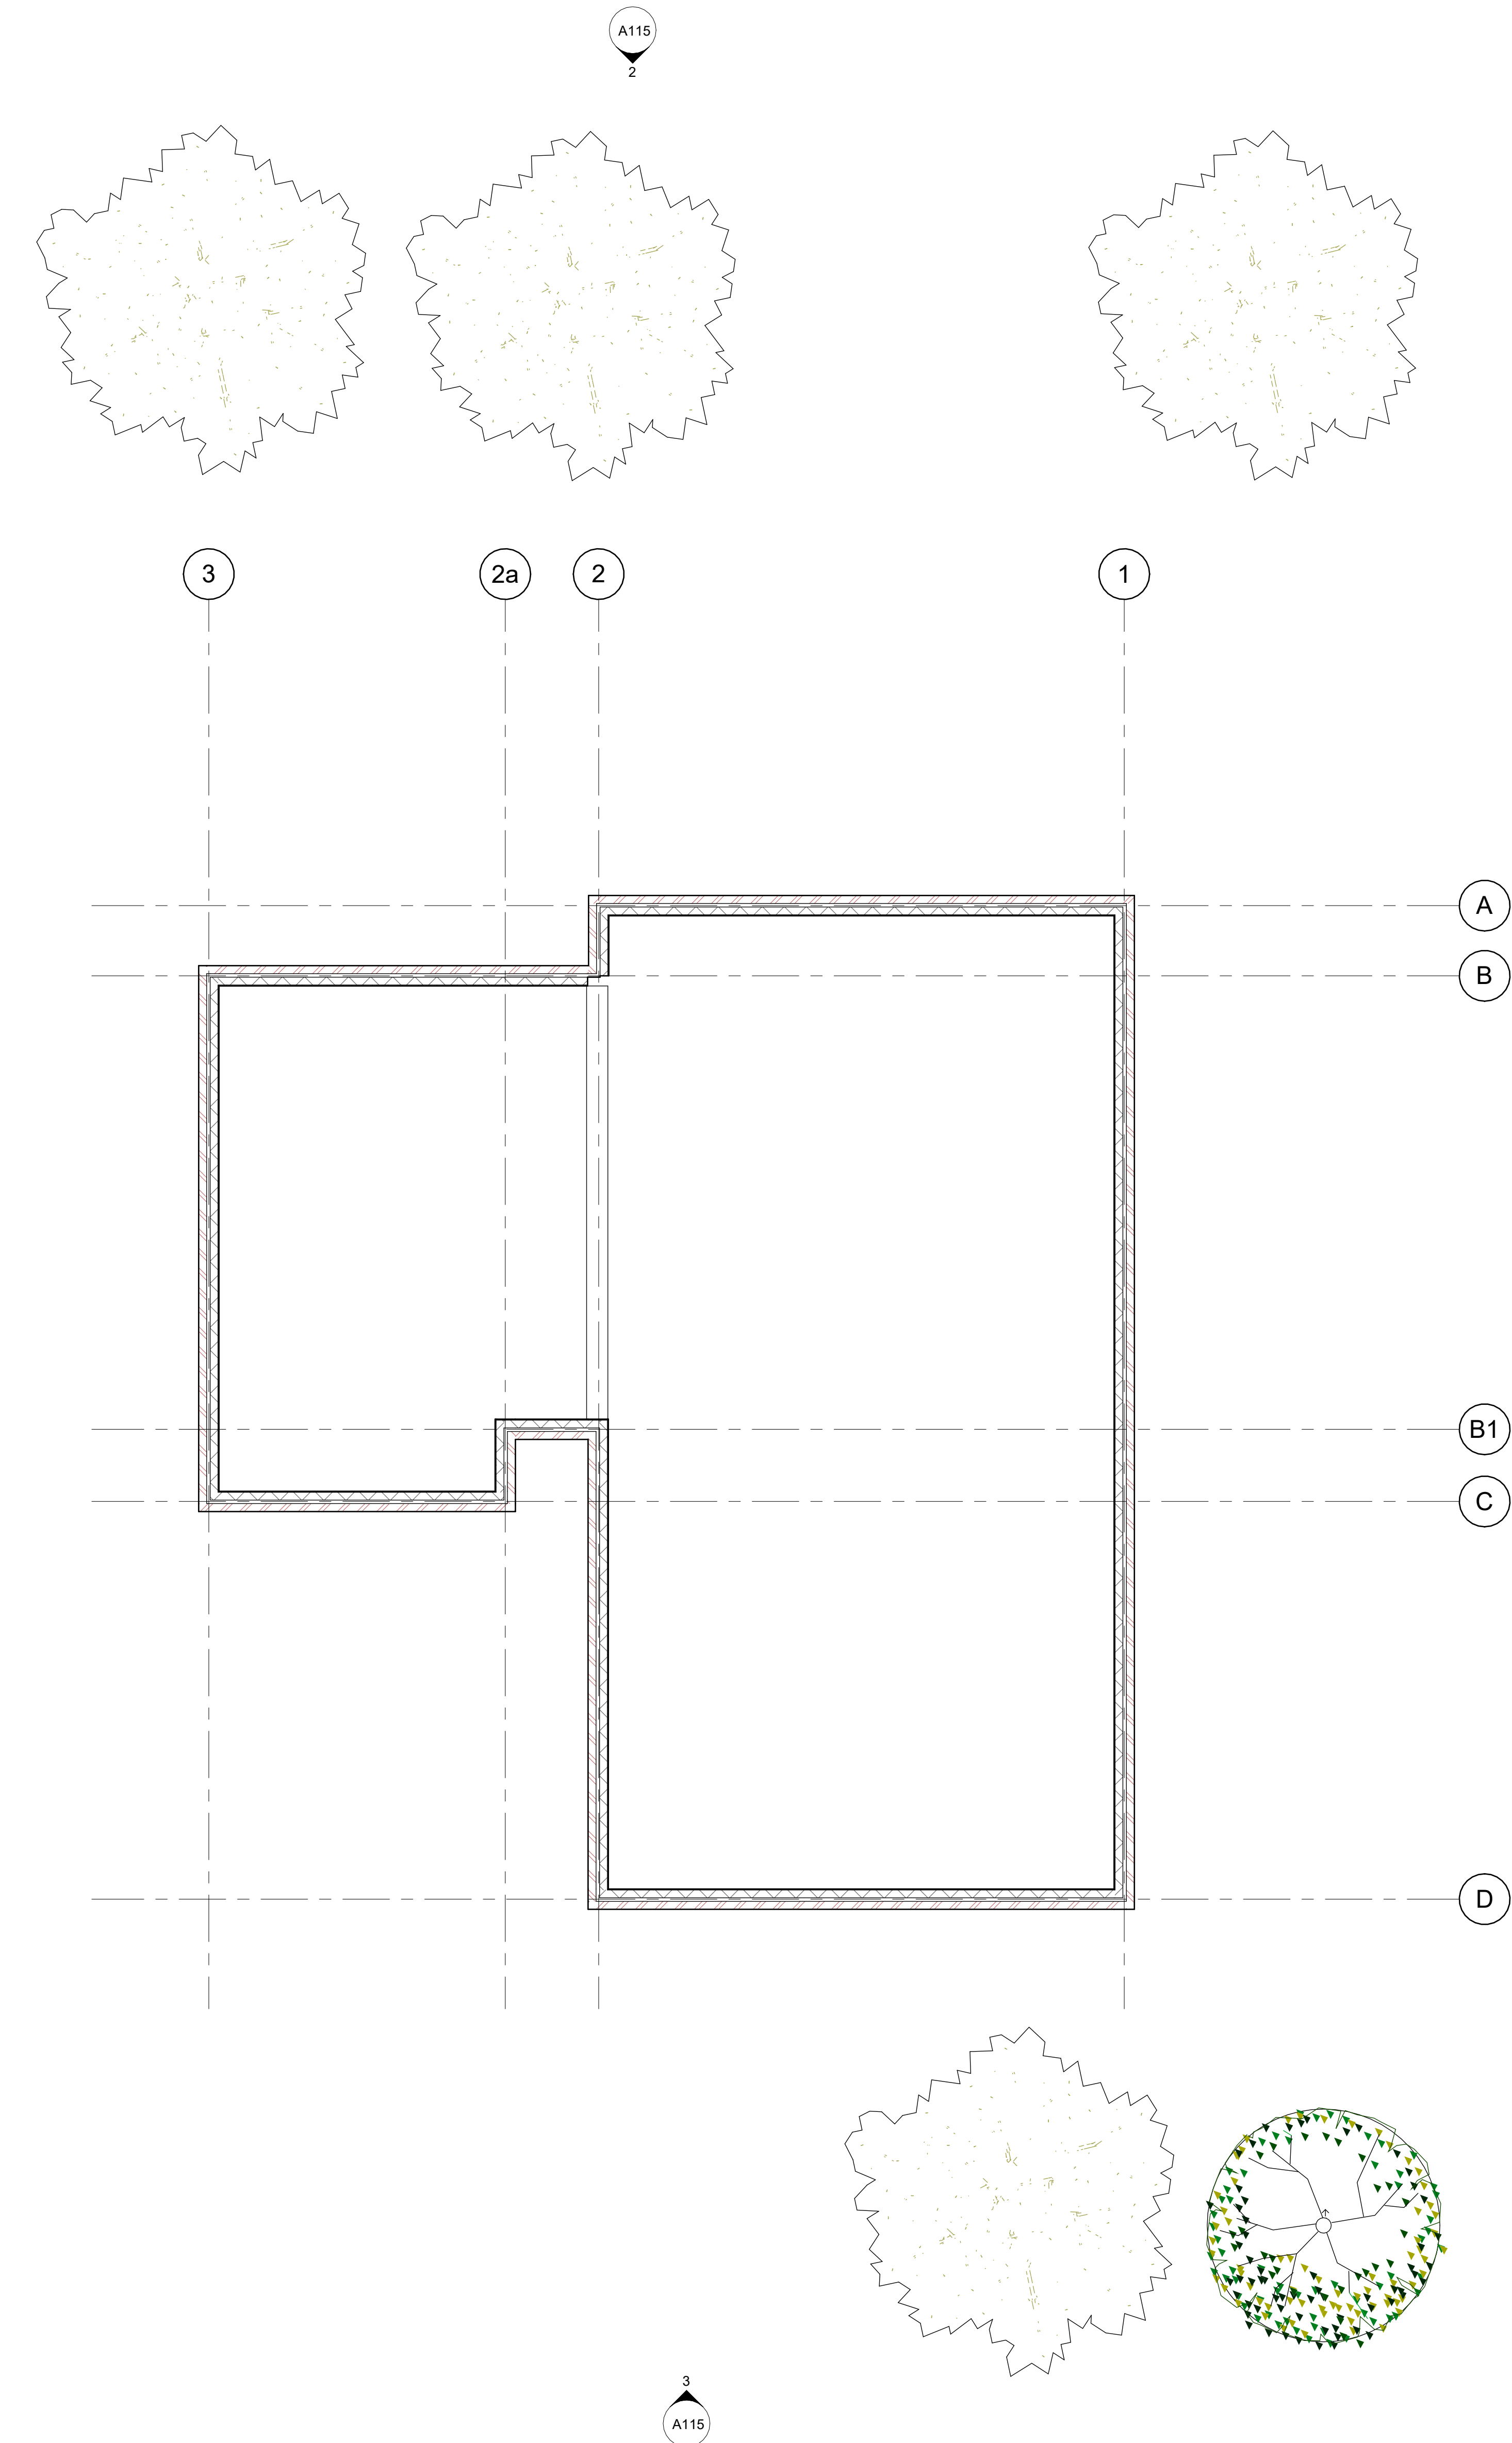
Date 03/24/25

Scale @A0	Sheet Number	A113
-----------	--------------	-------------

1 : 50 Revision



1 Level 00 Section Line
1 : 50



2 Level 01 Copy 1
1 : 50

[illegible]

Project Name
**Existing Building Extension
Proposal**

Project Number	M3K227048
----------------	-----------

Drawing Title

Floor plan

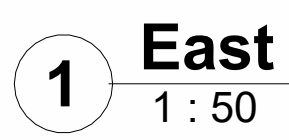
Drawn By **KIRAN VISHWANATH**
RAWAL 202474957

Checked By University of Strathclyde

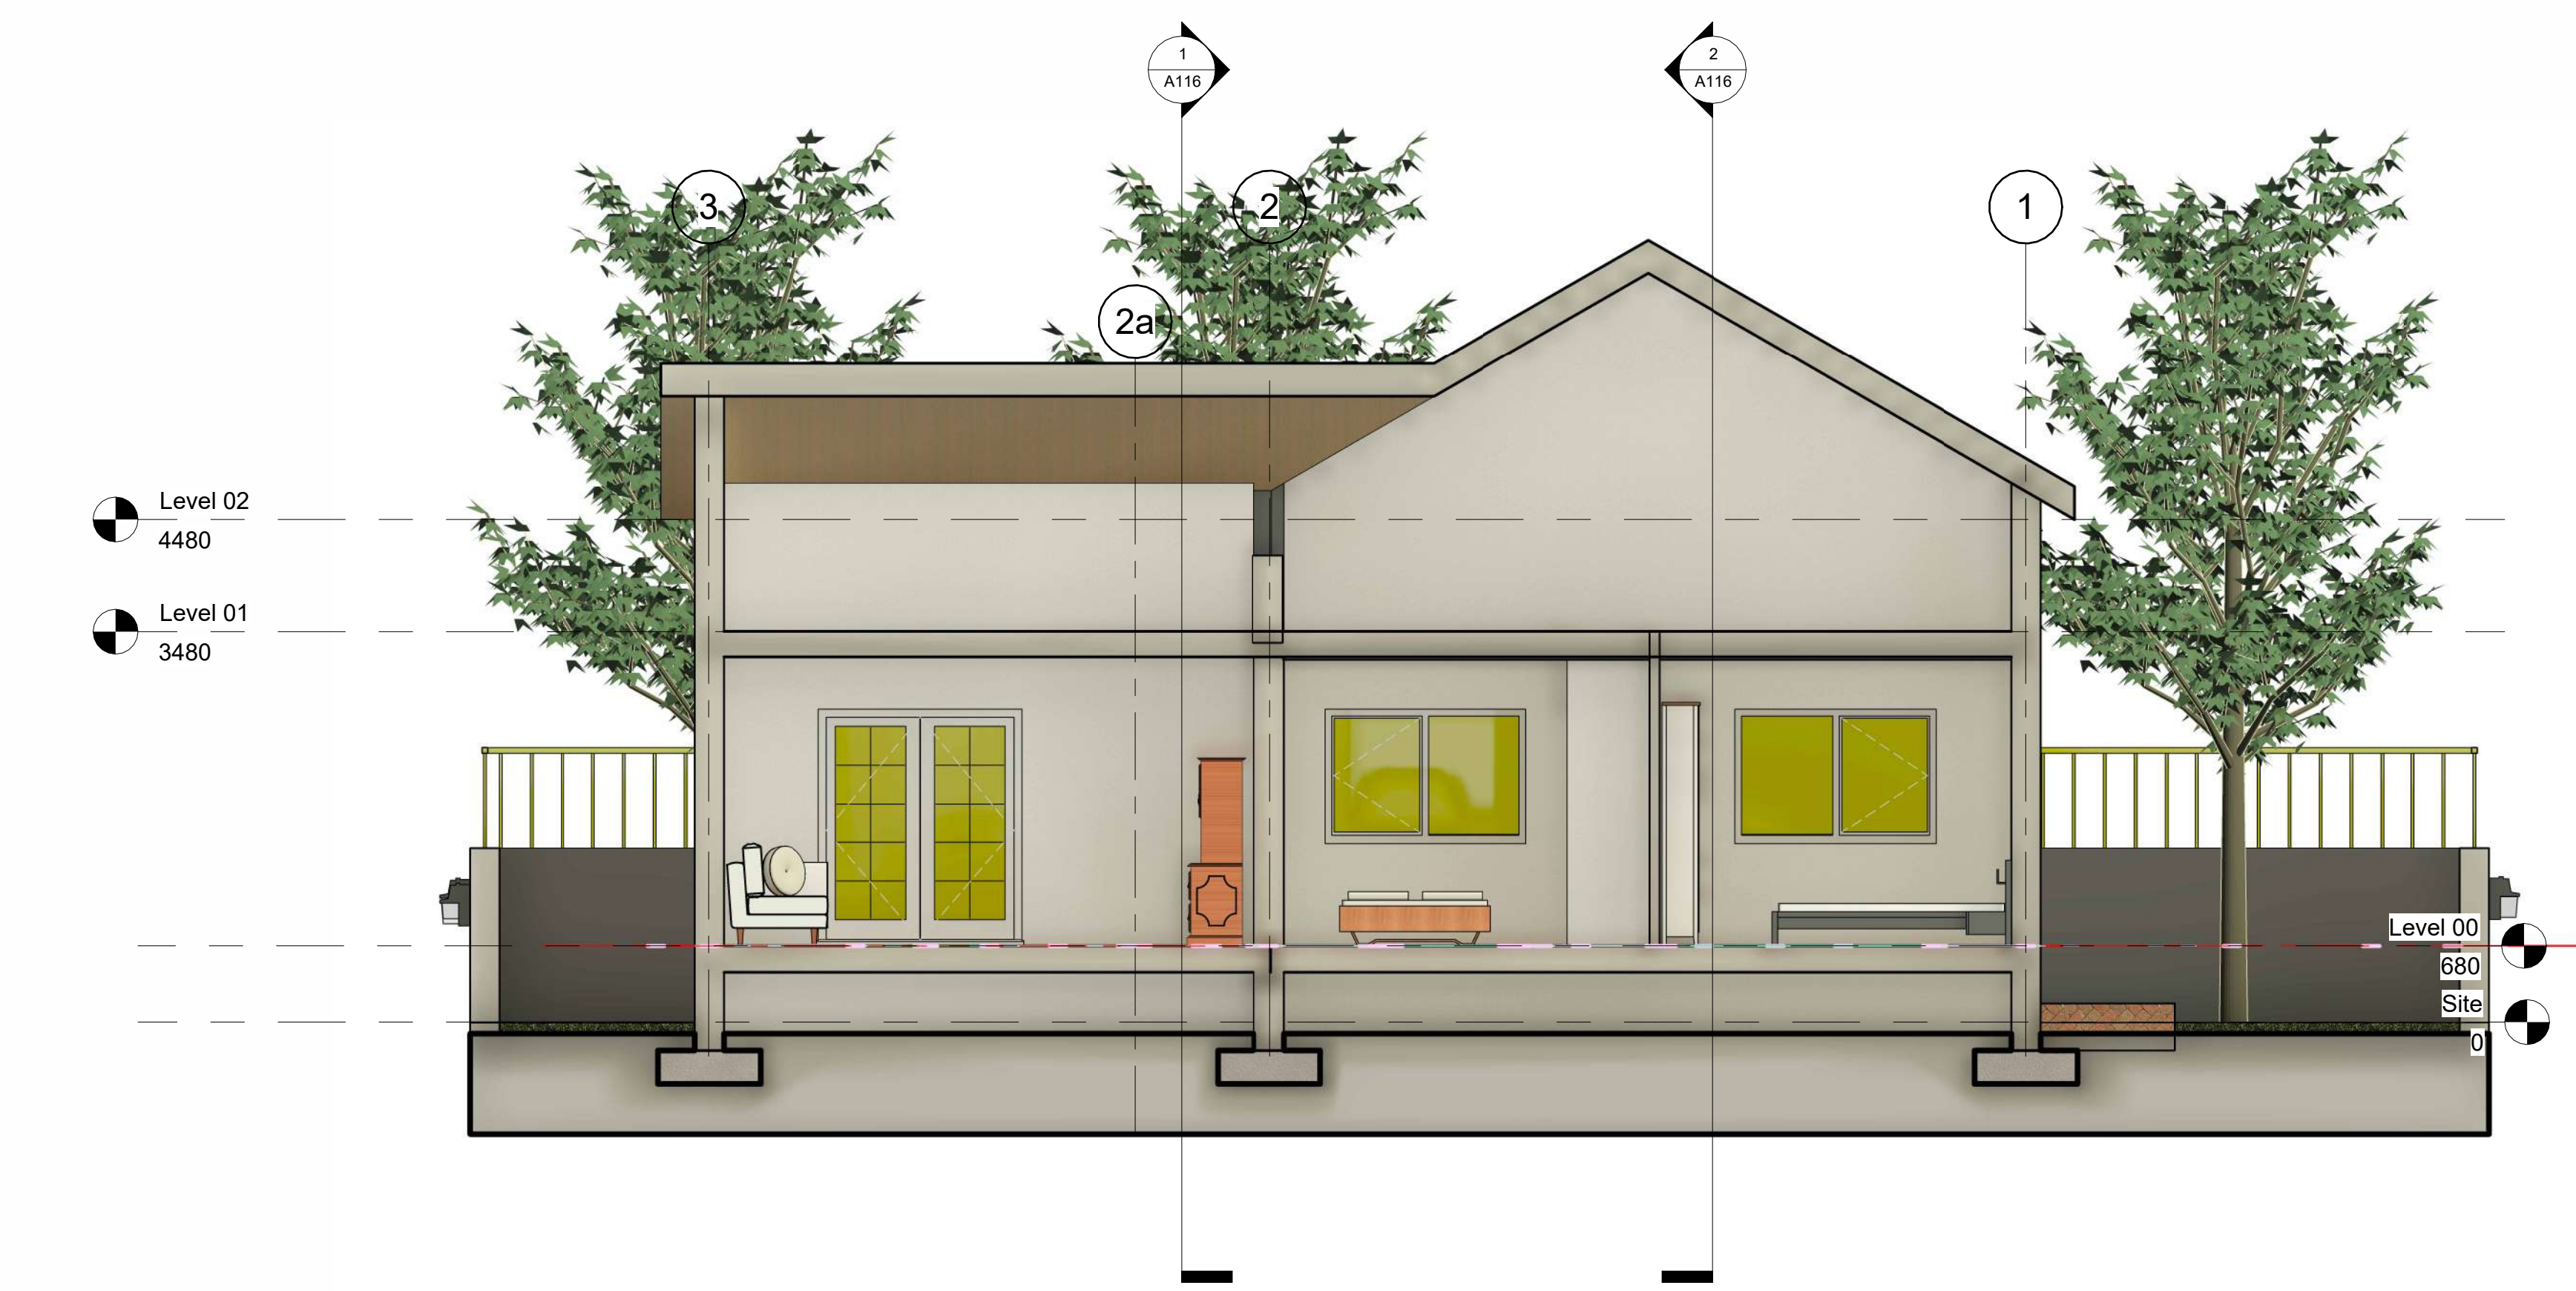
Date 03/24/25

Scale @A0	Sheet Number	A114
-----------	--------------	-------------

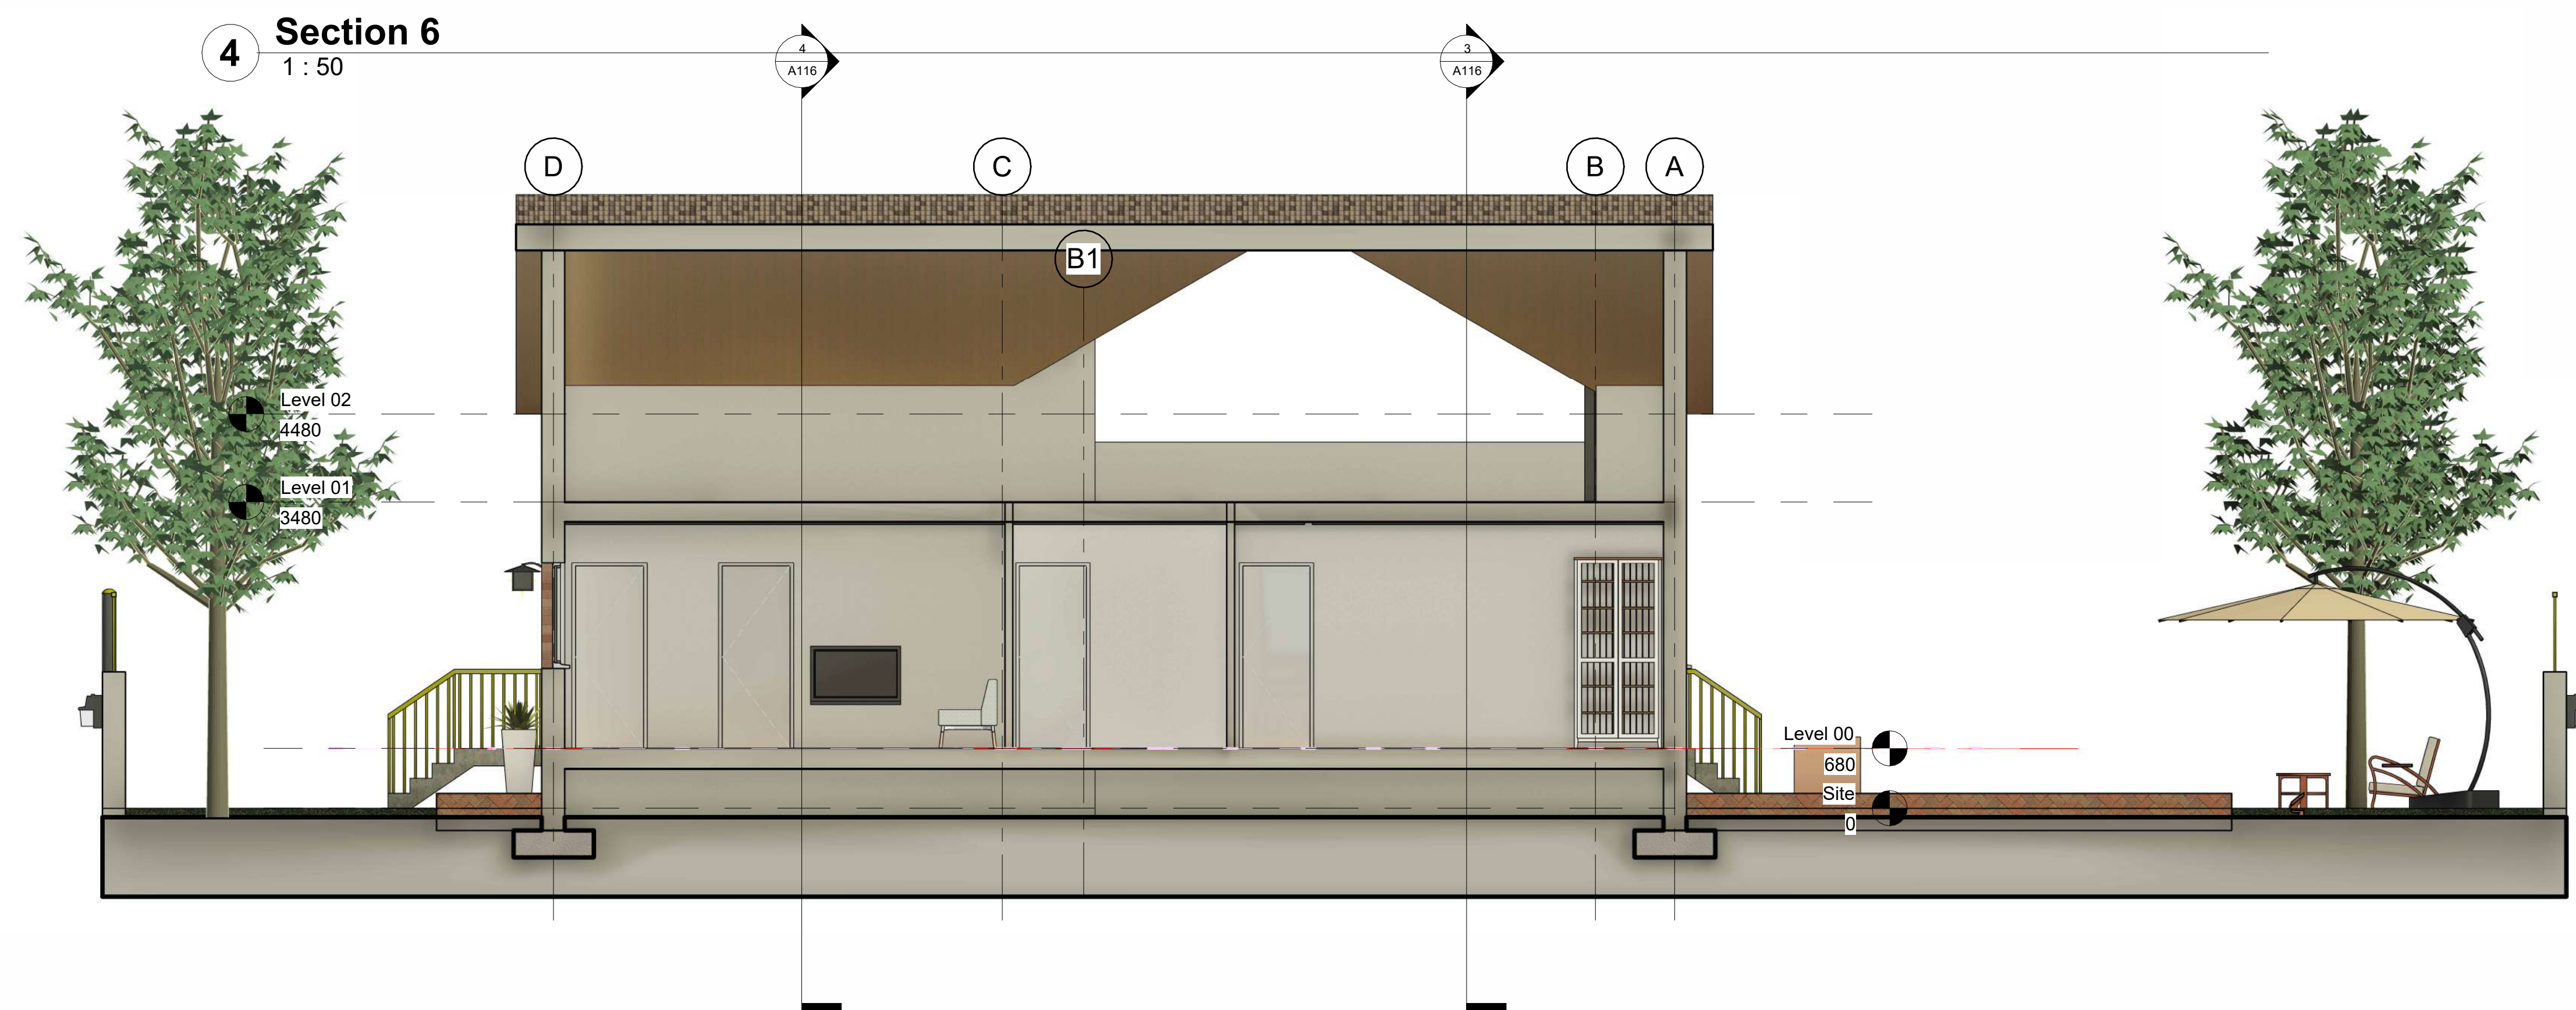
1 : 50	Revision
---------------	----------



Scale @A0	Sheet Number	A115
1 : 50	Revision	



3 **Section 5**
1 : 50



2 Section 3
1 : 50

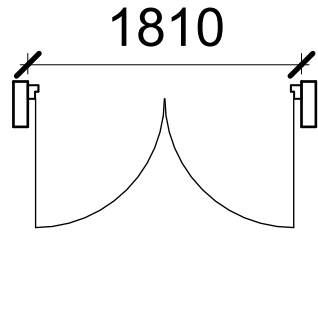
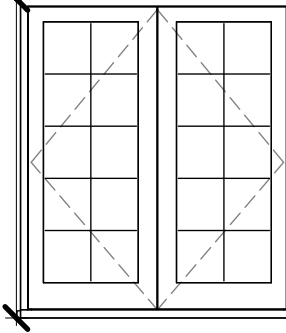
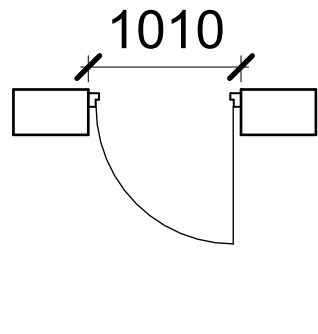
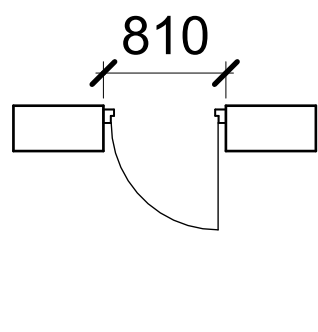
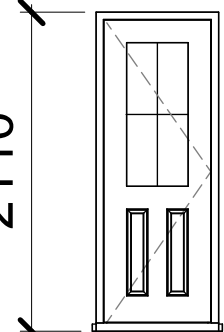
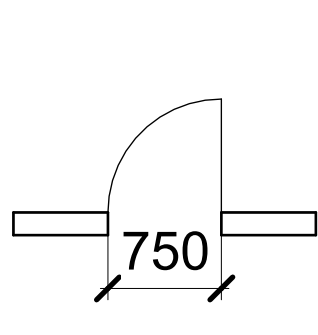
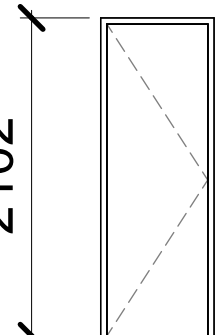
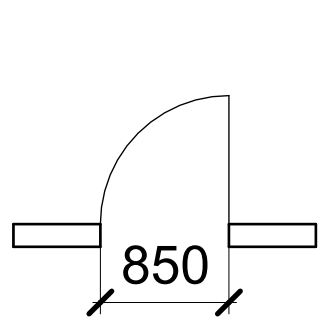
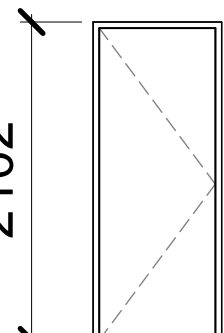
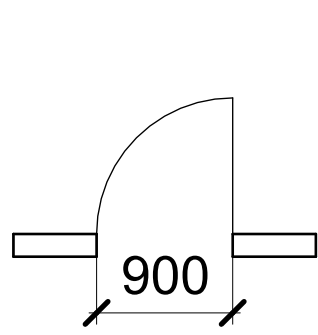
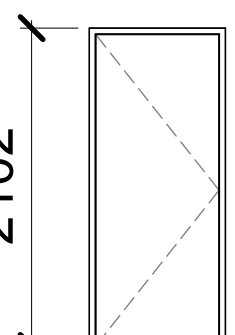
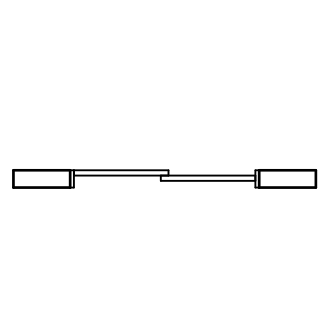
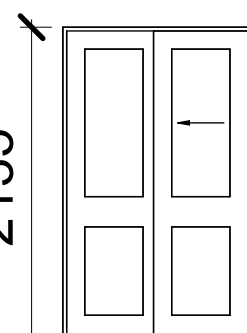
 
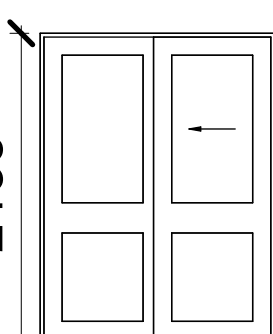
1 : 50 Revision



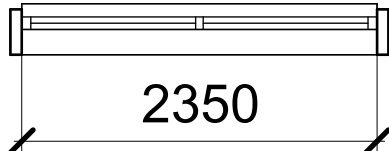
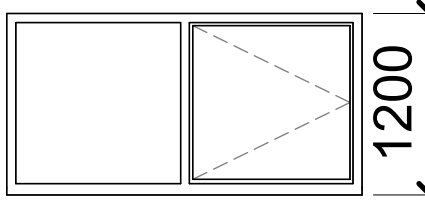
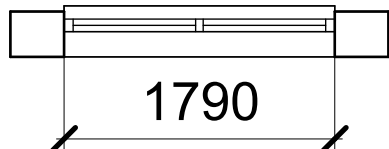
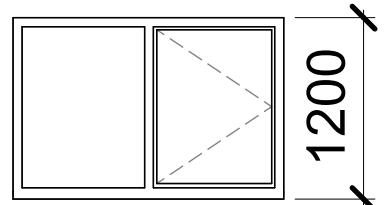
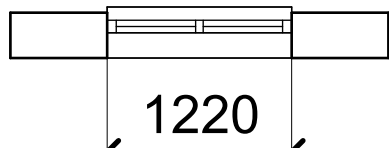
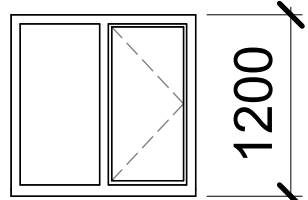
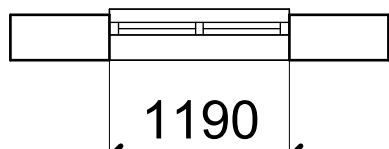
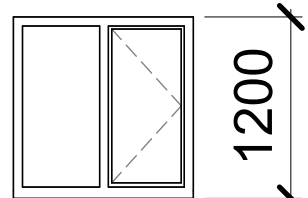
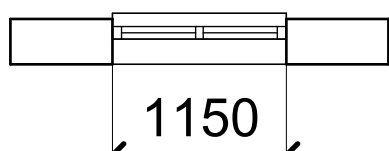
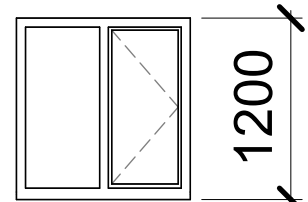
Original Sheet Size A0		
Revision Schedule		
No.	Description	Date
Project Name		
Existing Building Extension Proposal		
Project Number		
M3K227048		
Drawing Title		
3D View Exterior		
Drawn By	KIRAN VISHWANATH RAWAL 202474957	
Checked By	University of Strathclyde	
Date	03/23/25	
Scale @A0	Sheet Number	A117
	Revision	



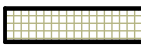
Original Sheet Size A0		
Revision Schedule		
No.	Description	Date
Project Name		
Existing Building Extension Proposal		
Project Number		
M3K227048		
Drawing Title		
3D Interior View		
Drawn By		
KIRAN VISHWANATH RAWAL 202474957		
Checked By		
University of Strathclyde		
Date		
03/23/25		
Scale @A0		
Sheet Number		
A118		
Revision		

Door Legend				
No.	Name	Door No.	Floor View	Elevation View
1.	Door Ext Dbl 1810x2100mm	PD-05		
2.	Door Main 910x2100mm	D-01		
3.	Door 810x2110mm	D-05		
4.	Door 750x2100mm	D-02 D-07		
5.	Door 850x2100mm	D-03 D-04 D-06 D-08 D-09 D-10 D-12 D-13		
6.	Door Ext Dbl 900x2100mm	PD-01 PD-03		
7.	Sliding Door 1200x2100mm	D-14		
8.	Sliding Door 1500x2110mm	PD-02 PD-04 D-11		

door
1 : 50

Window Legend				
No.	Name	Window Nos.	Floor View	Elevation View
1.	Window 2350x1200mm	EW-T1-01		
2.	Window 1790x1200mm	EW-T3-01 EW-T3-02		
3.	Window 1220x1200mm	EW-T4-01		
4.	Window 1190x1200mm	EW-T5-01		
5.	Window 1150x1200mm	EW-T2-01		

Window
1 : 50

Building Component		
No.	Name	Elevation View
1.	Exterior Brick Wall T260MM	
2.	Separate Wall Brick T272.5MM	
3.	Interior Wall Timber Pls 9-T90mm	
4.	Interior Wall Metal Pls 12.5-T90MM	
5.	Ceiling Plasterboard 25MM	
6.	Floor Timber Joist 235MM	
7.	Floor Timber Joist 225MM	
8.	Timber Roof Bat Truss 200. T254MM	

Building Components

1 : 50

MSc/PgDip/PgCert
Advanced Construction
Technologies & BIM

AB991
Building Information Management

Original Sheet Size A1

[illegible]

Project Name

Existing Building Extension Proposal

Project Number

M3K227048

Drawing Title

Legends

Drawn By

KIRAN VISHWANATH
RAWAL 202474957

Checked By

University of Strathclyde

Date

03/24/25

Scale @A1

Sheet Number

1 : 50

Revision

A119

Door Schedule									
Type Mark	Family and Type	Height	Width	Level	Cost	Count	Head Height	Manufacturer	Comments
49	Doors_IntSgl: UoS_Door_IntSgl_900x2110mm	2110	900	Level 00	220.00	2	2110	SCDoors	
59	Door-Opening: Opening 1000mm	0	0	Level 00		1	0		
93	M_Door-Interior-Double-Sliding-2_Panel-Wood: UoS_Door_IntDbISlid_1500x2100mm	2110	1500	Level 00	250.00	3	2110	BandQ	
94	M_Door-Interior-Double-Sliding-2_Panel-Wood: UoS_Door_IntDbISlid_1200x2110mm	2110	1200	Level 00	230.00	1	2110	BandQ	
98	Doors_ExtSgl_6: UoS_ExtSgle_Main_910mmx2110mm	2110	1010	Level 00		1	2110		
99	Doors_ExtSgl_w-Glazing_Bars_2: UoS_ExtSgl_Kitchen_810x2110mm	2110	810	Level 00		1	2110		
100	Doors_ExtDbI_w-Glazing_Bars_1: UoS_Door_ExtDbI_1810x2110mm	2110	1810	Level 00		1	2110		
101	Doors_IntSgl: UoS_Door_IntSgl_850x2110mm	2110	850	Level 00		8	2110	SCDoors	
102	Doors_IntSgl: UoS_Door_IntSgl_750x2110mm	2110	750	Level 00		2	2110	SCDoors	
Grand total: 20									

Window Schedule									
Type Mark	Family and Type	Head Height	Comments	Cost	Level	Height	Width	Manufacturer	Count
55	Windows_Concept_Plain_Dbl: UoS_Win_2350x1200mm	2110		1000.00	Level 00	1200	2350	PVCGlaze	1
62	Windows_Concept_Plain_Dbl: UoS_Win_1220x1200mm	2110		550.00	Level 00	1200	1220	PVCGlaze	1
63	Windows_Concept_Plain_Dbl: UoS_Win_1150x1200mm	2110		450.00	Level 00	1200	1150	PVCGlaze	1
64	Windows_Concept_Plain_Dbl: UoS_Win_1190x1200mm	2110		480.00	Level 00	1200	1190	PVCGlaze	1
65	Windows_Concept_Plain_Dbl: UoS_Win_1790x1200mm	2110		600.00	Level 00	1200	1790	PVCGlaze	2
Grand total: 6									

Room Schedule					
Number	Name	Level	Count	Perimeter	Area
00-RM-017	Family Room	Level 00	1	17558	15 m²
00-RM-016	W.C.	Level 00	1	4842	1 m²
00-RM-018	Storage	Level 00	1	4672	1 m²
00-RM-015	Master Bedroom	Level 00	1	12934	10 m²
00-RM-014	passage	Level 00	1	6444	2 m²
00-RM-005	passage	Level 00	1	12495	7 m²
00-RM-0013	Common Toilet	Level 00	1	8133	5 m²
00-RM-0011	Master Bedroom	Level 00	1	13315	9 m²
00-RM-012	Walk-in wardrobe	Level 00	1	4342	1 m²
00-RM-009	Master Bedroom	Level 00	1	16470	14 m²
00-RM-0010	Walk-in wardrobe	Level 00	1	5962	2 m²
00-RM-007	Dining	Level 00	1	10502	7 m²
00-RM-006	Utilities	Level 00	1	3715	1 m²
00-RM-004	Kitchen	Level 00	1	12155	9 m²
00-RM-003	Living Room	Level 00	1	17600	19 m²
00-RM-001	passage	Level 00	1	6972	3 m²
00-RM-002	Boiler	Level 00	1	4553	1 m²
00-RM-008	passage	Level 00	1	5152	2 m²

View List				
View Name	Title on Sheet	Scale Value	1:	Sheet Number
Family and Type				
North		50	A115	Elevation: 12mm Circle
East		50	A115	Elevation: 12mm Circle
South		50	A115	Elevation: 12mm Circle
Site {3D}		50	A112	Floor Plan: Floor Plan
Level 01		50		3D View: 3D View
Level 00		50	A113	Floor Plan: Floor Plan
Level 00		100		Ceiling Plan: Ceiling Plan
Starting View		50		3D View: 3D View
Level 02		50		Floor Plan: Floor Plan
Level 02		50		Ceiling Plan: Ceiling Plan
Level 02		50		Structural Plan: Structural Plan
3D View 1				3D View: 3D View
3D View 1_1		1		Rendering: Rendering
3D View 2				3D View: 3D View
3D View 2_1		1		Rendering: Rendering
Site Copy 1		50		Floor Plan: Floor Plan
Level 02 Copy 1		50	A113	Floor Plan: Floor Plan
Level 01 Copy 1		50	A114	Floor Plan: Floor Plan
Level 00 Section Line		50	A114	Floor Plan: Floor Plan
Section 1		50	A116	Section: Building Section
3D View 3				3D View: 3D View
3D View 3_1		1		Rendering: Rendering
3D View 3_2		1		Rendering: Rendering
3D View 4		1		Rendering: Rendering
3D View 3_3		1		Rendering: Rendering
3D View 3_4		1		Rendering: Rendering
3D View 3_5		1		Rendering: Rendering
Section 3		50	A116	Section: Building Section
Section 5		50	A116	Section: Building Section
Section 6		50	A116	Section: Building Section
-3D-_1		1		Rendering: Rendering

Original Sheet Size A1		
Revision Schedule		
No.	Description	Date
Project Name		
Existing Building Extension Proposal		
Project Number		
M3K227048		
Drawing Title		
schedule		
Drawn By		
KIRAN VISHWANATH RAWAL 202474957		
Checked By		
University of Strathclyde		
Date		
03/24/25		
Scale @A1	Sheet Number	A120
	Revision	